
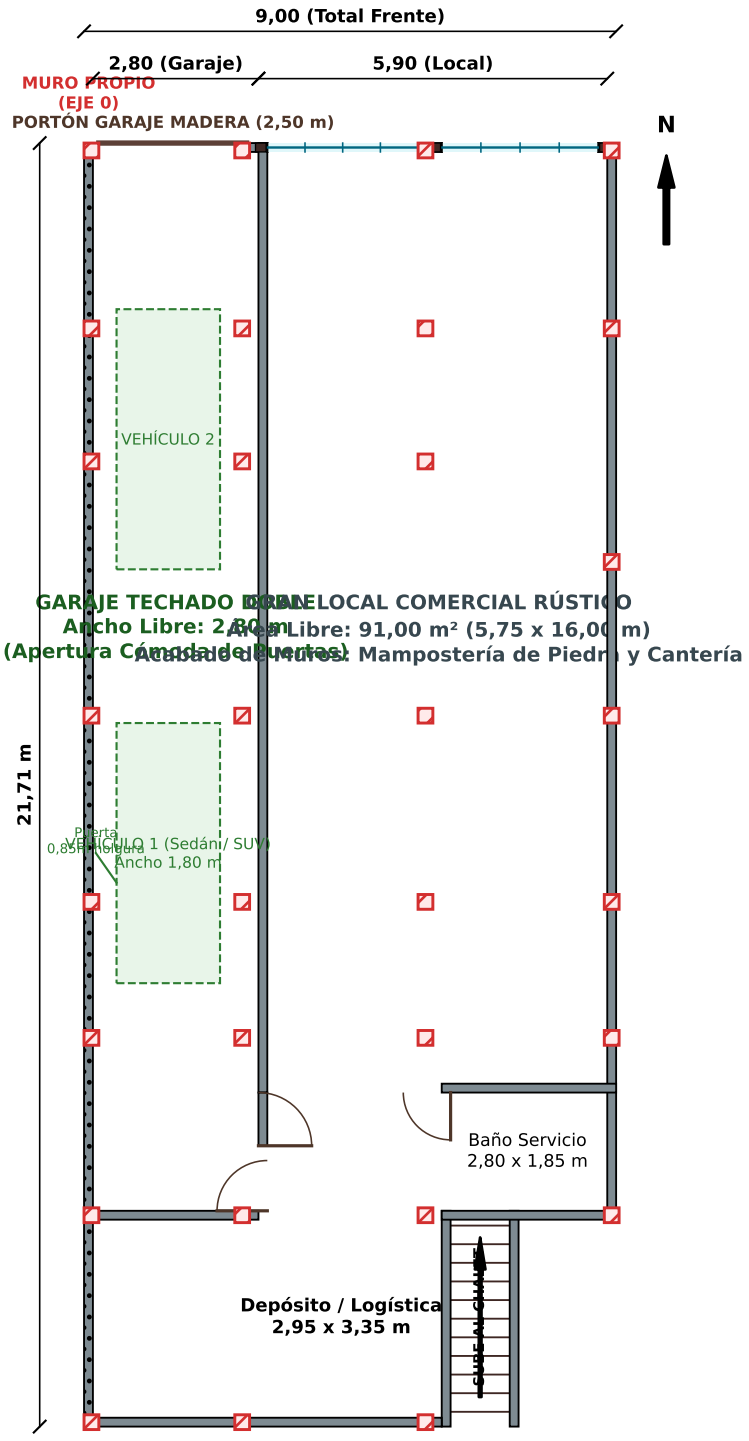


PLANTA BAJA - ZÓCALO RÚSTICO Y GARAJE AMPLIADO (2,80 m LIBRES)

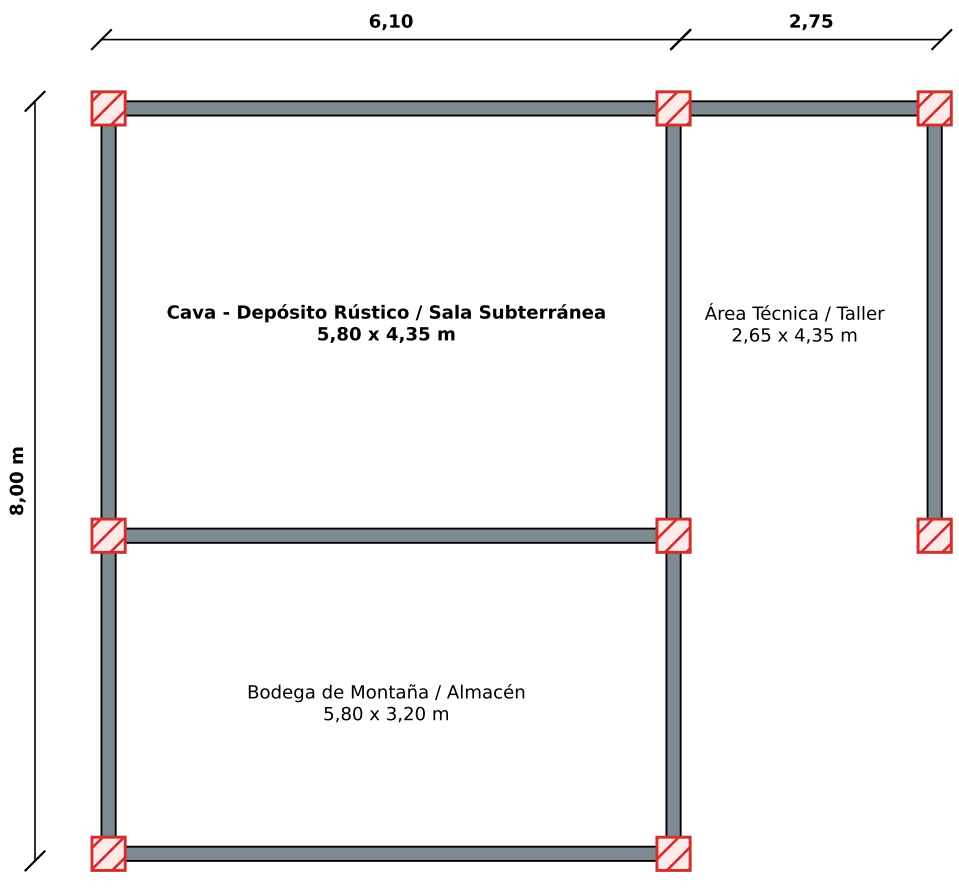


PLANTA SÓTANO (Z = -2,55 m) - FUNDACIÓN Y ESTRUCTURA DE RETENCIÓN

PLANO PLANTA ARQUITECTÓNICA DISTRIBUCIÓN

PLANTA BAJA (ZÓCALO DE MAMPOSTERÍA RÚSTICA) Y SÓTANO.

UBICACIÓN:	PROPIEDAD:	ESPECIALISTA ARQ. RÚSTICA / DIGITALIZO:	REVISADO:	FECHA:	ESCALA:
AVENIDA 4 ENTRE CALLES 30 Y 31 30-7 MUNICIPIO INDEPENDENCIA ESTADO YARACUY.	ALVARO ARGELIO DIAZ FLOREZ. C.I.: 24.633.787	ARQ. ESPECIALISTA CHALET & TIMBER FRAME. T.S.U. ANGEL CAMACARO M. (CVPT 1260)	APROBADO PARA EJECUCIÓN	OCT 2026	1:75

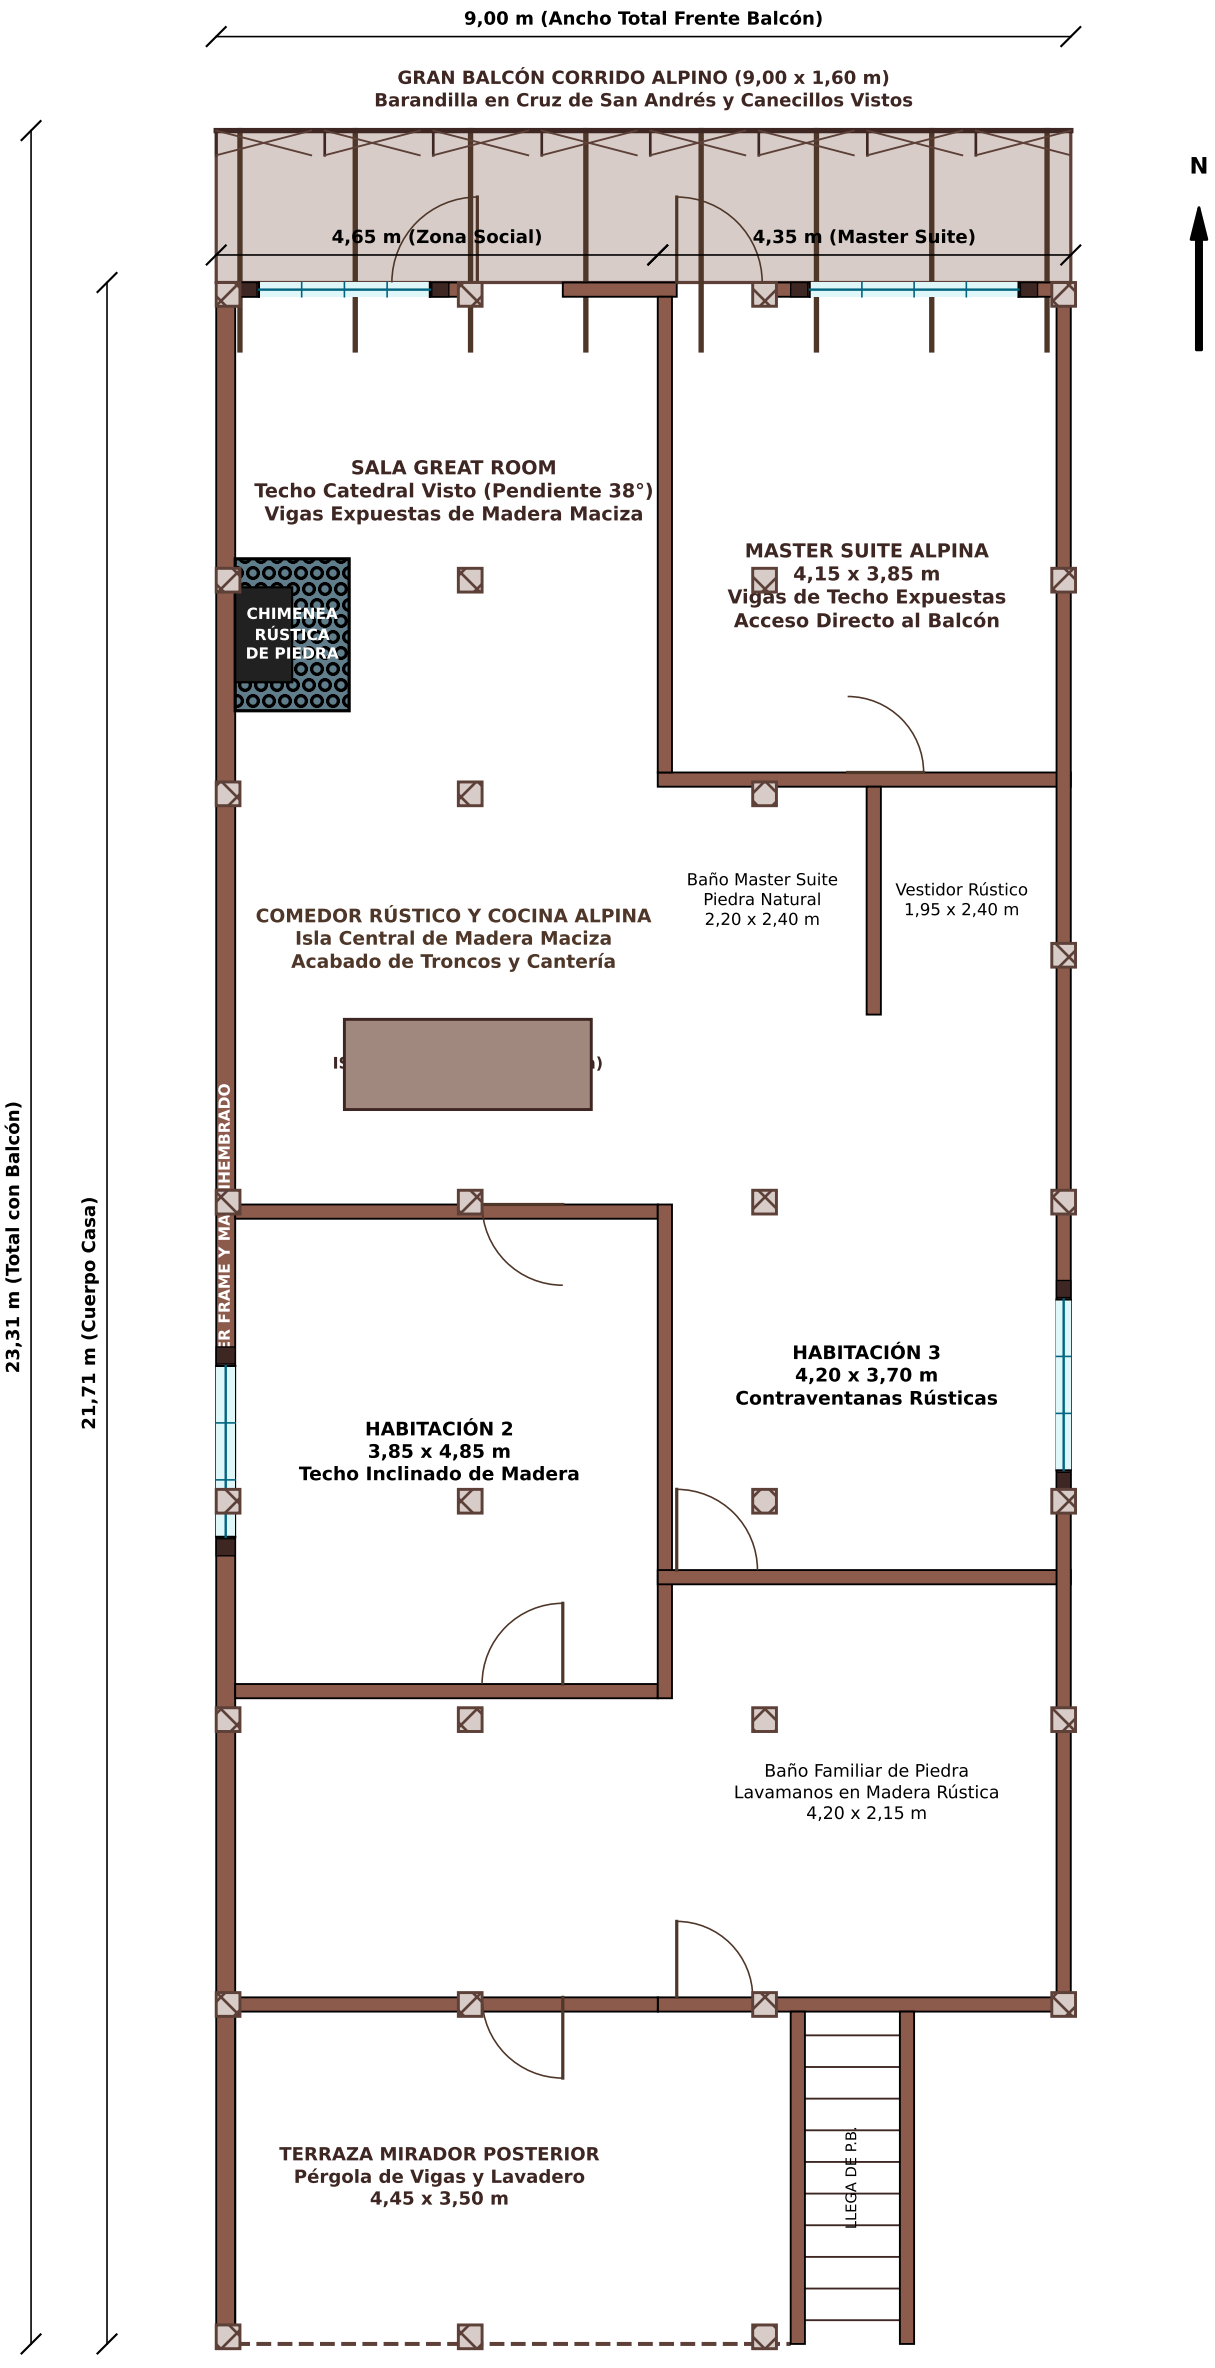

PLANTA ALTA - RESIDENCIA CHALET CON TECHOS DE VIGAS VISTAS Y BALCÓN CORRIDO

PLANO PLANTA ARQUITECTÓNICA DISTRIBUCIÓN - PLANTA ALTA

CHALET RÚSTICO Y ALPINO (TIMBER FRAME, BALCONADA Y CHIMENEA).


UBICACIÓN:	PROPIEDAD:	ESPECIALISTA ARQ. RÚSTICA / DIGITALIZO:	REVISADO:	FECHA:	ESCALA:
AVENIDA 4 ENTRE CALLES 30 Y 31 30-7 MUNICIPIO INDEPENDENCIA ESTADO YARACUY.	ALVARO ARGELIO DIAZ FLOREZ. C.I.: 24.633.787	ARQ. ESPECIALISTA CHALET & TIMBER FRAME. T.S.U. ANGEL CAMACARO M. (CVPT 1260)	APROBADO PARA EJECUCIÓN	OCT 2026	1:75

REPÚBLICA BOLIVARIANA DE VENEZUELA

MUNICIPIO INDEPENDENCIA YARACUY

PROYECTO CHALET RÚSTICO Y ALPINO (TIMBER FRAME)

DISEÑO PARAMÉTRICO OPENCAD / OPENSCAD

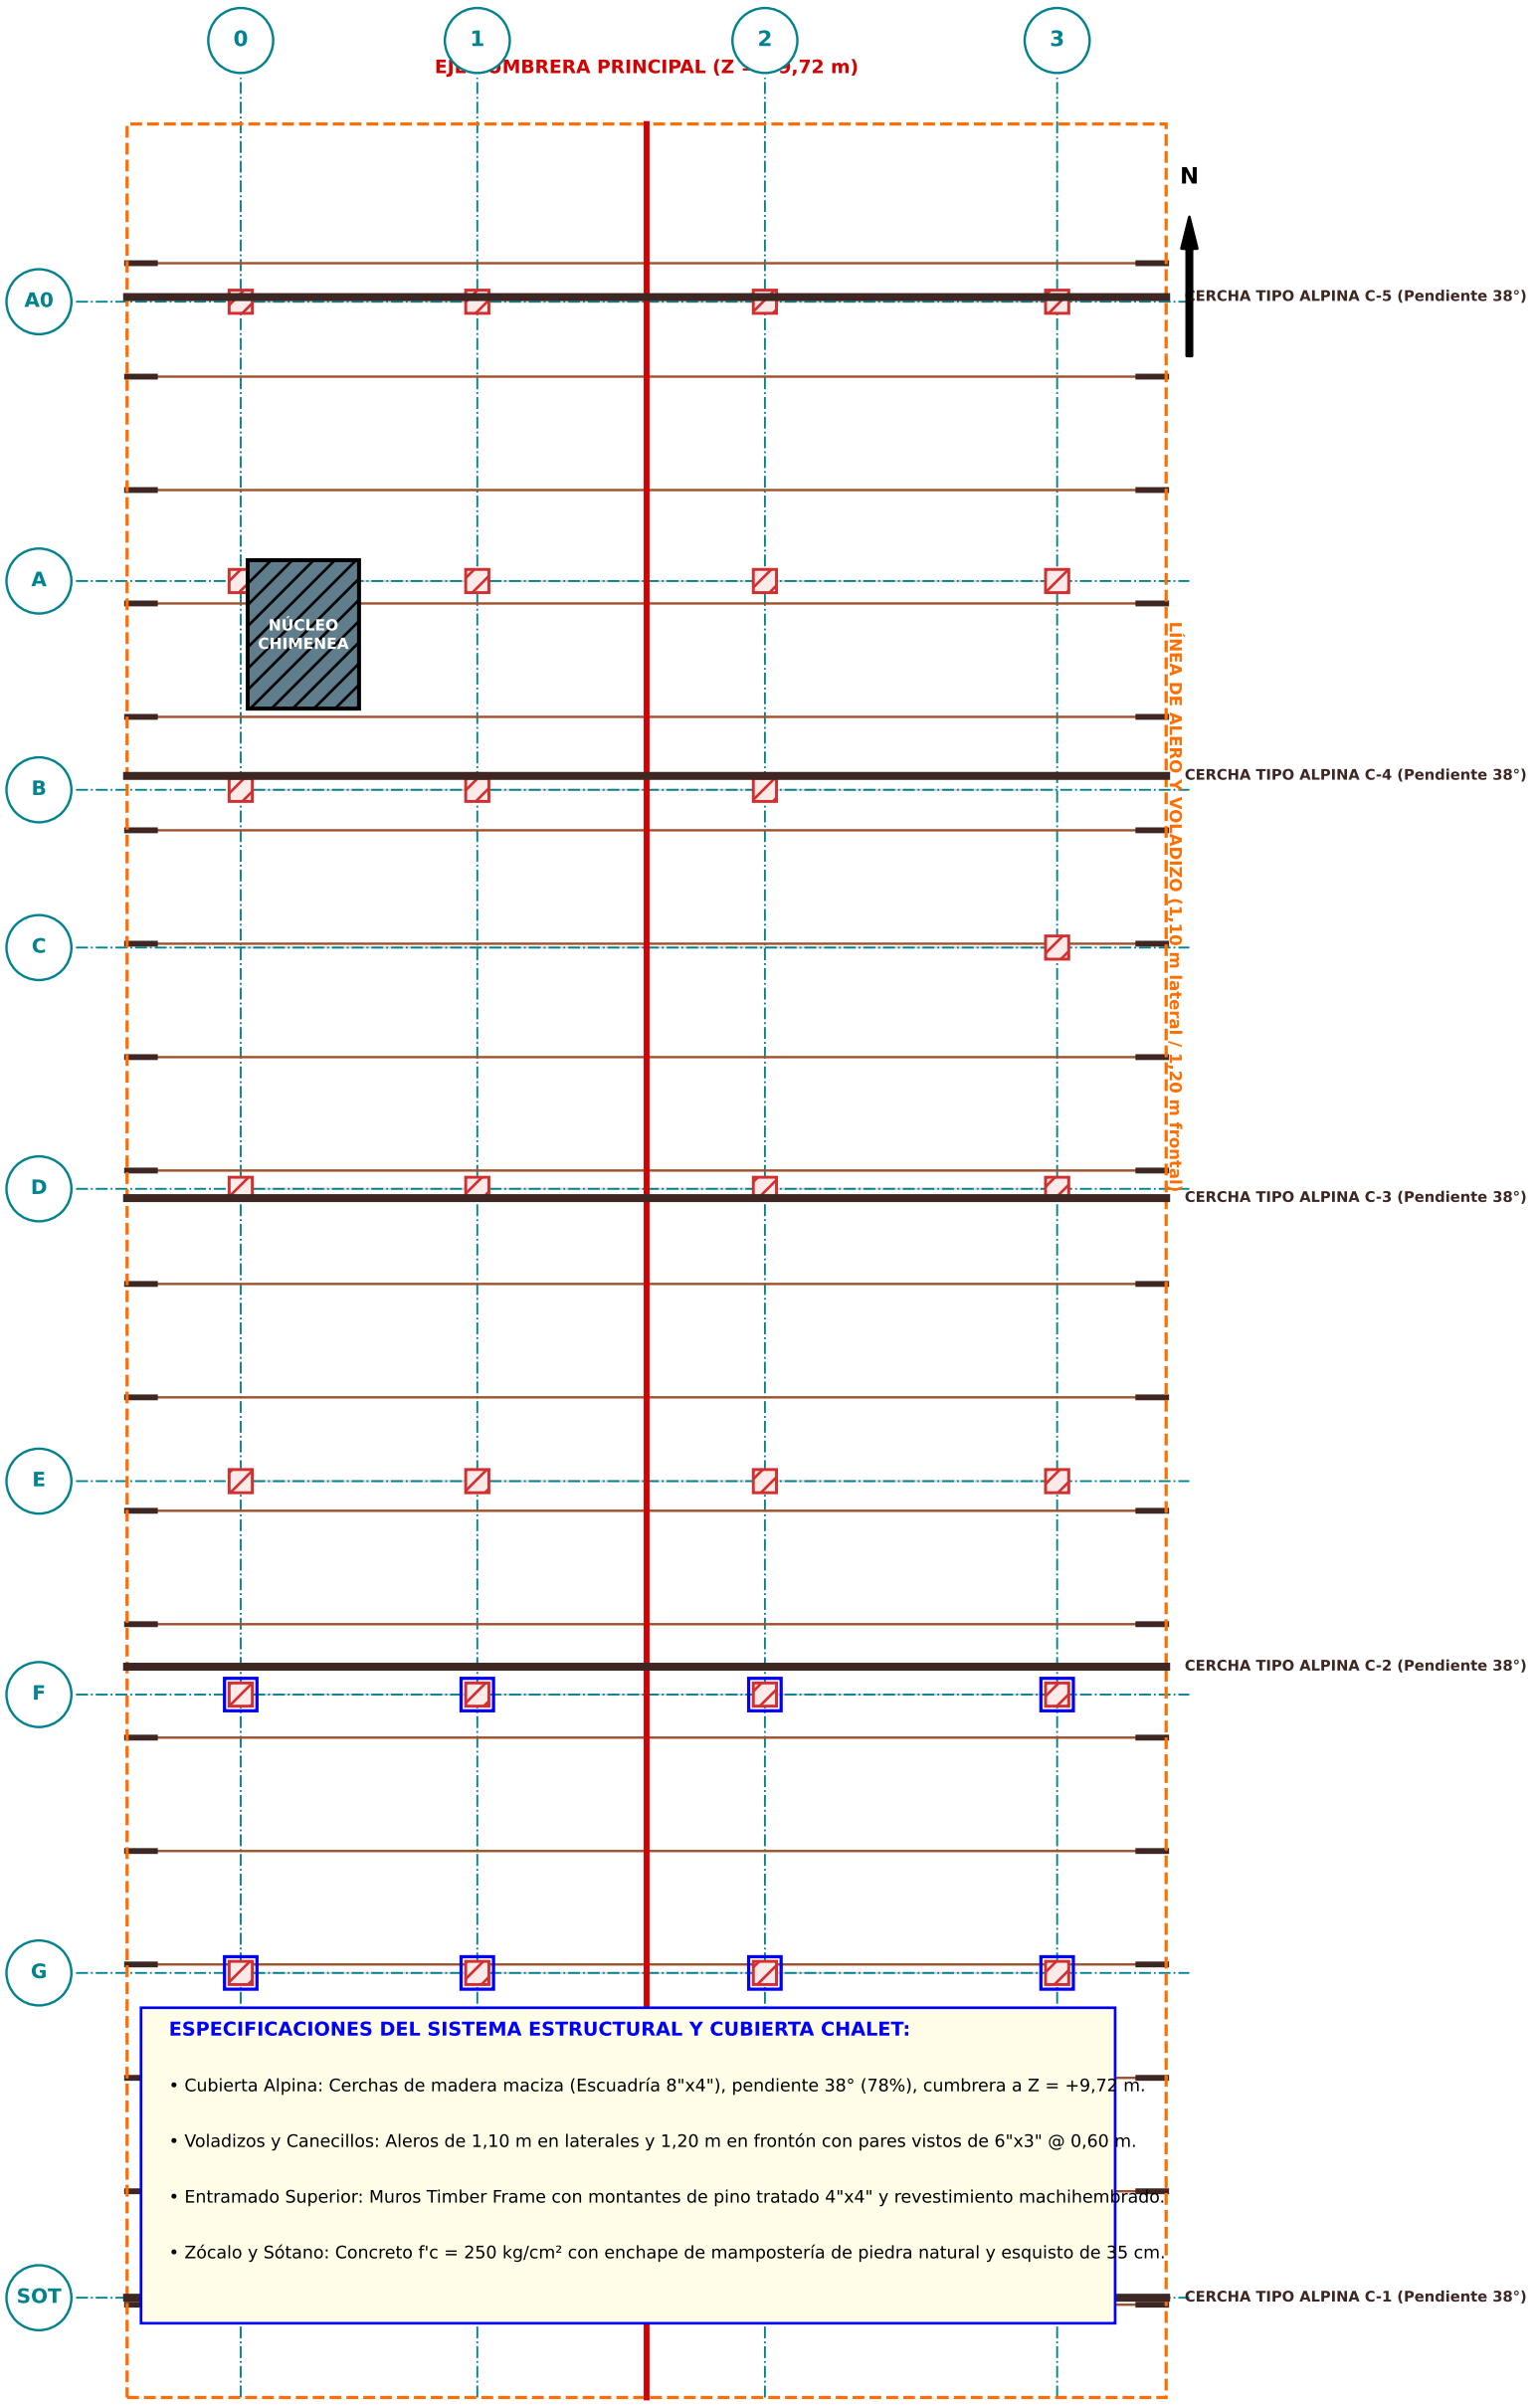

ESPECIFICACIONES DEL SISTEMA ESTRUCTURAL Y CUBIERTA CHALET:

- Cubierta Alpina: Cerchas de madera maciza (Escuadría 8"x4"), pendiente 38° (78%), cumbrera a Z = +9,72 m.
- Voladizos y Canecillos: Aleros de 1,10 m en laterales y 1,20 m en frontón con pares vistos de 6"x3" @ 0,60 m.
- Entramado Superior: Muros Timber Frame con montantes de pino tratado 4"x4" y revestimiento machihembrado.
- Zócalo y Sótano: Concreto f'c = 250 kg/cm² con enchape de mampostería de piedra natural y esquisto de 35 cm.

SISTEMA ESTRUCTURAL HÍBRIDO: ZÓCALO DE HORMIGÓN/PIEDRA + TIMBER FRAME + CERCHAS 38°


PLANO ESTRUCTURAL Y SISTEMA DE CUBIERTA ALPINA

ENTRAMADO DE VIGAS VISTAS, CERCHAS A DOS AGUAS Y TIJERAS DE MADERA.


UBICACIÓN:	PROPIEDAD:	ESPECIALISTA ARQ. RÚSTICA / DIGITALIZO:	REVISADO:	FECHA:	ESCALA:
AVENIDA 4 ENTRE CALLES 30 Y 31 30-7 MUNICIPIO INDEPENDENCIA ESTADO YARACUY.	ALVARO ARGELIO DIAZ FLOREZ. C.I.: 24.633.787	ARQ. ESPECIALISTA CHALET & TIMBER FRAME T.S.U. ANGEL CAMACARO M. (CVPT 1260)	APROBADO PARA EJECUCIÓN	OCT 2026	1:75

REPÚBLICA BOLIVARIANA DE VENEZUELA
MUNICIPIO INDEPENDENCIA YARACUY


PROYECTO CHALET RÚSTICO Y ALPINO (TIMBER FRAME)
DISEÑO PARAMÉTRICO OPENCAD / OPENSCAD

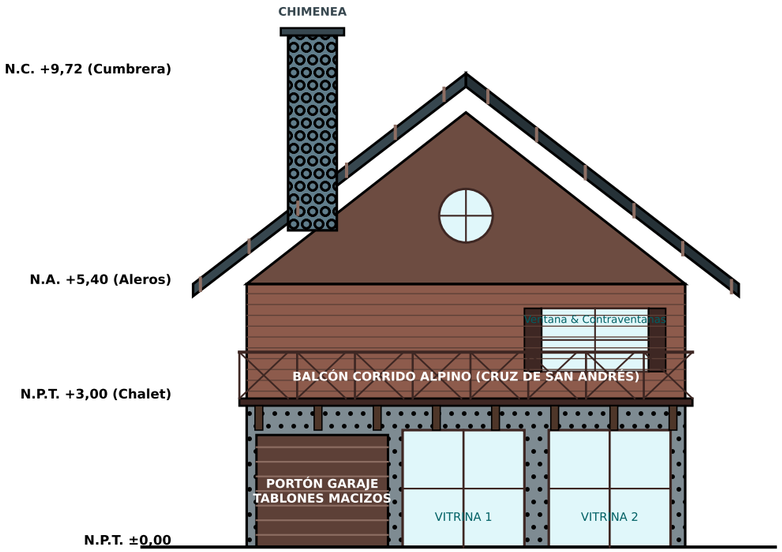

FACHADA PRINCIPAL (AVENIDA 4) - ESTILO CHALET ALPINO

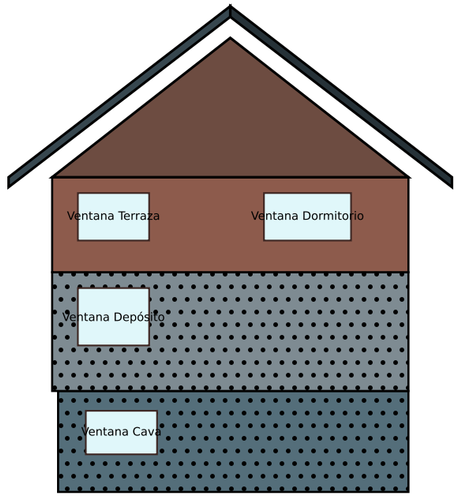

FACHADA ~~POSTERIOR (SÓTANO - ZÓCALO~~ - CHALET)

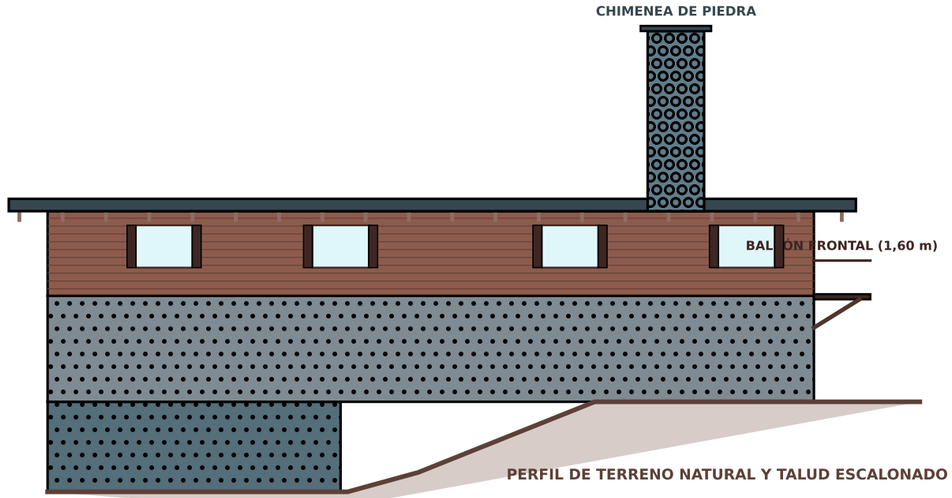

FACHADA LATERAL IZQUIERDA (SÓTANO + ZÓCALO MAMPOSTERÍA + CUERPO TIMBER FRAME + CHIMENEA)

PLANO FACHADAS Y ELEVACIONES RÚSTICAS (CHALET ALPINO)
FACHADA PRINCIPAL (AV. 4) — FACHADA LATERAL CON TALUD — FACHADA POSTERIOR.

UBICACIÓN:	PROPIEDAD:	ESPECIALISTA ARQ. RUSTICA / DIGITALIZO:	REVISADO:	FECHA:	ESCALA:
AVENIDA 4 ENTRE CALLES 30 Y 31 30-7 MUNICIPIO INDEPENDENCIA ESTADO YARACUY.	ALVARO ARGELIO DIAZ FLOREZ. C.I.: 24.633.787	ARQ. ESPECIALISTA CHALET & TIMBER FRAME T.S.U. ANGEL CAMACARO M. (CVPT 1260)	APROBADO PARA EJECUCIÓN	OCT 2026	1:75

REPÚBLICA BOLIVARIANA DE VENEZUELA
MUNICIPIO INDEPENDENCIA YARACUY

PROYECTO CHALET RÚSTICO Y ALPINO (TIMBER FRAME)


DISEÑO PARAMÉTRICO OPENCAD / OPENSCAD

CUADRO DE COORDENADAS U.T.M. (REGVEN / WGS84)

LADO EST-PV	RUMBO	DISTANCIA	P	NORTE	ESTE
1 - 2	N 57°10'22.40" E	11.37 m	1	1.141.664,17	529.755,04
2 - 3	S 30°17'59.36" E	24.72 m	2	1.141.670,33	529.764,60
3 - 4	S 57°10'22.40" W	10.81 m	3	1.141.648,99	529.777,07
4 - 1	N 31°36'27.01" W	24.70 m	4	1.141.643,13	529.767,99

LINDEROS

LINDERO	COLINDANTE
NORESTE	CASA DE MIGUEL RODRIGUEZ
SURESTE	SOLAR DE MIGUEL RODRIGUEZ
NOROESTE	AVENIDA 4
SUROESTE	CASA DE MARIO GRATEROL

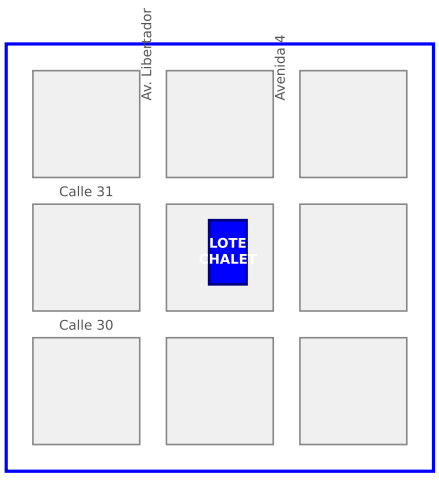


SITUACIÓN RELATIVA S/ESC.

ÁREA DE TERRENO: 273,81 m²

ÁREA DE CONSTRUCCIÓN TOTAL: 372,50 m²

- Planta Baja (Zócalo Mampostería y Garaje 2,80 m): 149,85 m²
- Planta Alta (Residencia Chalet Timber Frame): 142,20 m² | Sótano: 80,45 m²

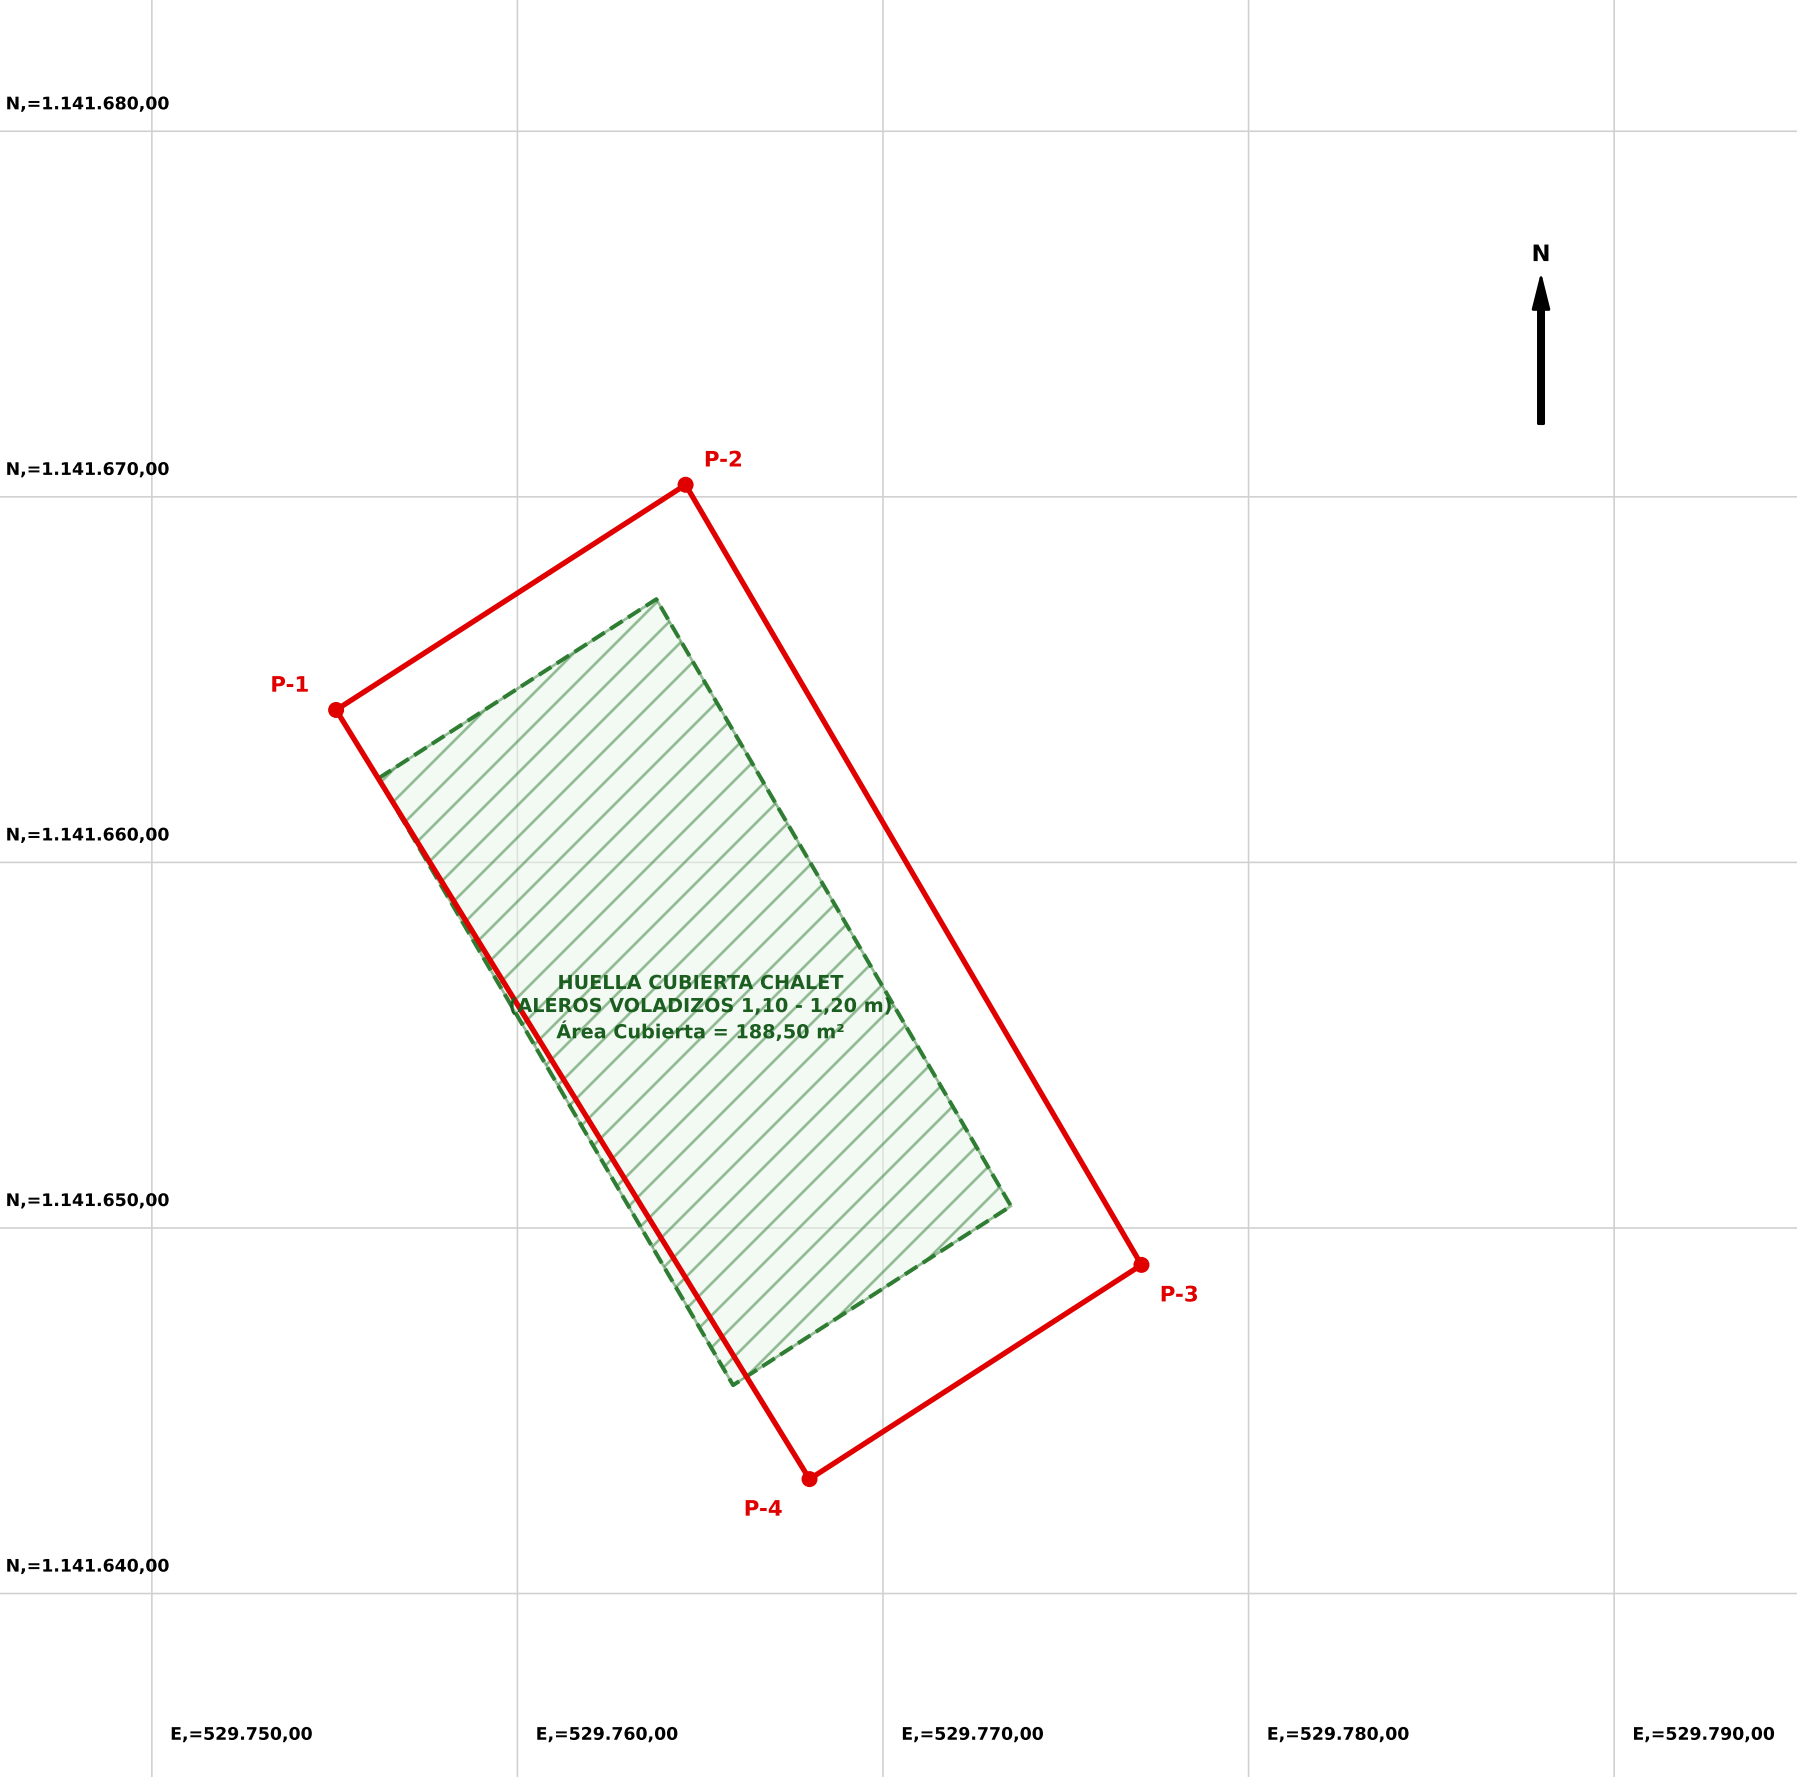

LEVANTAMIENTO TOPOGRÁFICO Y POLIGONAL DE LINDEROS
COORDENADAS U.T.M. (REGVEN / WGS84) Y CUADRO DE ÁREAS DEL CHALET.

UBICACIÓN:	PROPIEDAD:	ESPECIALISTA ARQ. RÚSTICA / DIGITALIZO:	REVISADO:	FECHA:	ESCALA:
AVENIDA 4 ENTRE CALLES 30 Y 31 30-7 MUNICIPIO INDEPENDENCIA ESTADO YARACUY.	ALVARO ARGELIO DIAZ FLOREZ. C.I.: 24.633.787	ARQ. ESPECIALISTA CHALET & TIMBER FRAME T.S.U. ANGEL CAMACARO M. (CVPT 1260)	APROBADO PARA EJECUCIÓN	OCT 2026	1:200