

REPÚBLICA BOLIVARIANA DE VENEZUELA
MUNICIPIO INDEPENDENCIA YARACUY

PROYECTO VILLA MEDITERRÁNEA (ARQUITECTURA VERNÁCULA IBÉRICA & CICLÁDICA)

DISEÑO PARAMÉTRICO OPENCAD / OPENSCAD

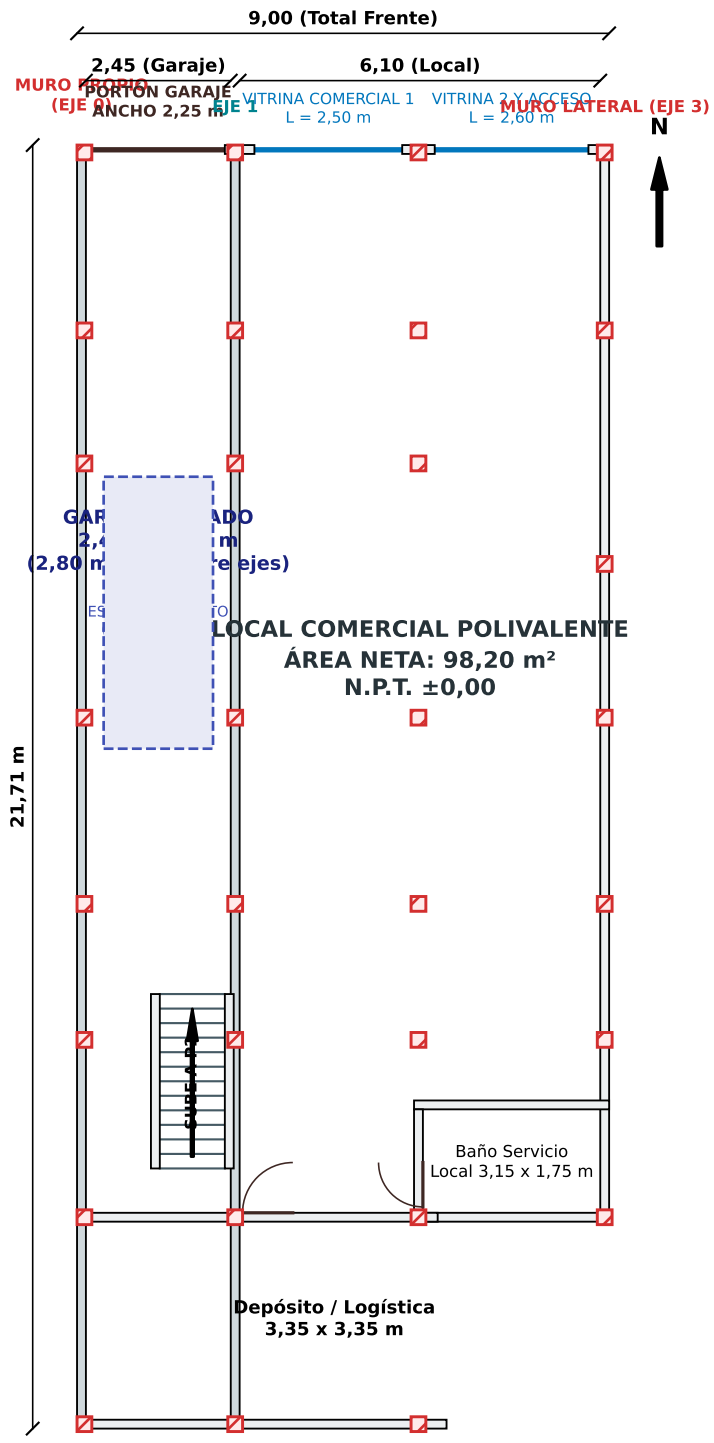

PLANTA BAJA - ZONA COMERCIAL (98 m²) Y GARAJE TECHADO (2,80 m LIBRES)

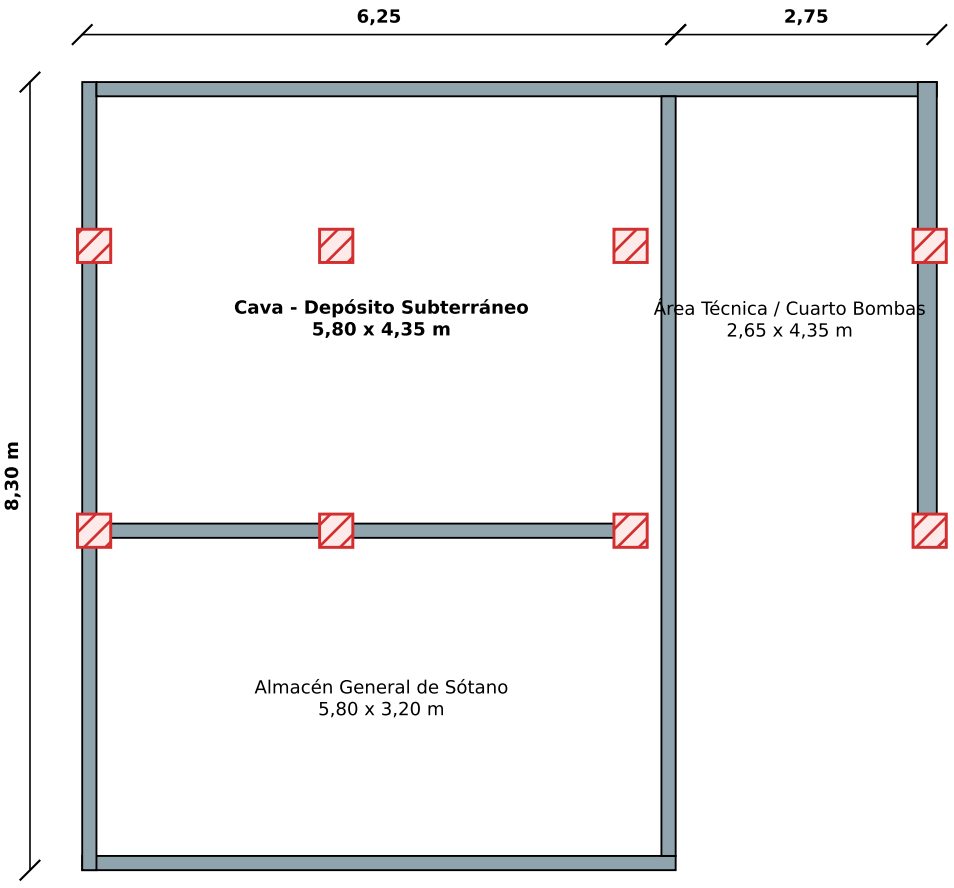


PLANTA SÓTANO (Z = -2,55 m) - FUNDACIÓN Y ESTRUCTURA DE RETENCIÓN

PLANO PLANTA ARQUITECTÓNICA DISTRIBUCIÓN

PLANTA BAJA (ZONA COMERCIAL Y GARAJE AMPLIADO 2,80 m) Y SÓTANO.

UBICACIÓN:	PROPIEDAD:	ESPECIALISTA ARQ. MEDITERRÁNEA / CAD:	REVISADO:	FECHA:	ESCALA:
AVENIDA 4 ENTRE CALLES 30 Y 31 30-7 MUNICIPIO INDEPENDENCIA ESTADO YARACUY.	ALVARO ARGELIO DIAZ FLOREZ. C.I.: 24.633.787	ARQ. ESPECIALISTA EN ESTILO MEDITERRÁNEO T.S.U. ANGEL CAMACARO M. (CVPT 1260)	APROBADO PARA EJECUCIÓN	OCT 2026	1:75

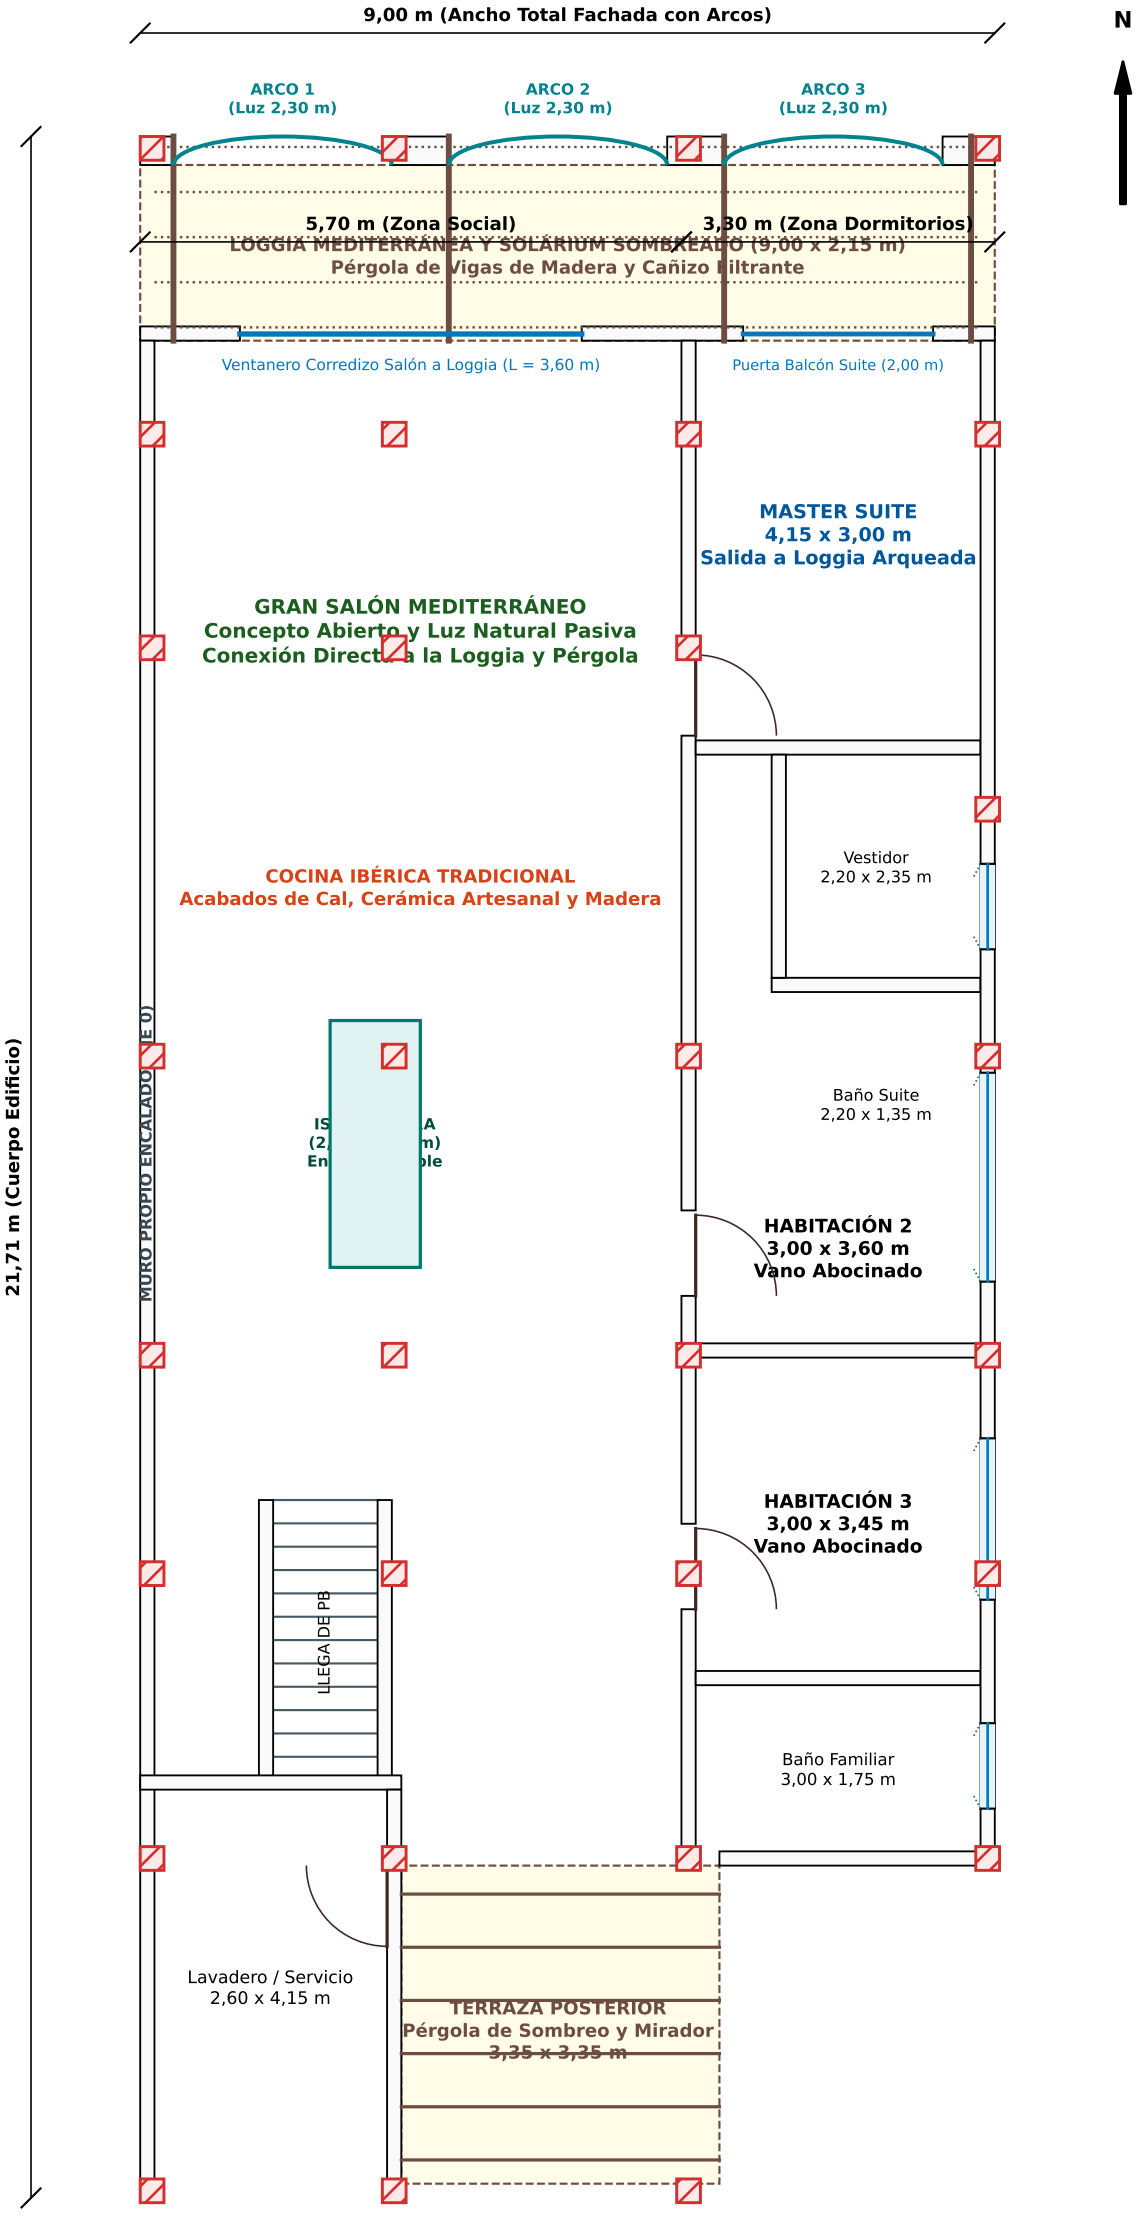

PLANTA ALTA - RESIDENCIA VILLA MEDITERRÁNEA CON LOGGIA DE ARCOS Y PÉRGOLAS DE SOMBRA

PLANO PLANTA ARQUITECTÓNICA DISTRIBUCIÓN - PLANTA ALTA


VILLA MEDITERRÁNEA (LOGGIA CON 3 ARCOS, PÉRGOLAS, SALÓN DIÁFANO Y SUITES).

UBICACIÓN:	PROPIEDAD:	ESPECIALISTA ARQ. MEDITERRÁNEA / CAD:	REVISADO:	FECHA:	ESCALA:
AVENIDA 4 ENTRE CALLES 30 Y 31 30-7 MUNICIPIO INDEPENDENCIA ESTADO YARACUY.	ALVARO ARGELIO DIAZ FLOREZ. C.I.: 24.633.787	ARQ. ESPECIALISTA EN ESTILO MEDITERRÁNEO T.S.U. ANGEL CAMACARO M. (CVPT 1260)	APROBADO PARA EJECUCIÓN	OCT 2026	1:75

REPÚBLICA BOLIVARIANA DE VENEZUELA
MUNICIPIO INDEPENDENCIA YARACUY

PROYECTO VILLA MEDITERRÁNEA (ARQUITECTURA VERNÁCULA IBÉRICA & CICLÁDICA)

DISEÑO PARAMÉTRICO OPENCAD / OPENSCAD

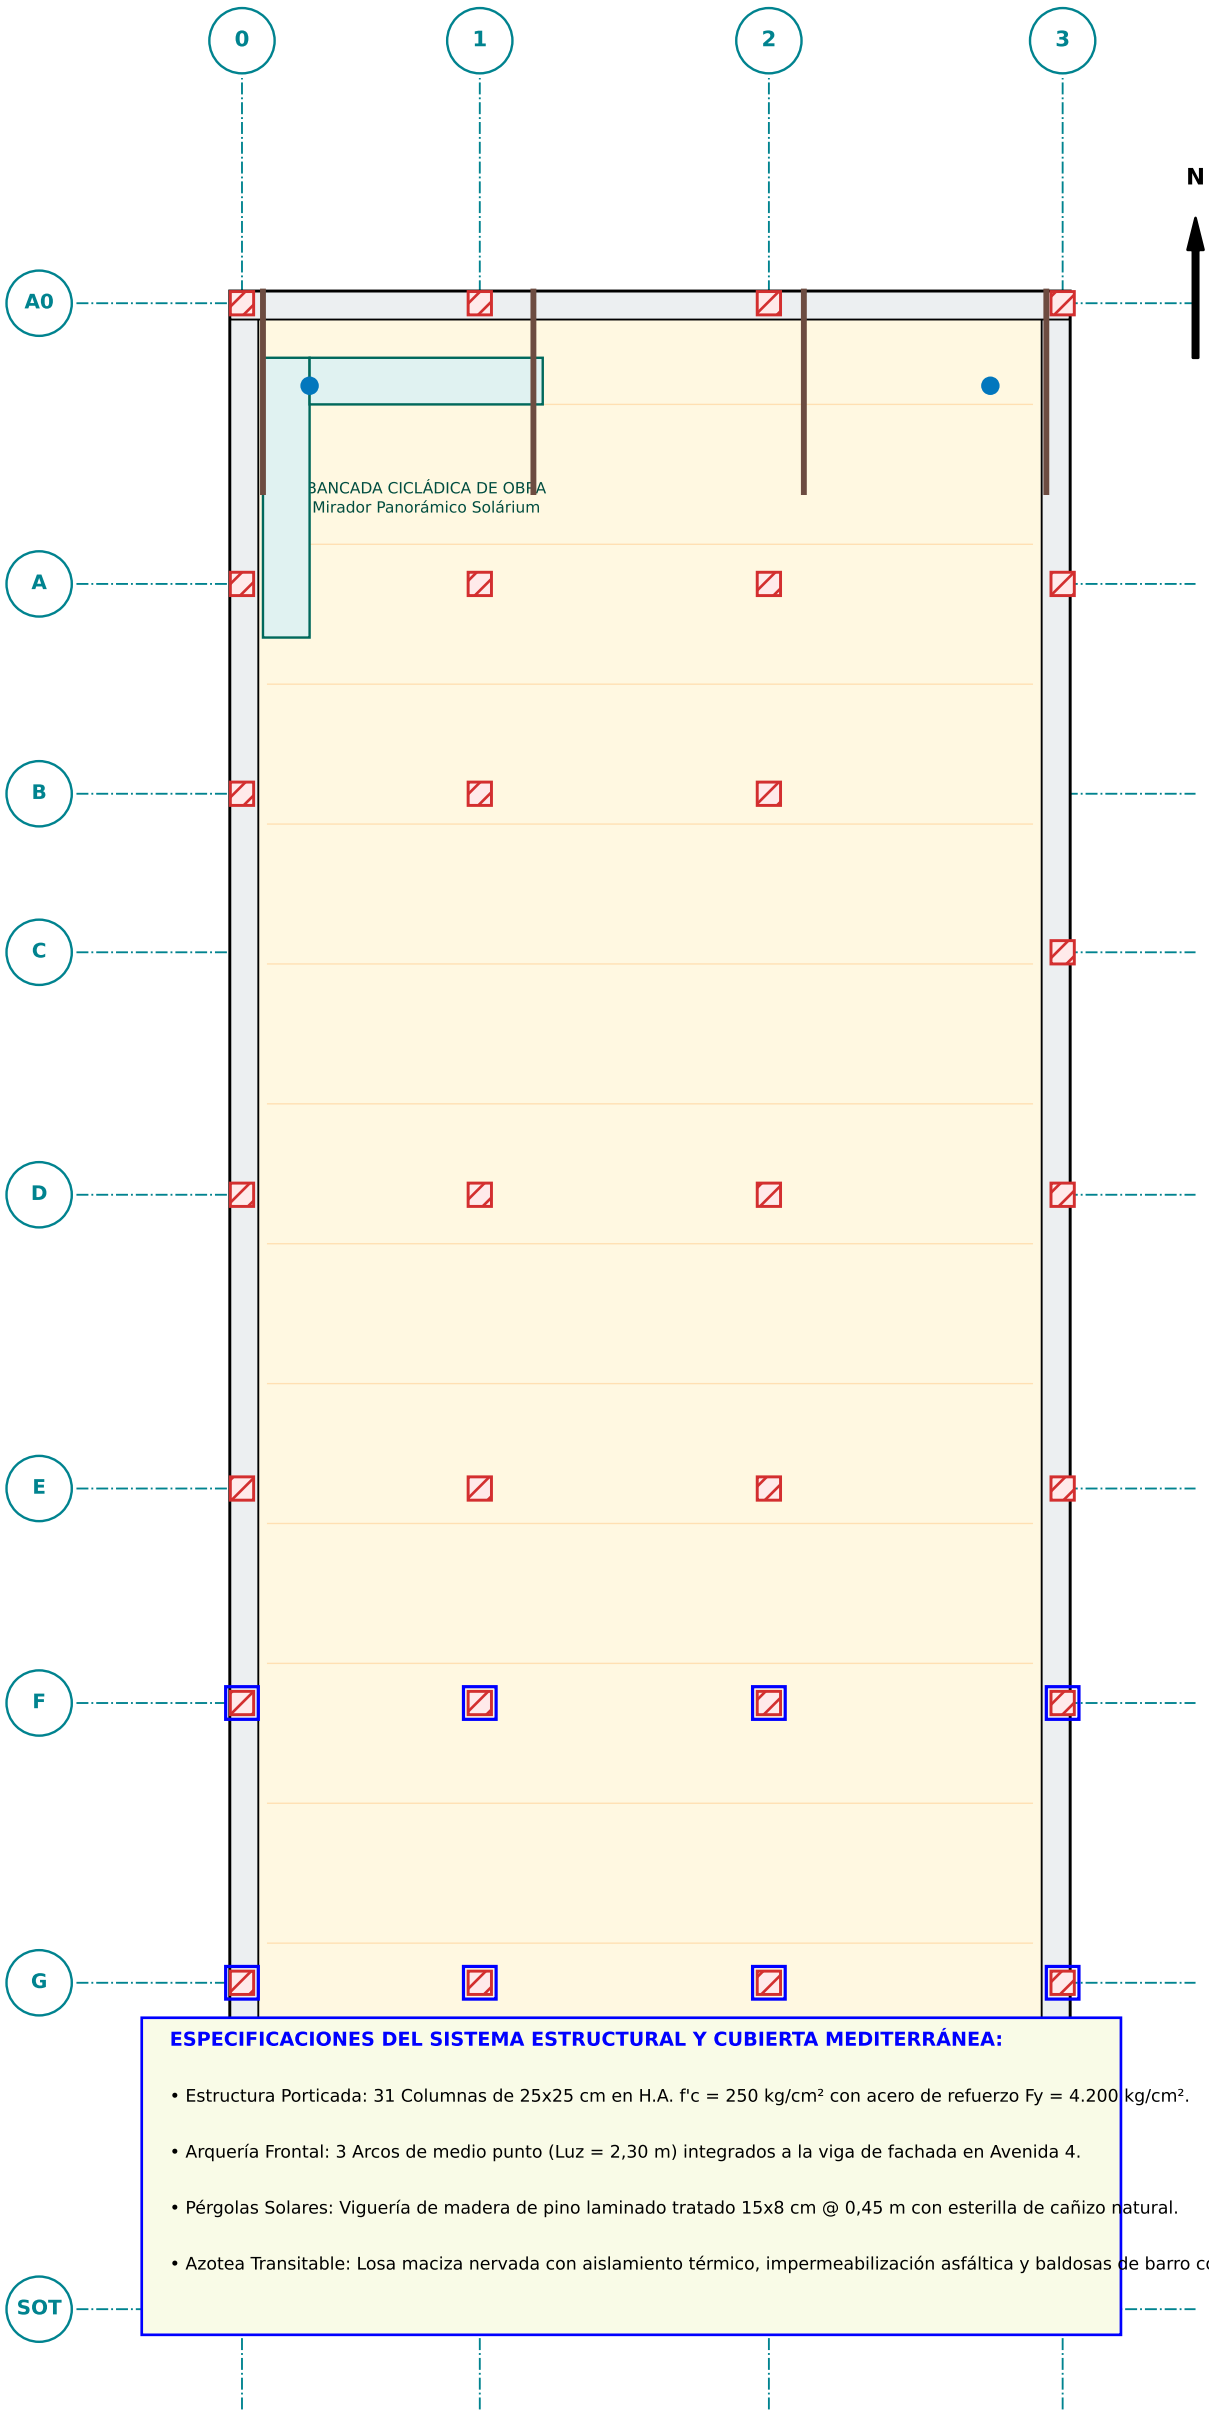

ESPECIFICACIONES DEL SISTEMA ESTRUCTURAL Y CUBIERTA MEDITERRÁNEA:


- Estructura Porticada: 31 Columnas de 25x25 cm en H.A. f'c = 250 kg/cm² con acero de refuerzo Fy = 4.200 kg/cm².
- Arquería Frontal: 3 Arcos de medio punto (Luz = 2,30 m) integrados a la viga de fachada en Avenida 4.
- Pérgolas Solares: Viguería de madera de pino laminado tratado 15x8 cm @ 0,45 m con esterilla de cañizo natural.
- Azotea Transitable: Losa maciza nervada con aislamiento térmico, impermeabilización asfáltica y baldosas de barro cocido.

SISTEMA ESTRUCTURAL: PÓRTICOS DE H.A. (31 COLUMNAS 25x25) + CUBIERTA PLANA TRANSITABLE A LA CATALANA


PLANO ESTRUCTURAL Y AZOTEA SOLÁRIUM TRANSITABLE

RETÍCULA MODULAR DE 31 COLUMNAS, PÉRGOLAS Y CUBIERTA PLANA CON ANTEPECHO.


UBICACIÓN:	PROPIEDAD:	ESPECIALISTA ARQ. MEDITERRÁNEA / CAD:	REVISADO:	FECHA:	ESCALA:
AVENIDA 4 ENTRE CALLES 30 Y 31 30-7 MUNICIPIO INDEPENDENCIA ESTADO YARACUY.	ALVARO ARGELIO DIAZ FLOREZ. C.I.: 24.633.787	ARQ. ESPECIALISTA EN ESTILO MEDITERRÁNEO T.S.U. ANGEL CAMACARO M. (CVPT 1260)	APROBADO PARA EJECUCIÓN	OCT 2026	1:75

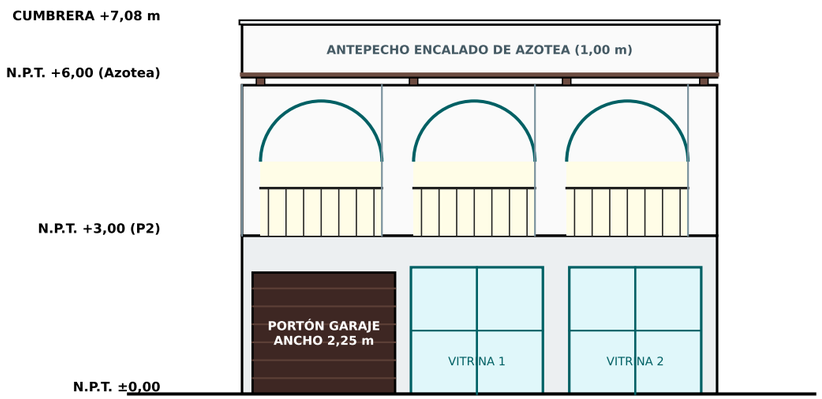

FACHADA PRINCIPAL (AVENIDA 4) - VILLA MEDITERRÁNEA CON ARQUERÍA

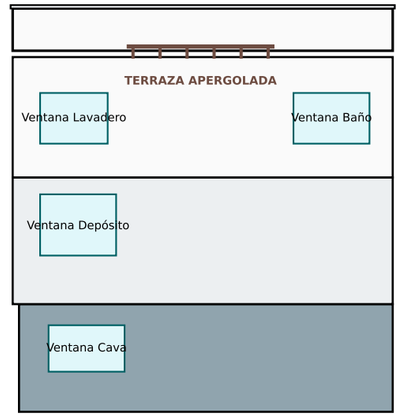

FACHADA POSTERIOR (SÓTANO - PB - P2 TERRAZA APERGOLADA)

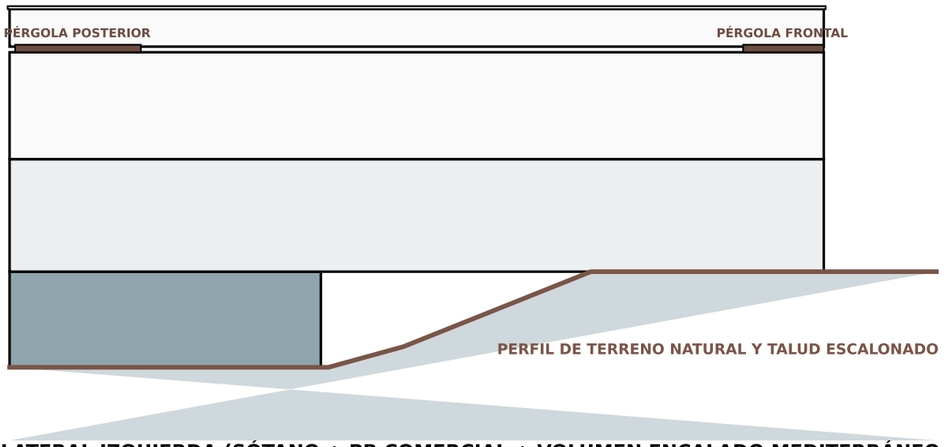

FACHADA LATERAL IZQUIERDA (SÓTANO + PB COMERCIAL + VOLUMEN ENCALADO MEDITERRÁNEO + AZOTEA)

PLANO FACHADAS Y ELEVACIONES MEDITERRÁNEAS
FACHADA PRINCIPAL (AV. 4 CON 3 ARCOS DE MEDIO PUNTO) — LATERAL CON TALUD — POSTERIOR.

UBICACIÓN:	PROPIEDAD:	ESPECIALISTA ARQ. MEDITERRANEA / CAD:	REVISADO:	FECHA:	ESCALA:
AVENIDA 4 ENTRE CALLES 30 Y 31 30-7 MUNICIPIO INDEPENDENCIA ESTADO YARACUY.	ALVARO ARGELIO DIAZ FLOREZ. C.I.: 24.633.787	ARQ. ESPECIALISTA EN ESTILO MEDITERRÁNEO T.S.U. ANGEL CAMACARO M. (CVPT 1260)	APROBADO PARA EJECUCIÓN	OCT 2026	1:75

REPÚBLICA BOLIVARIANA DE VENEZUELA
MUNICIPIO INDEPENDENCIA YARACUY

PROYECTO VILLA MEDITERRÁNEA (ARQUITECTURA VERNÁCULA IBÉRICA & CICLÁDICA)


DISEÑO PARAMÉTRICO OPENCAD / OPENSCAD

CUADRO DE COORDENADAS U.T.M. (REGVEN / WGS84)

LADO EST-PV	RUMBO	DISTANCIA	P	NORTE	ESTE
1 - 2	N 57°10'22.40" E	11.37 m	1	1.141.664,17	529.755,04
2 - 3	S 30°17'59.36" E	24.72 m	2	1.141.670,33	529.764,60
3 - 4	S 57°10'22.40" W	10.81 m	3	1.141.648,99	529.777,07
4 - 1	N 31°36'27.01" W	24.70 m	4	1.141.643,13	529.767,99

LINDEROS

LINDERO	COLINDANTE
NORESTE	CASA DE MIGUEL RODRIGUEZ
SURESTE	SOLAR DE MIGUEL RODRIGUEZ
NOROESTE	AVENIDA 4
SUROESTE	CASA DE MARIO GRATEROL

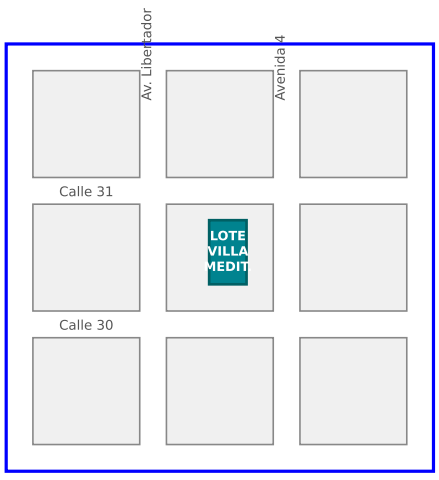


SITUACIÓN RELATIVA S/ESC.

ÁREA DE TERRENO: 273,81 m²

ÁREA DE CONSTRUCCIÓN TOTAL: 372,50 m²

- Planta Baja (Zona Comercial y Garaje 2,80 m): 149,85 m²
- Planta Alta (Villa Mediterránea): 142,20 m² | Sótano: 80,45 m²

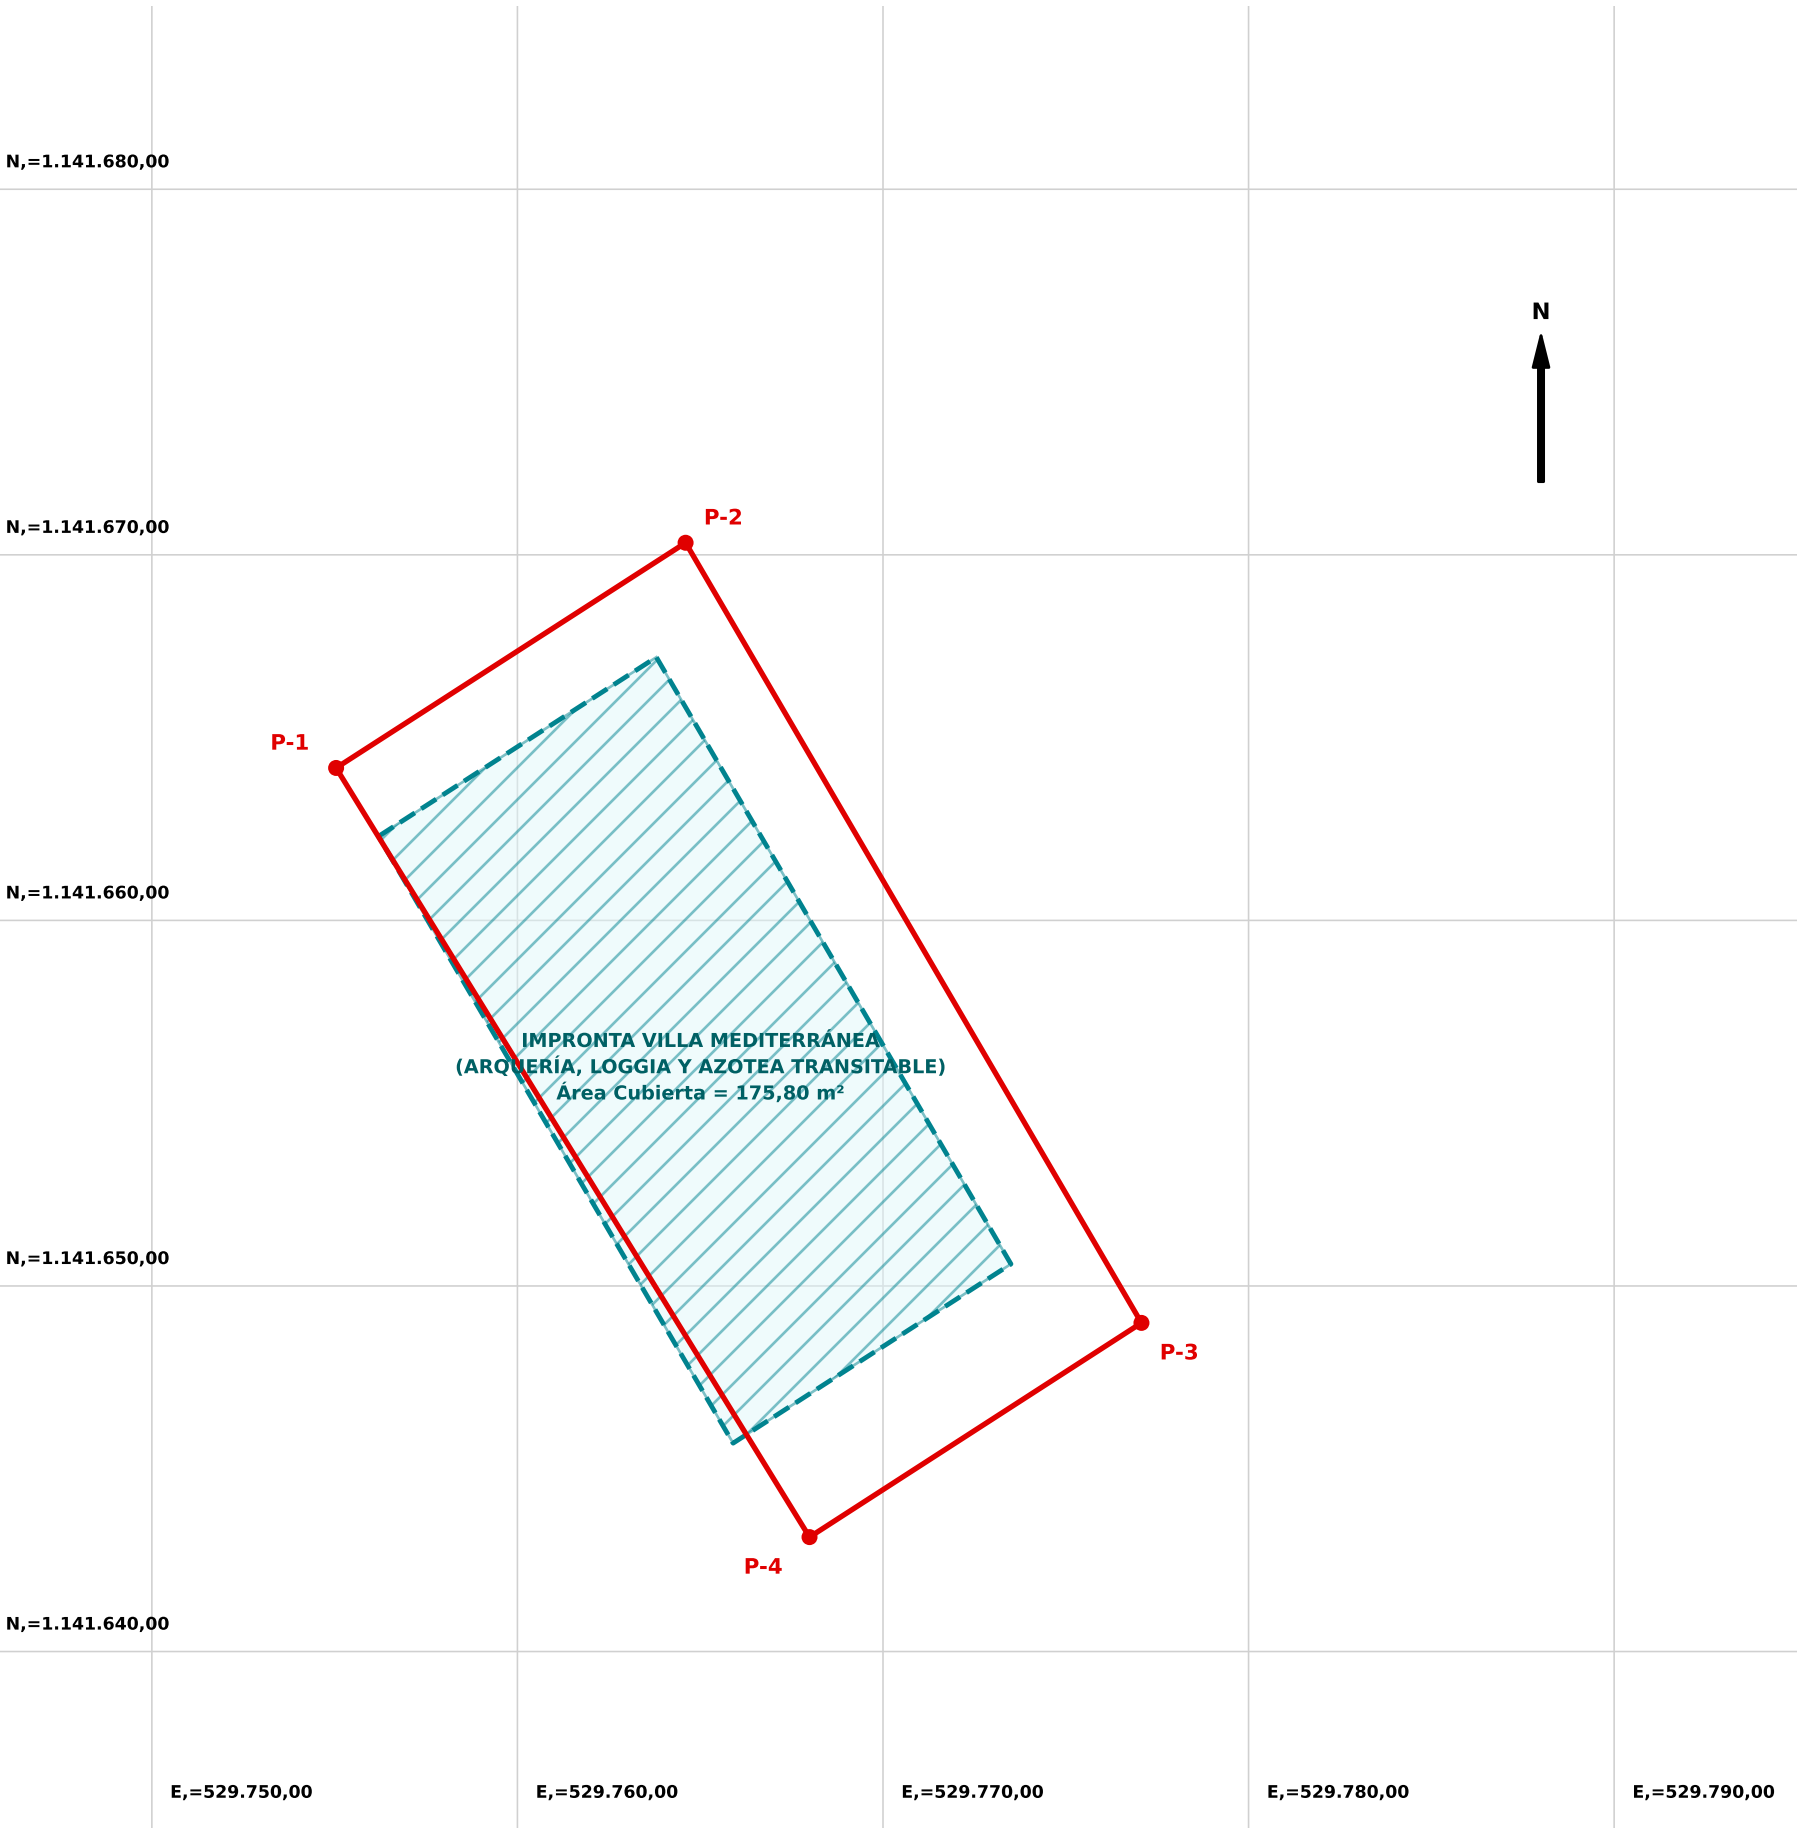

LEVANTAMIENTO TOPOGRÁFICO Y POLIGONAL DE LINDEROS
COORDENADAS U.T.M. (REGVEN / WGS84) Y CUADRO DE ÁREAS VILLA MEDITERRÁNEA.

UBICACIÓN:	PROPIEDAD:	ESPECIALISTA ARQ. MEDITERRÁNEA / CAD:	REVISADO:	FECHA:	ESCALA:
AVENIDA 4 ENTRE CALLES 30 Y 31 30-7 MUNICIPIO INDEPENDENCIA ESTADO YARACUY.	ALVARO ARGELIO DIAZ FLOREZ. C.I.: 24.633.787	ARQ. ESPECIALISTA EN ESTILO MEDITERRÁNEO. T.S.U. ANGEL CAMACARO M. (CVPT 1260)	APROBADO PARA EJECUCIÓN	OCT 2026	1:200