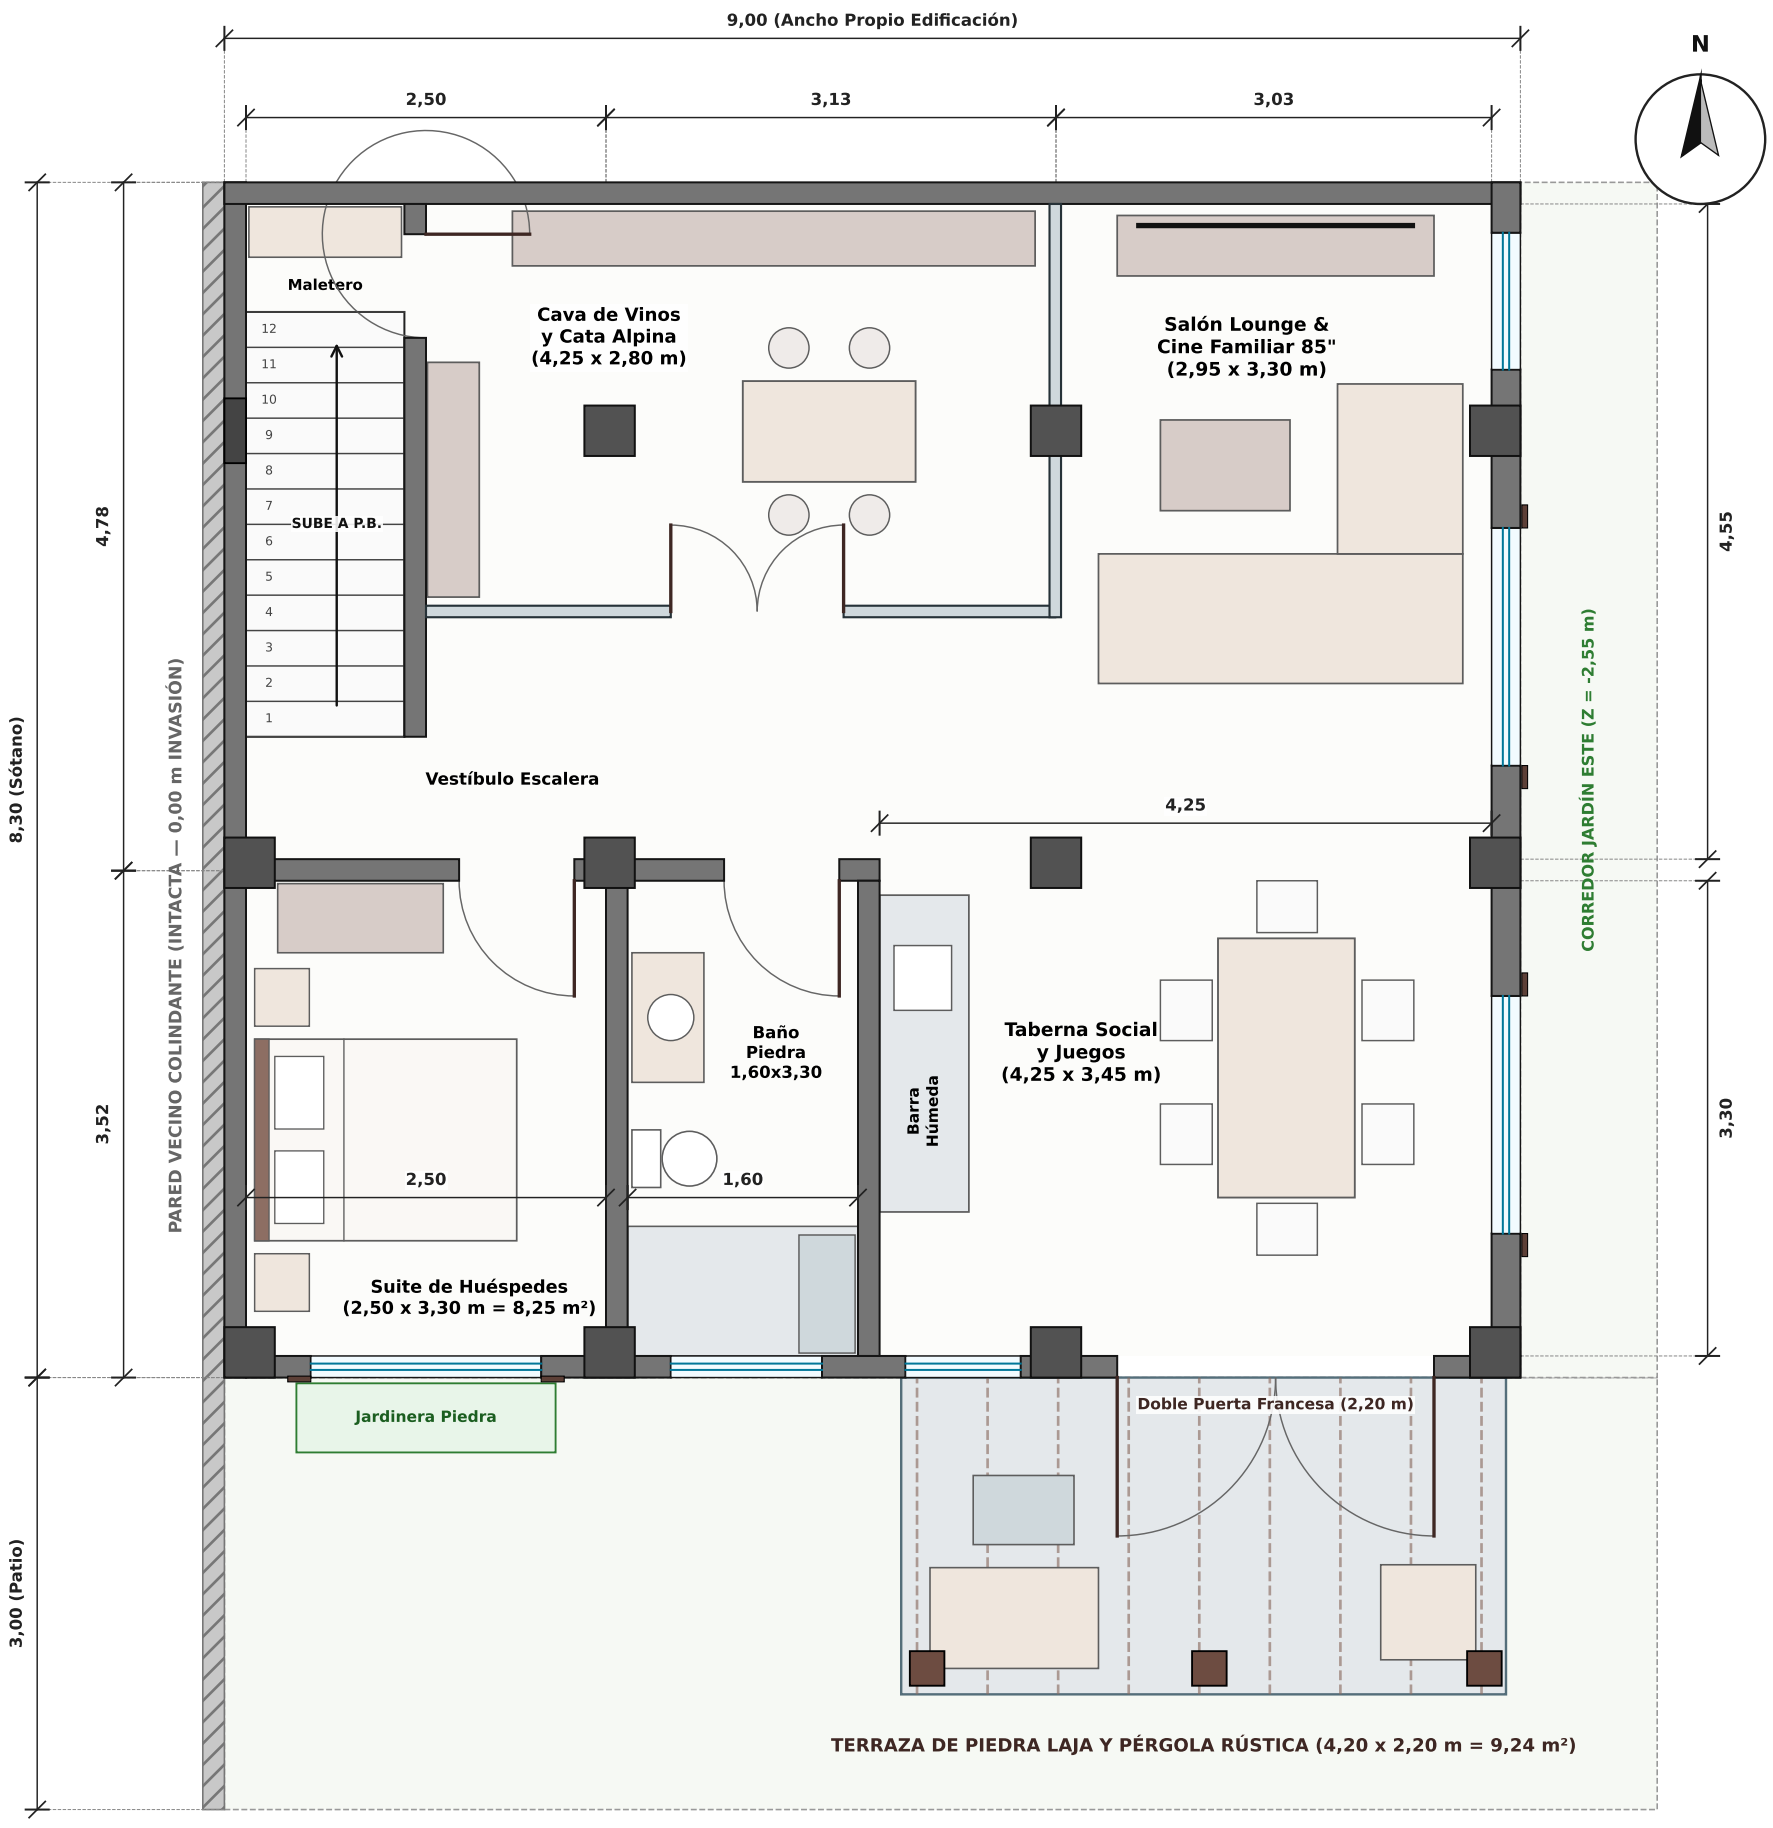


PLANTA SÓTANO CHALET Y PATIO TRASERO (COTA N.P.T. = -2,55 m)

PROGRAMA ARQUITECTÓNICO DEL NIVEL SÓTANO (OPCIÓN A — CHALET ALPINO):

- Huella Construida Sótano: 9,00 x 8,30 m = 74,70 m² | Terraza Exterior Techada con Pérgola: 4,20 x 2,20 m = 9,24 m².
- Zona Social Integrada: Cava de Vinos Climatizada en Hierro/Vidrio (11,9 m²) + Salón Lounge & Cine 85" + Taberna de Juegos y Barra Húmeda.
- Zona Privada Independiente: Suite de Huéspedes con vista al jardín (8,25 m²) + Baño Completo Rústico en Piedra Pizarra (5,28 m²) + Maletero.
- Relación con el Terreno: Nivel -2,55 m abierto a ras con el Patio Posterior mediante Doble Puerta Francesa de 2,20 m; muro oeste 100% propio (X >= 0,15 m).


PLANO PLANTA ARQUITECTÓNICA — NIVEL SÓTANO Y JARDÍN

ARQUITECTURA EN PIEDRA RÚSTICA Y MADERA

DISTRIBUCIÓN: CAVA DE VINOS, SALÓN CINE, TABERNA, SUITE HUÉSPEDES Y PÉRGOLA (Z = -2,55 m).

RESPETO ESTRICTO DE LINDEROS (0,00 m INVASIÓN)

UBICACIÓN:	PROPIEDAD:	LEVANTADO CALCULADO Y DIGITALIZO:	REVISADO:	FECHA:	ESCALA:
AVENIDA 4 ENTRE CALLES 30 Y 31 30-7 MUNICIPIO INDEPENDENCIA ESTADO YARACUY.	ALVARO ARGELIO DIAZ FLOREZ. C.I.: 24.633.787	T.S.U. ANGEL CAMACARO M. CVPT.: N° 1260 SOVIT.: N° 0050	PROYECTO REDISEÑO CHALET ALPINO	OCT 2026	1:50

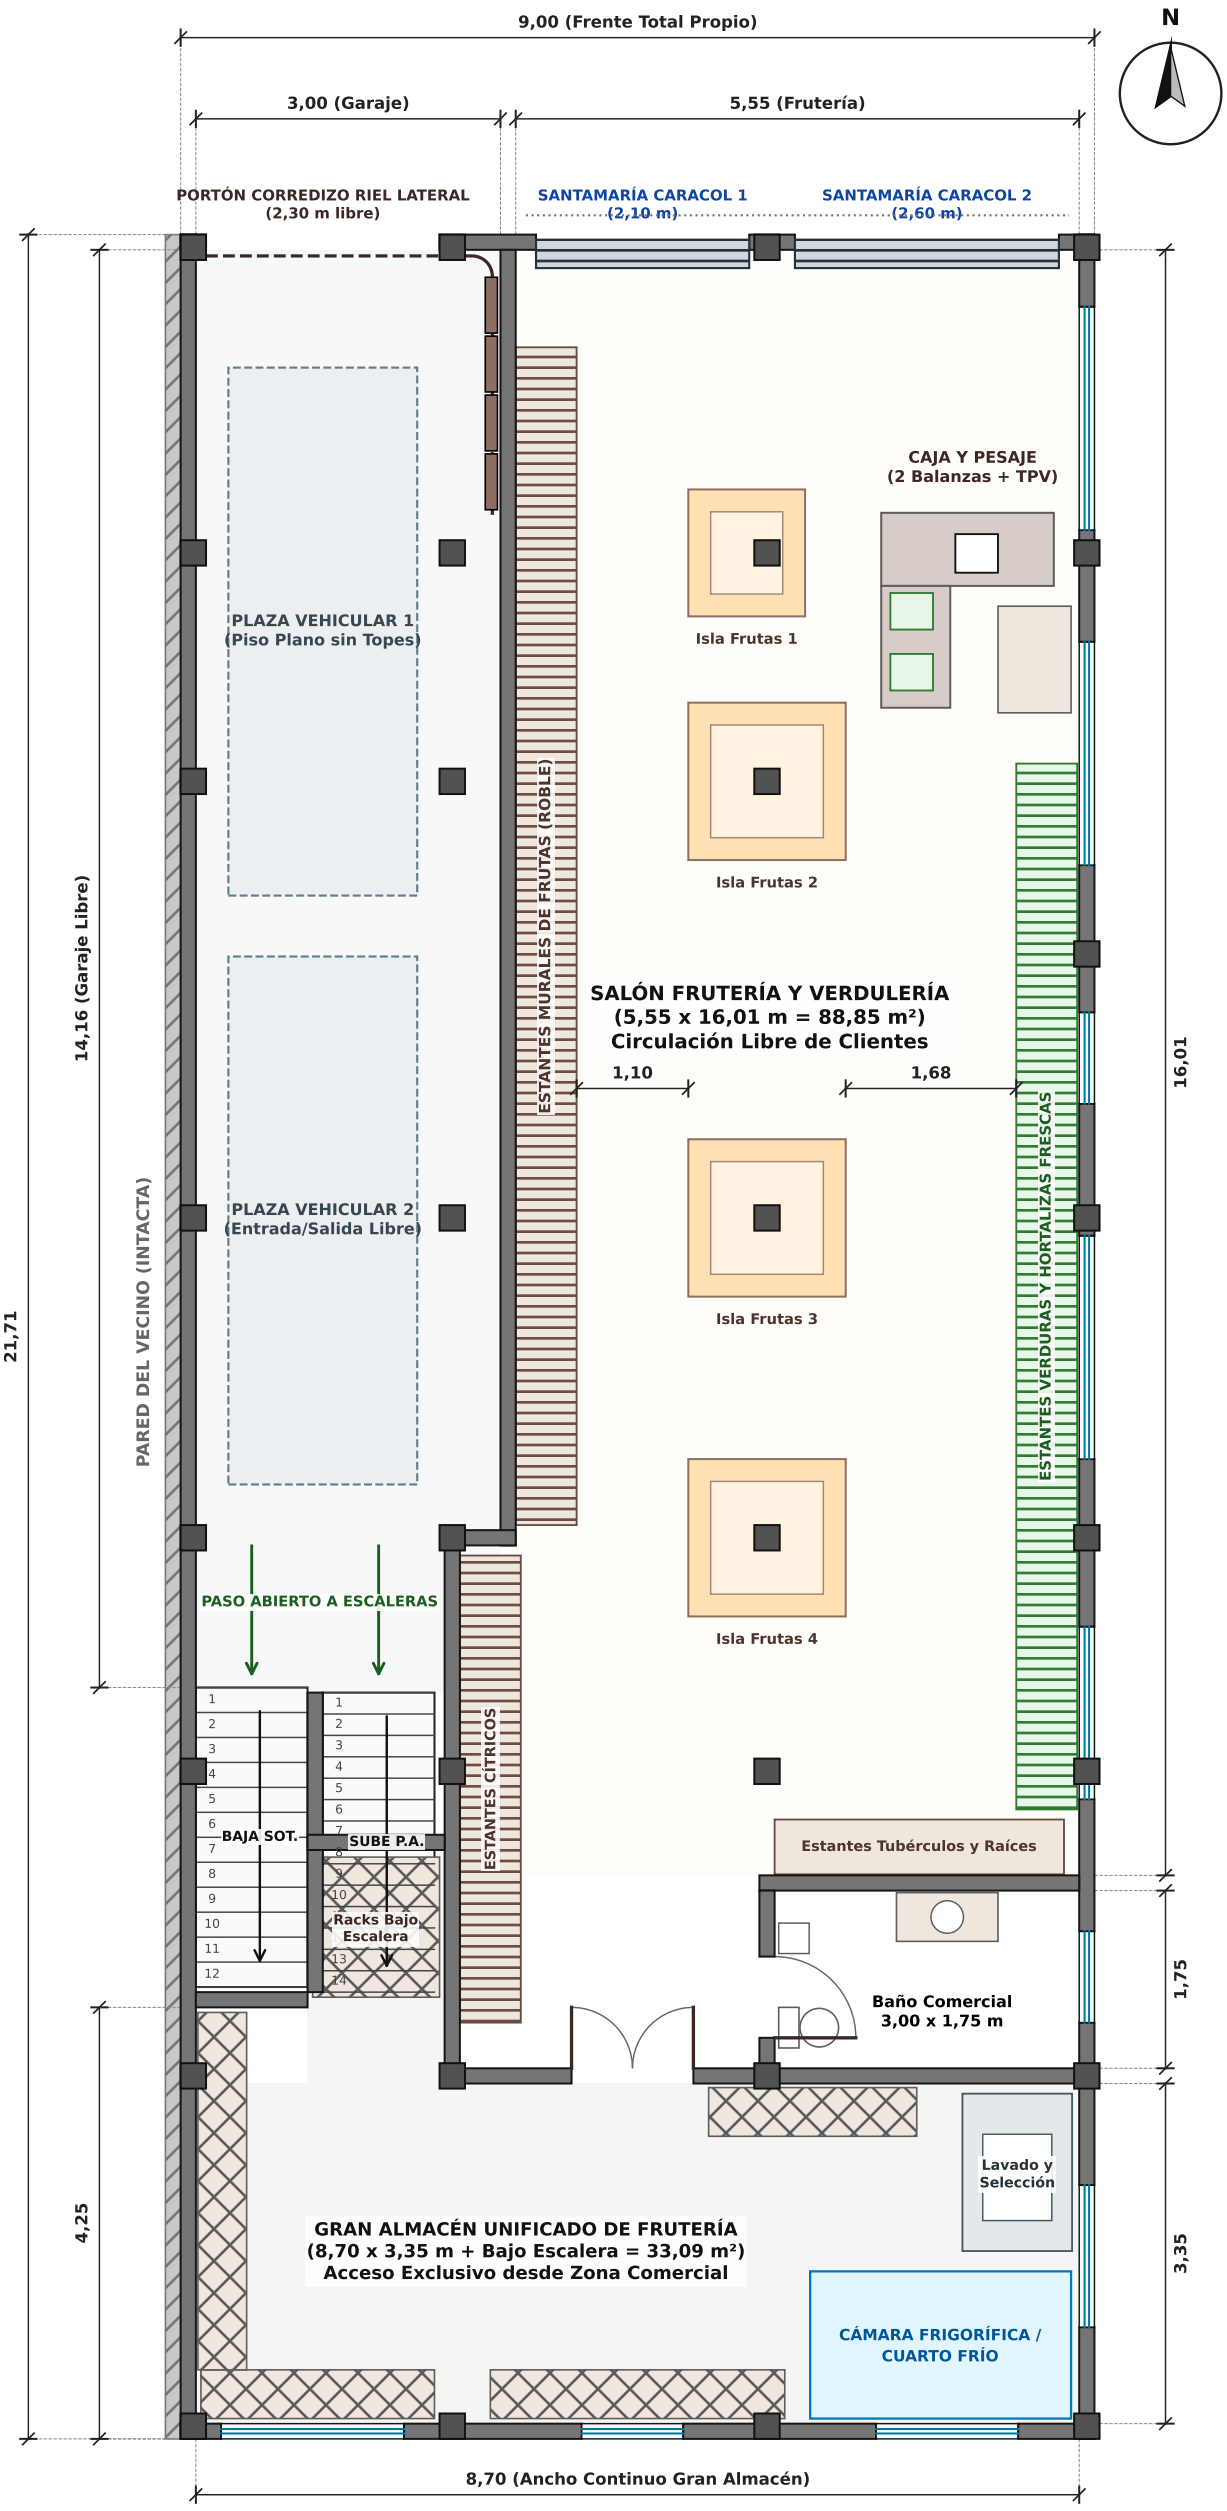

PLANTA BAJA — FRUTERÍA Y ESTACIONAMIENTO (N.P.T. ±0,00 m)

CUADRO DE AMBIENTES
PLANTA BAJA (195,39 m²)

1. SALÓN DE FRUTERÍA — 88,85 m²

- Doble acceso frontal con Santamarías de Caracol enrollables hacia arriba.
- 4 Islas Piramidales de Frutas a 4 caras integradas en las columnas del Eje 2.
- Estanterías inclinadas de roble en muros Oeste, Este y Sur (sin mesas).
- Pasillos amplios de 1,10 m a 1,68 m.

2. CAJA Y PESAJE MEJORADA — Integrada

- Mostrador en 'L' en piedra laja y roble.
- 2 Balanzas electrónicas con visor alto, TPV táctil y área trasera de empaque.

3. GRAN ALMACÉN UNIFICADO — 33,09 m²

- Unión total de Depósito + Área Apoyo + Bajo Escalera + antigua Gerencia.
- Ancho libre de pared a pared: 8,70 m.
- Cero acceso desde el estacionamiento; entrada exclusiva por puerta doble (1,20m).
- Incluye Cuarto Frío, Mesón de Lavado y 4 baterías de racks industriales.

4. BAÑO COMERCIAL RÚSTICO — 5,70 m²

- Lavamanos en piedra, WC y urinario.

5. ESTACIONAMIENTO FLUIDO — 46,20 m²

- Portón corredizo sobre riel lateral a 90° alojado en bolsillo derecho (X=3,16..3,28).
- 3,00 m entre muros y 14,16 m de largo.
- Piso 100% plano SIN topes en fila.
- Acceso directo y abierto a las escaleras de Sótano y Segundo Piso.


PLANO PLANTA ARQUITECTÓNICA — PLANTA BAJA

FRUTERÍA Y VERDULERÍA ALPINO + GRAN ALMACÉN (33,09 m²) + ESTACIONAMIENTO FLUIDO.


ARQUITECTURA EN PIEDRA RÚSTICA Y MADERA

RESPETO ESTRICTO DE LINDEROS (0,00 m INVASIÓN)

UBICACIÓN:	PROPIEDAD:	LEVANTADO CALCULADO Y DIGITALIZO:	REVISADO:	FECHA:	ESCALA:
AVENIDA 4 ENTRE CALLES 30 Y 31 30-7 MUNICIPIO INDEPENDENCIA ESTADO YARACUY.	ALVARO ARGELIO DIAZ FLOREZ. C.I.: 24.633.787	T.S.U. ANGEL CAMACARO M. CVPT.: N° 1260 SOVIT.: N° 0050	PROYECTO REDISEÑO CHALET ALPINO	OCT 2026	1:75

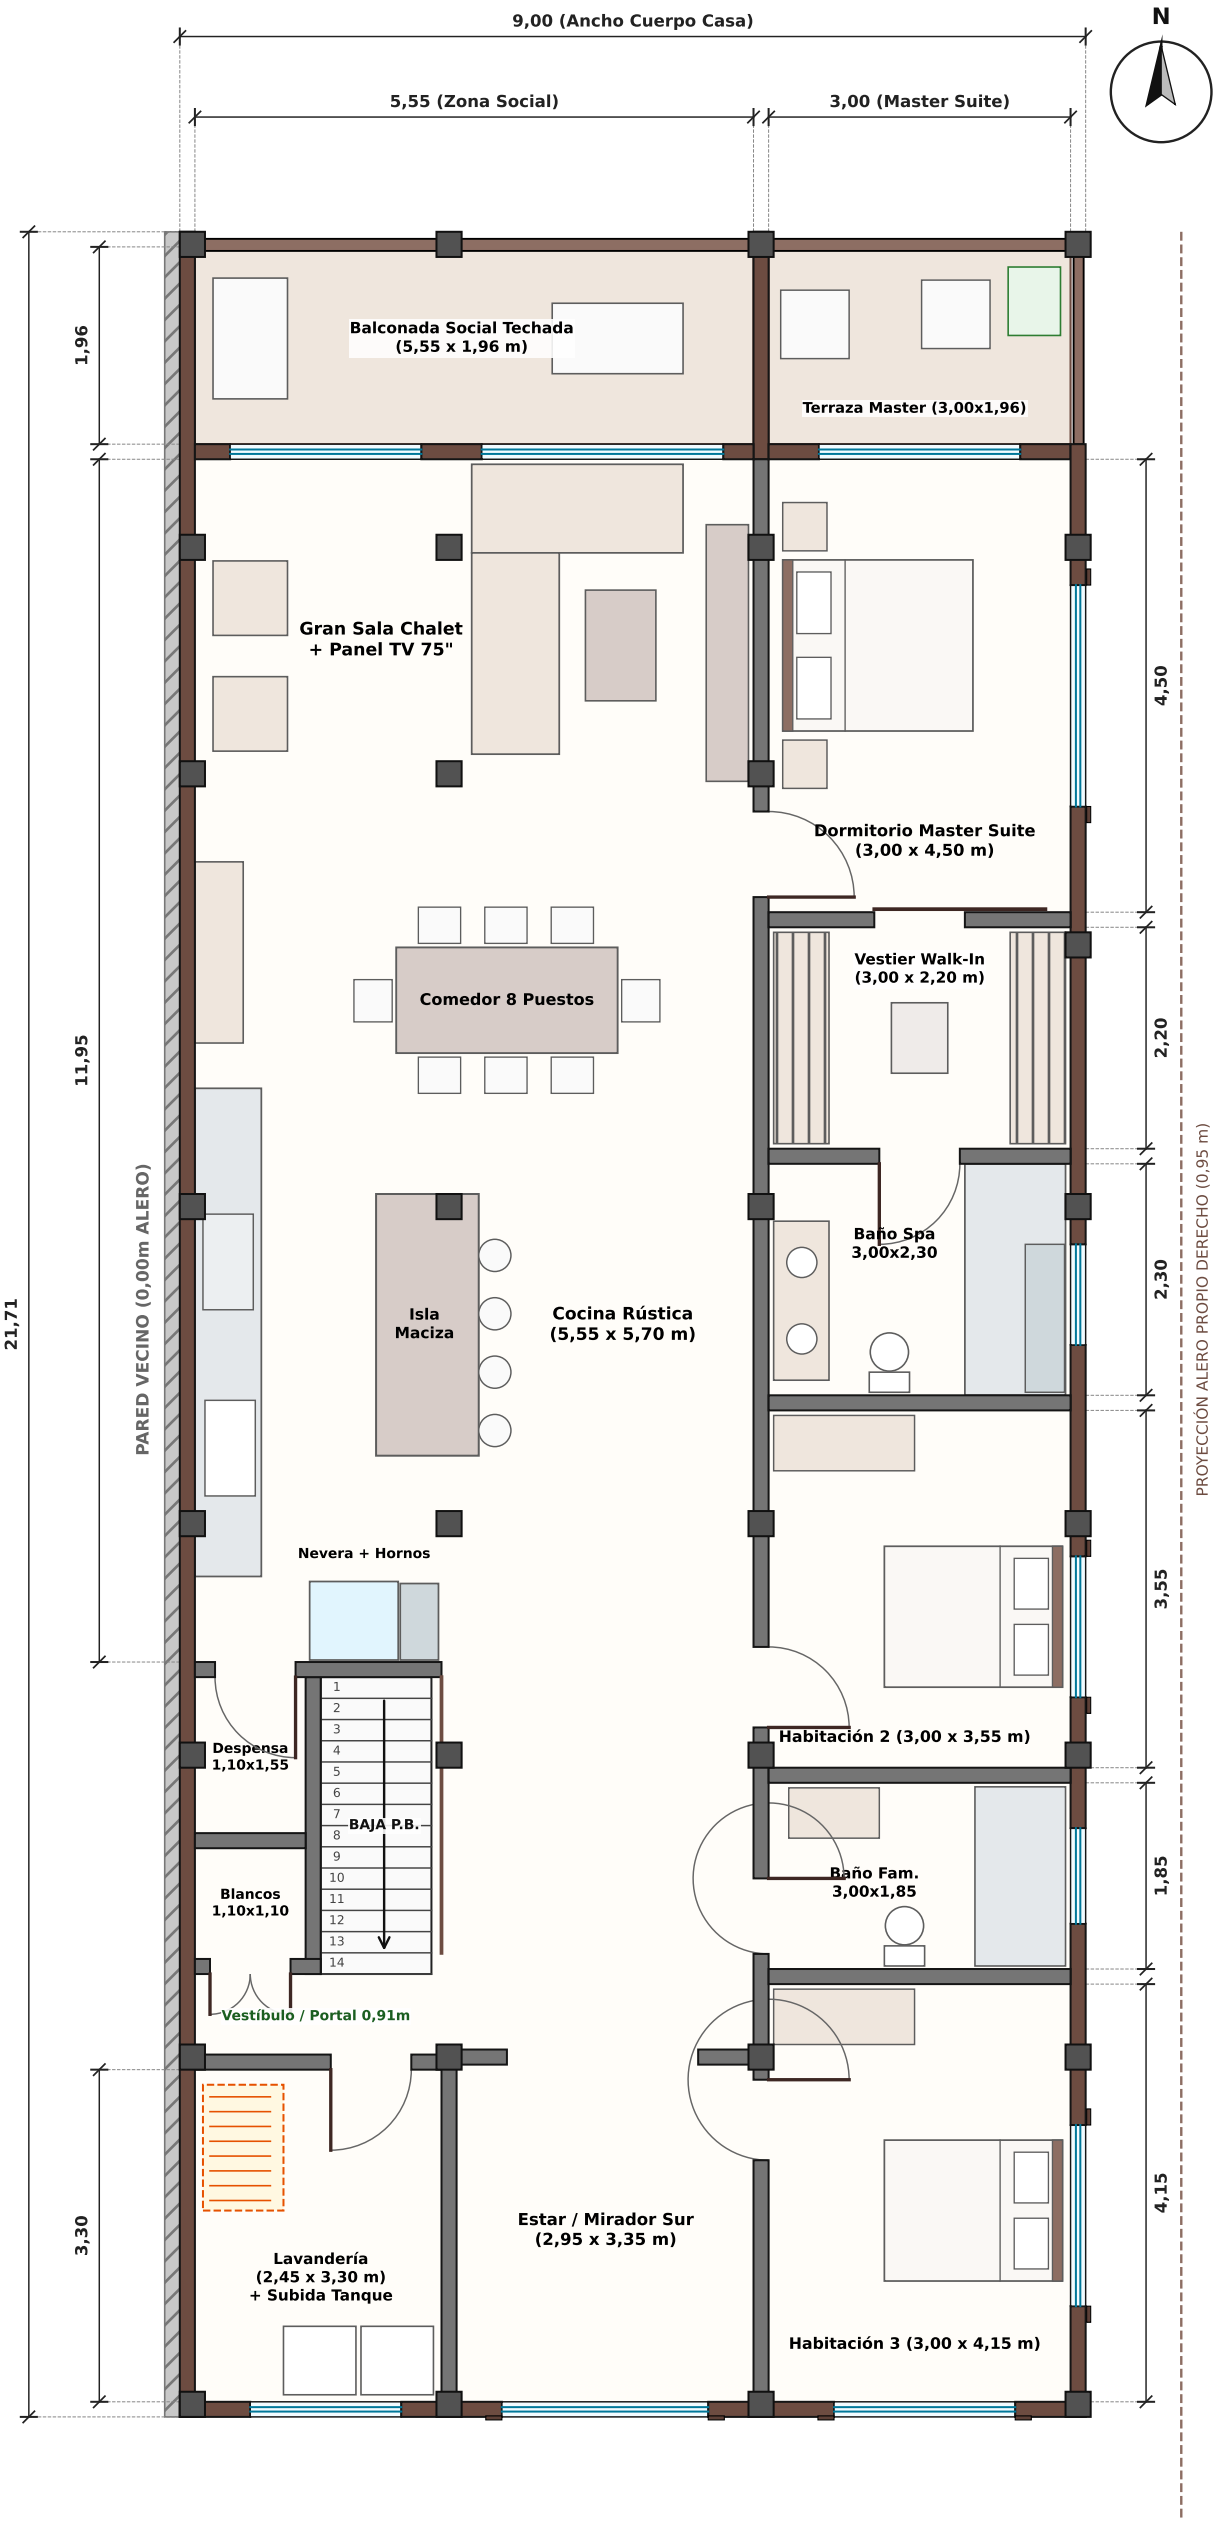

PLANTA SEGUNDO PISO RESIDENCIAL CHALET (N.P.T. +3,00 m)

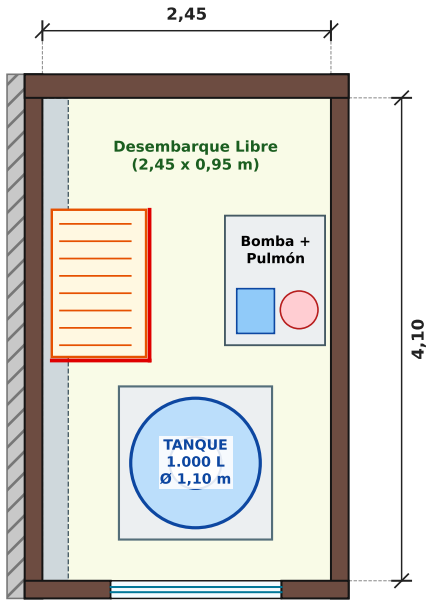

Celosía Abatible 1,45 m

PLANTA BUHARDILLA TANQUE 1.000 L
(N.P.T. +5,68 m — ESC. 1:50)

PROGRAMA RESIDENCIAL SEGUNDO PISO (195,39 m²)

- Doble Terraza Independiente Av. 4: Balconada Social (10,88 m²) + Terraza Privada Master Suite (5,88 m²).
- Master Suite de Gran Formato (32,88 m²): Dormitorio King + Vestier Walk-In doble frente + Baño Spa con ducha pizarra.
- Zona Familiar Posterior: Habitación 2 (10,65 m²), Baño Familiar (5,55 m²), Habitación 3 (12,45 m²) y Estar / Mirador Sur (9,88 m²).
- Área Social Chalet Integrada: Gran Sala TV 75", Comedor 8 puestos, Cocina Rústica con Isla Central, Despensa Walk-In y Clóset de Blancos.
- Lavandería + Buhardilla Hidroneumática: Tanque vertical de 1.000 L a +5,68 m con acceso seguro y 0,00 m invasión.


PLANO PLANTA ARQUITECTÓNICA — SEGUNDO PISO Y TANQUE

RESIDENCIA FAMILIAR CHALET RÚSTICO (Z = +3,00 m) + BUHARDILLA TÉCNICA 1.000 L (Z = +5,68 m).

ARQUITECTURA EN PIEDRA RÚSTICA Y MADERA

RESPETO ESTRICTO DE LINDEROS (0,00 m INVASIÓN)

UBICACIÓN:	PROPIEDAD:	LEVANTADO CALCULADO Y DIGITALIZO:	REVISADO:	FECHA:	ESCALA:
AVENIDA 4 ENTRE CALLES 30 Y 31 30-7 MUNICIPIO INDEPENDENCIA ESTADO YARACUY.	ALVARO ARGELIO DIAZ FLOREZ. C.I.: 24.633.787	T.S.U. ANGEL CAMACARO M. CVPT.: N° 1260 SOVIT.: N° 0050	PROYECTO REDISEÑO CHALET ALPINO	OCT 2026	1:75 / 1:50

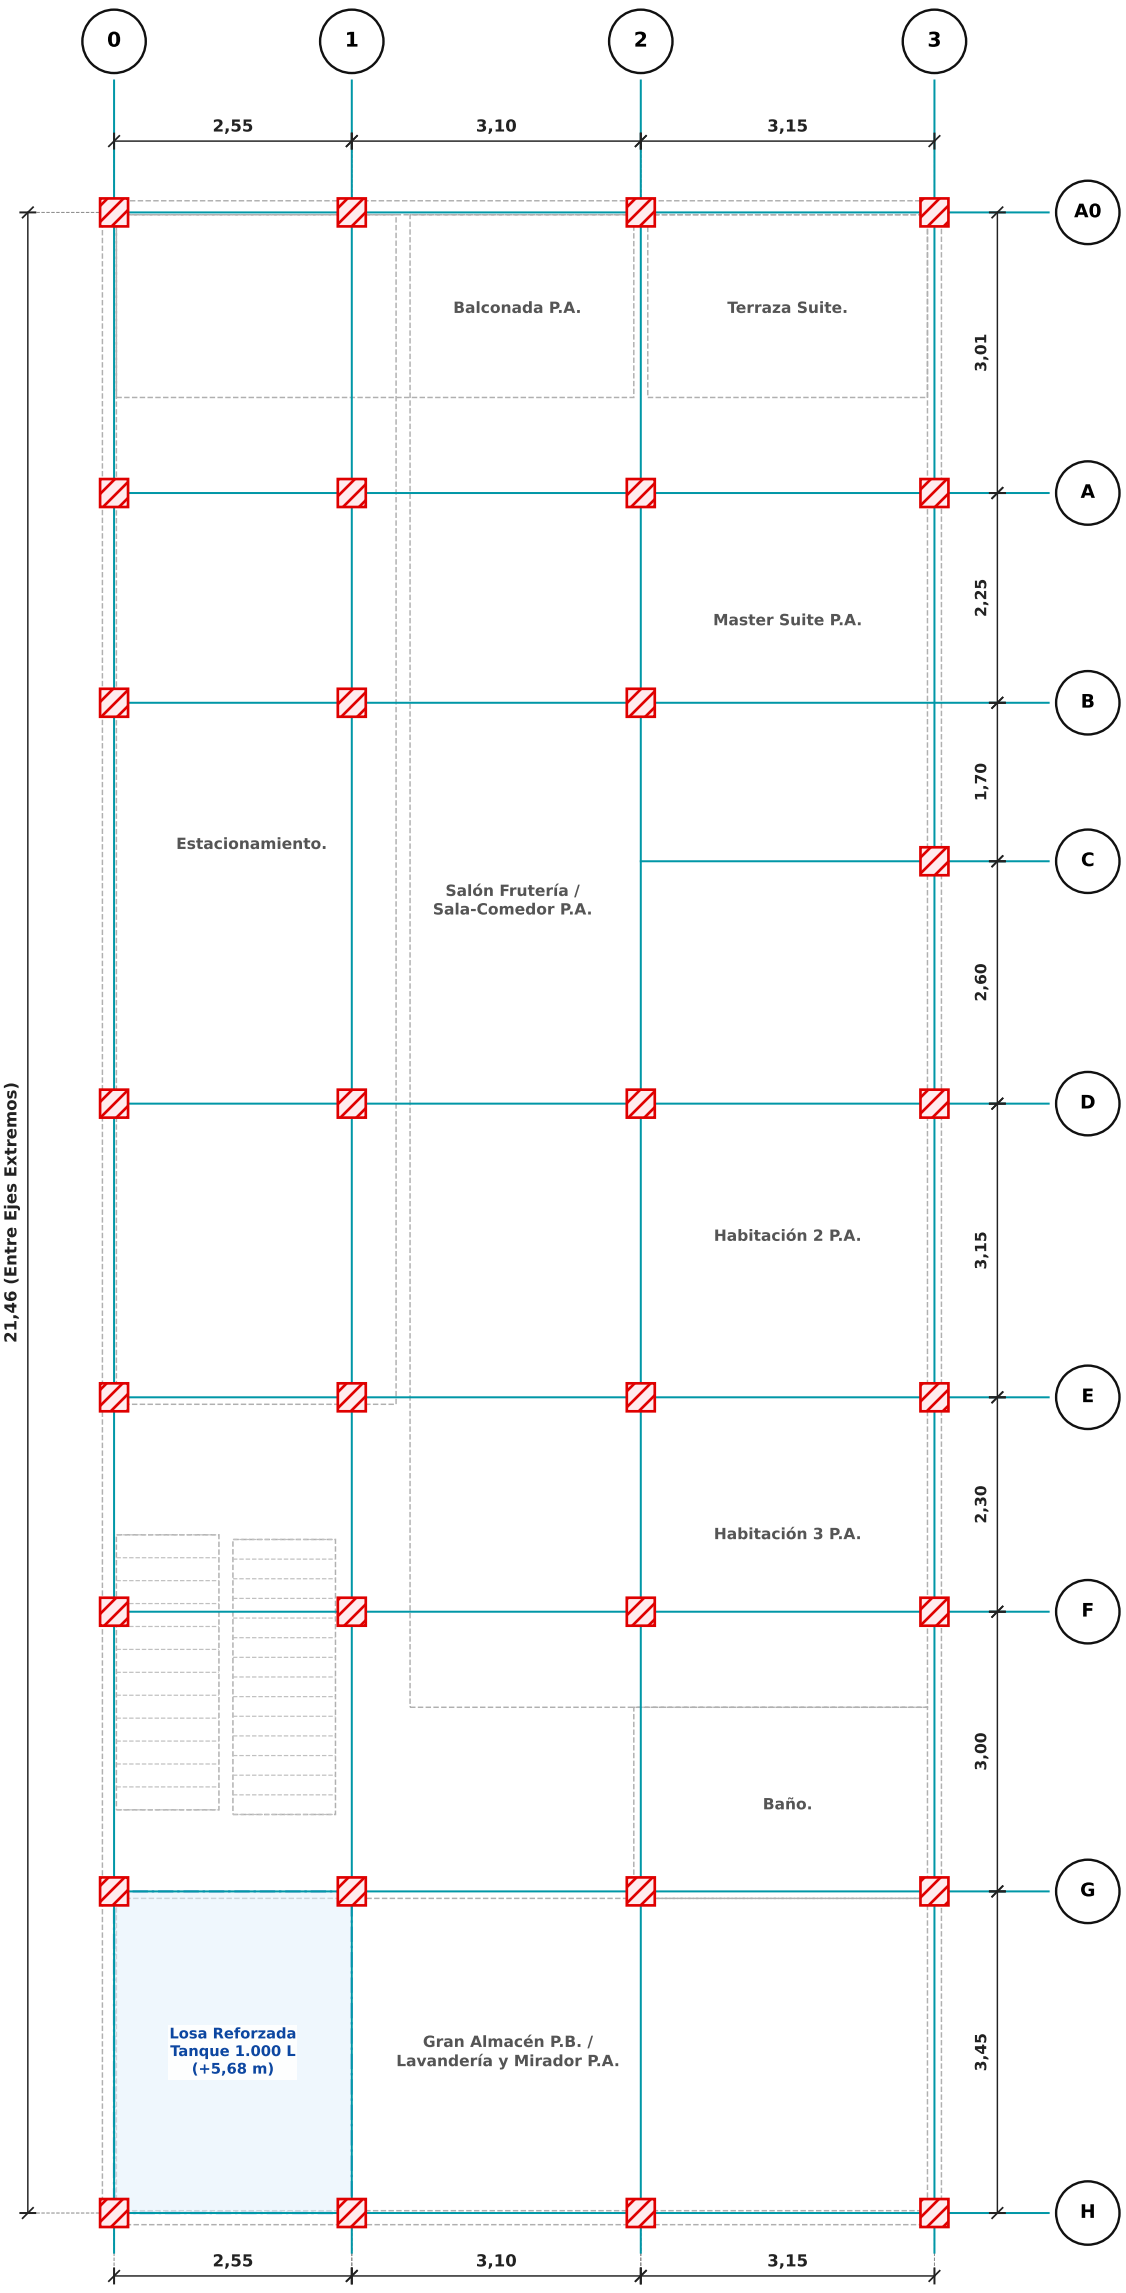

PLANTA CASA — PLANTA BAJA Y SEGUNDO PISO
(32 APOYOS ESTRUCTURALES 25 x 25 cm)

MEMORIA Y ESPECIFICACIONES ESTRUCTURALES

1. INFRAESTRUCTURA Y SÓTANO (-2,55 m):

- 12 columnas de 35 x 35 cm en concreto armado ($f'c$ = 250 kg/cm², 8 Ø 5/8" + estribos Ø 3/8").
- Muro de contención norte y muro propio oeste (X = 0,15..0,30 m) sin tocar pared vecina.

2. PLANTA BAJA COMERCIAL (±0,00 m):


- 32 columnas de 25 x 25 cm en retícula ortogonal intacta (Ejes 0, 1, 2, 3 x A0..H).
- Vigas sísmicas de carga de 25 x 35 cm.

3. ÚLTIMO PISO (+3,00 m) — CONCRETO O IPE:

- Opción A: Continuación en concreto 25 x 25 cm.
- Opción B Recomendada: Columnas metálicas tipo IPE 160 / HEA 140 (Acero ASTM A36) sobre planchas base 250x250x16 mm con 4 pernos Ø 5/8" anclados en los nodos de +3,00 m (menor peso sísmico y acople directo con cubierta Chalet).

4. CUBIERTA CHALET Y TANQUE (+5,68 m):

- Losa maciza reforzada en Ejes 0-1 / G-H para Tanque de 1.000 L + Cerchas Alpinas a 32°.

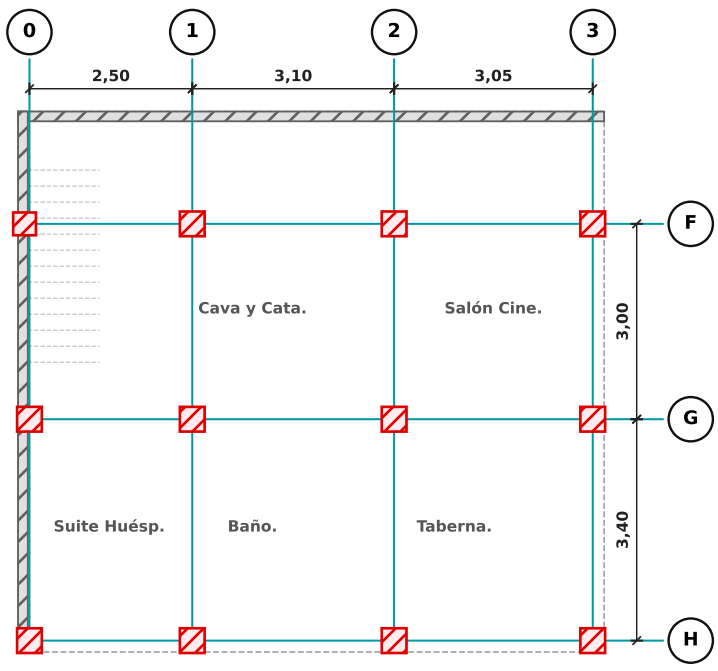

PLANTA SÓTANO (12 APOYOS 35 x 35 cm)

PLANO DISTRIBUCIÓN DE COLUMNAS Y EJES ESTRUCTURALES

PLANTA BAJA Y SEGUNDO PISO: 25 x 25 (cm) / IPE METÁLICO — SÓTANO: 35 x 35 (cm).

ARQUITECTURA EN PIEDRA RÚSTICA Y MADERA


RESPETO ESTRICTO DE LINDEROS (0,00 m INVASIÓN)

UBICACIÓN:	PROPIEDAD:	LEVANTADO CALCULADO Y DIGITALIZO:	REVISADO:	FECHA:	ESCALA:
AVENIDA 4 ENTRE CALLES 30 Y 31 30-7 MUNICIPIO INDEPENDENCIA ESTADO YARACUY.	ALVARO ARGELIO DIAZ FLOREZ. C.I.: 24.633.787	T.S.U. ANGEL CAMACARO M. CVPT.: N° 1260 SOVIT.: N° 0050	PROYECTO REDISEÑO CHALET ALPINO	OCT 2026	1:75


REPÚBLICA BOLIVARIANA DE VENEZUELA
MUNICIPIO INDEPENDENCIA YARACUY

PROYECTO INTEGRAL: CHALET RÚSTICO ALPINO & COMERCIO


ELEVACIONES Y PERFIL TOPOGRÁFICO | LÁMINA 5 / 6

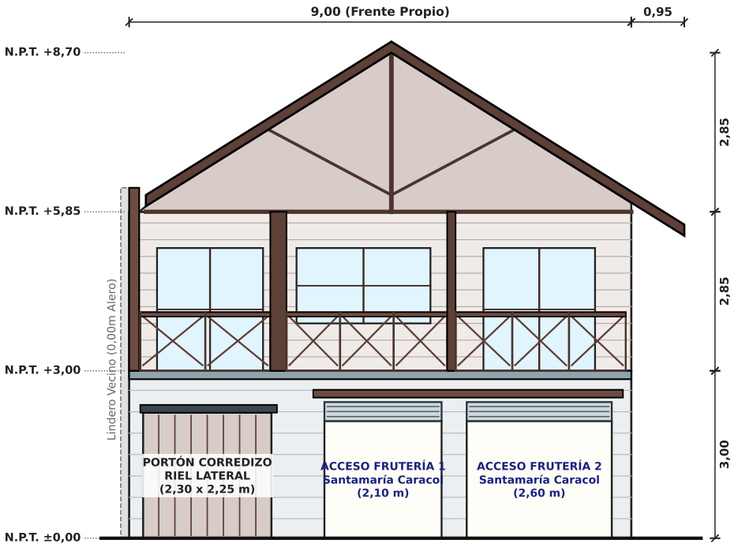

FACHADA PRINCIPAL AVENIDA 4
(PLANTA BAJA COMERCIAL Y SEGUNDO PISO CHALET)

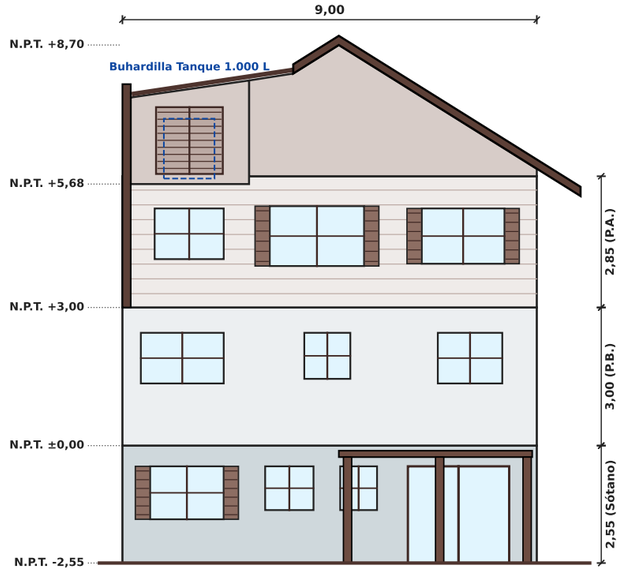

FACHADA POSTERIOR SUR
(PATIO PÉRGOLA, SÓTANO, GRAN ALMACÉN, P.A. Y BUHARDILLA TANQUE)

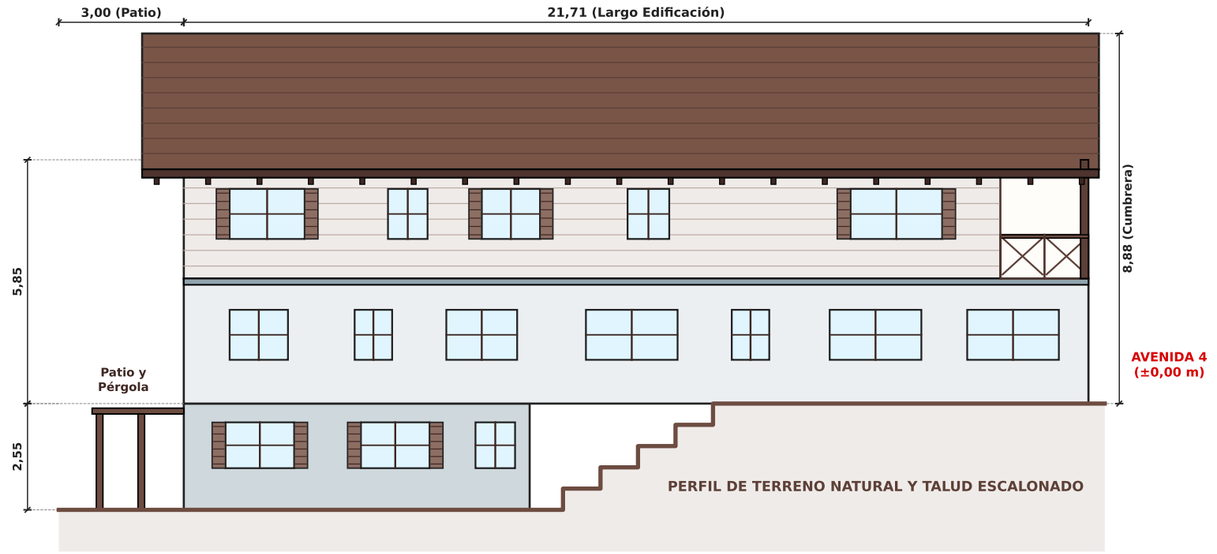

ELEVACIÓN LATERAL COMPLETA — SÓTANO, PLANTA BAJA, SEGUNDO PISO Y TALUD DE TERRENO NATURAL

PLANO DE FACHADAS Y ELEVACIONES ARQUITECTÓNICAS

FACHADA PRINCIPAL AV. 4 • FACHADA POSTERIOR JARDÍN • ELEVACIÓN LATERAL CON DESNIVEL.

PIEDRA RÚSTICA + MADERA MACHIHEMBRADA + CUBIERTA ALPINA 32°

RESPETO ESTRICTO DE MEDIANERA (0,00 m INVASIÓN LINDERO VECINO)

UBICACIÓN:	PROPIEDAD:	LEVANTADO CALCULADO Y DIGITALIZO:	REVISADO:	FECHA:	ESCALA:
AVENIDA 4 ENTRE CALLES 30 Y 31 30-7 MUNICIPIO INDEPENDENCIA ESTADO YARACUY.	ALVARO ARGELIO DIAZ FLOREZ. C.I.: 24.633.787	T.S.U. ANGEL CAMACARO M. CVPT.: N° 1260 SOVIT.: N° 0050	PROYECTO REDISEÑO CHALET ALPINO	OCT 2026	1:75

REPÚBLICA BOLIVARIANA DE VENEZUELA
MUNICIPIO INDEPENDENCIA YARACUY

PROYECTO INTEGRAL: CHALET RÚSTICO ALPINO & COMERCIO

MODELO MAESTRO VERIFICADO | LÁMINA 6 / 6

CUADRO DE COORDENADAS U.T.M.

LADO		RUMBO	DISTANCIA	P	COORDENADAS	
EST	PV				NORTE	ESTE
				1	1.141.664,17	529.755,04
1	2	N 57°10'22,40" E	11,37 m	2	1.141.670,33	529.764,60
2	3	S 30°17'59,36" E	24,72 m	3	1.141.648,99	529.777,07
3	4	S 57°10'22,40" W	10,81 m	4	1.141.643,13	529.767,99
4	1	N 31°36'27,01" W	24,70 m	1	1.141.664,17	529.755,04

ÁREA DE TERRENO POLIGONAL: 273,81 m².

ÁREA TOTAL CONSTRUIDA TECHADA: 477,72 m² (+ 9,24 m² Pérgola).

Desglose: Sótano 74,70 m² | P. Baja 195,39 m² | 2do Piso 195,39 m² | Buhardilla 12,24 m²


LINDEROS.

NORESTE
CASA DE MIGUEL RODRIGUEZ.


SURESTE
SOLAR DE MIGUEL RODRIGUEZ.

NOROESTE
AVENIDA 4.

SUROESTE
CASA DE MARIO GRATEROL.

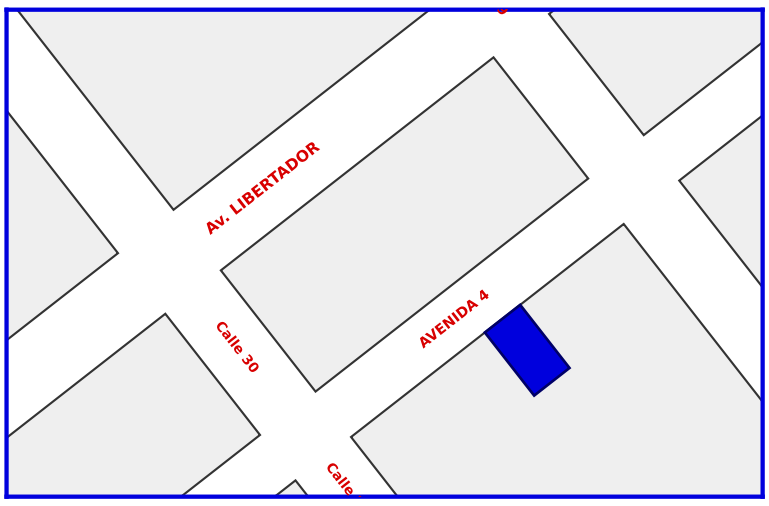

SITUACIÓN RELATIVA S/ESC.

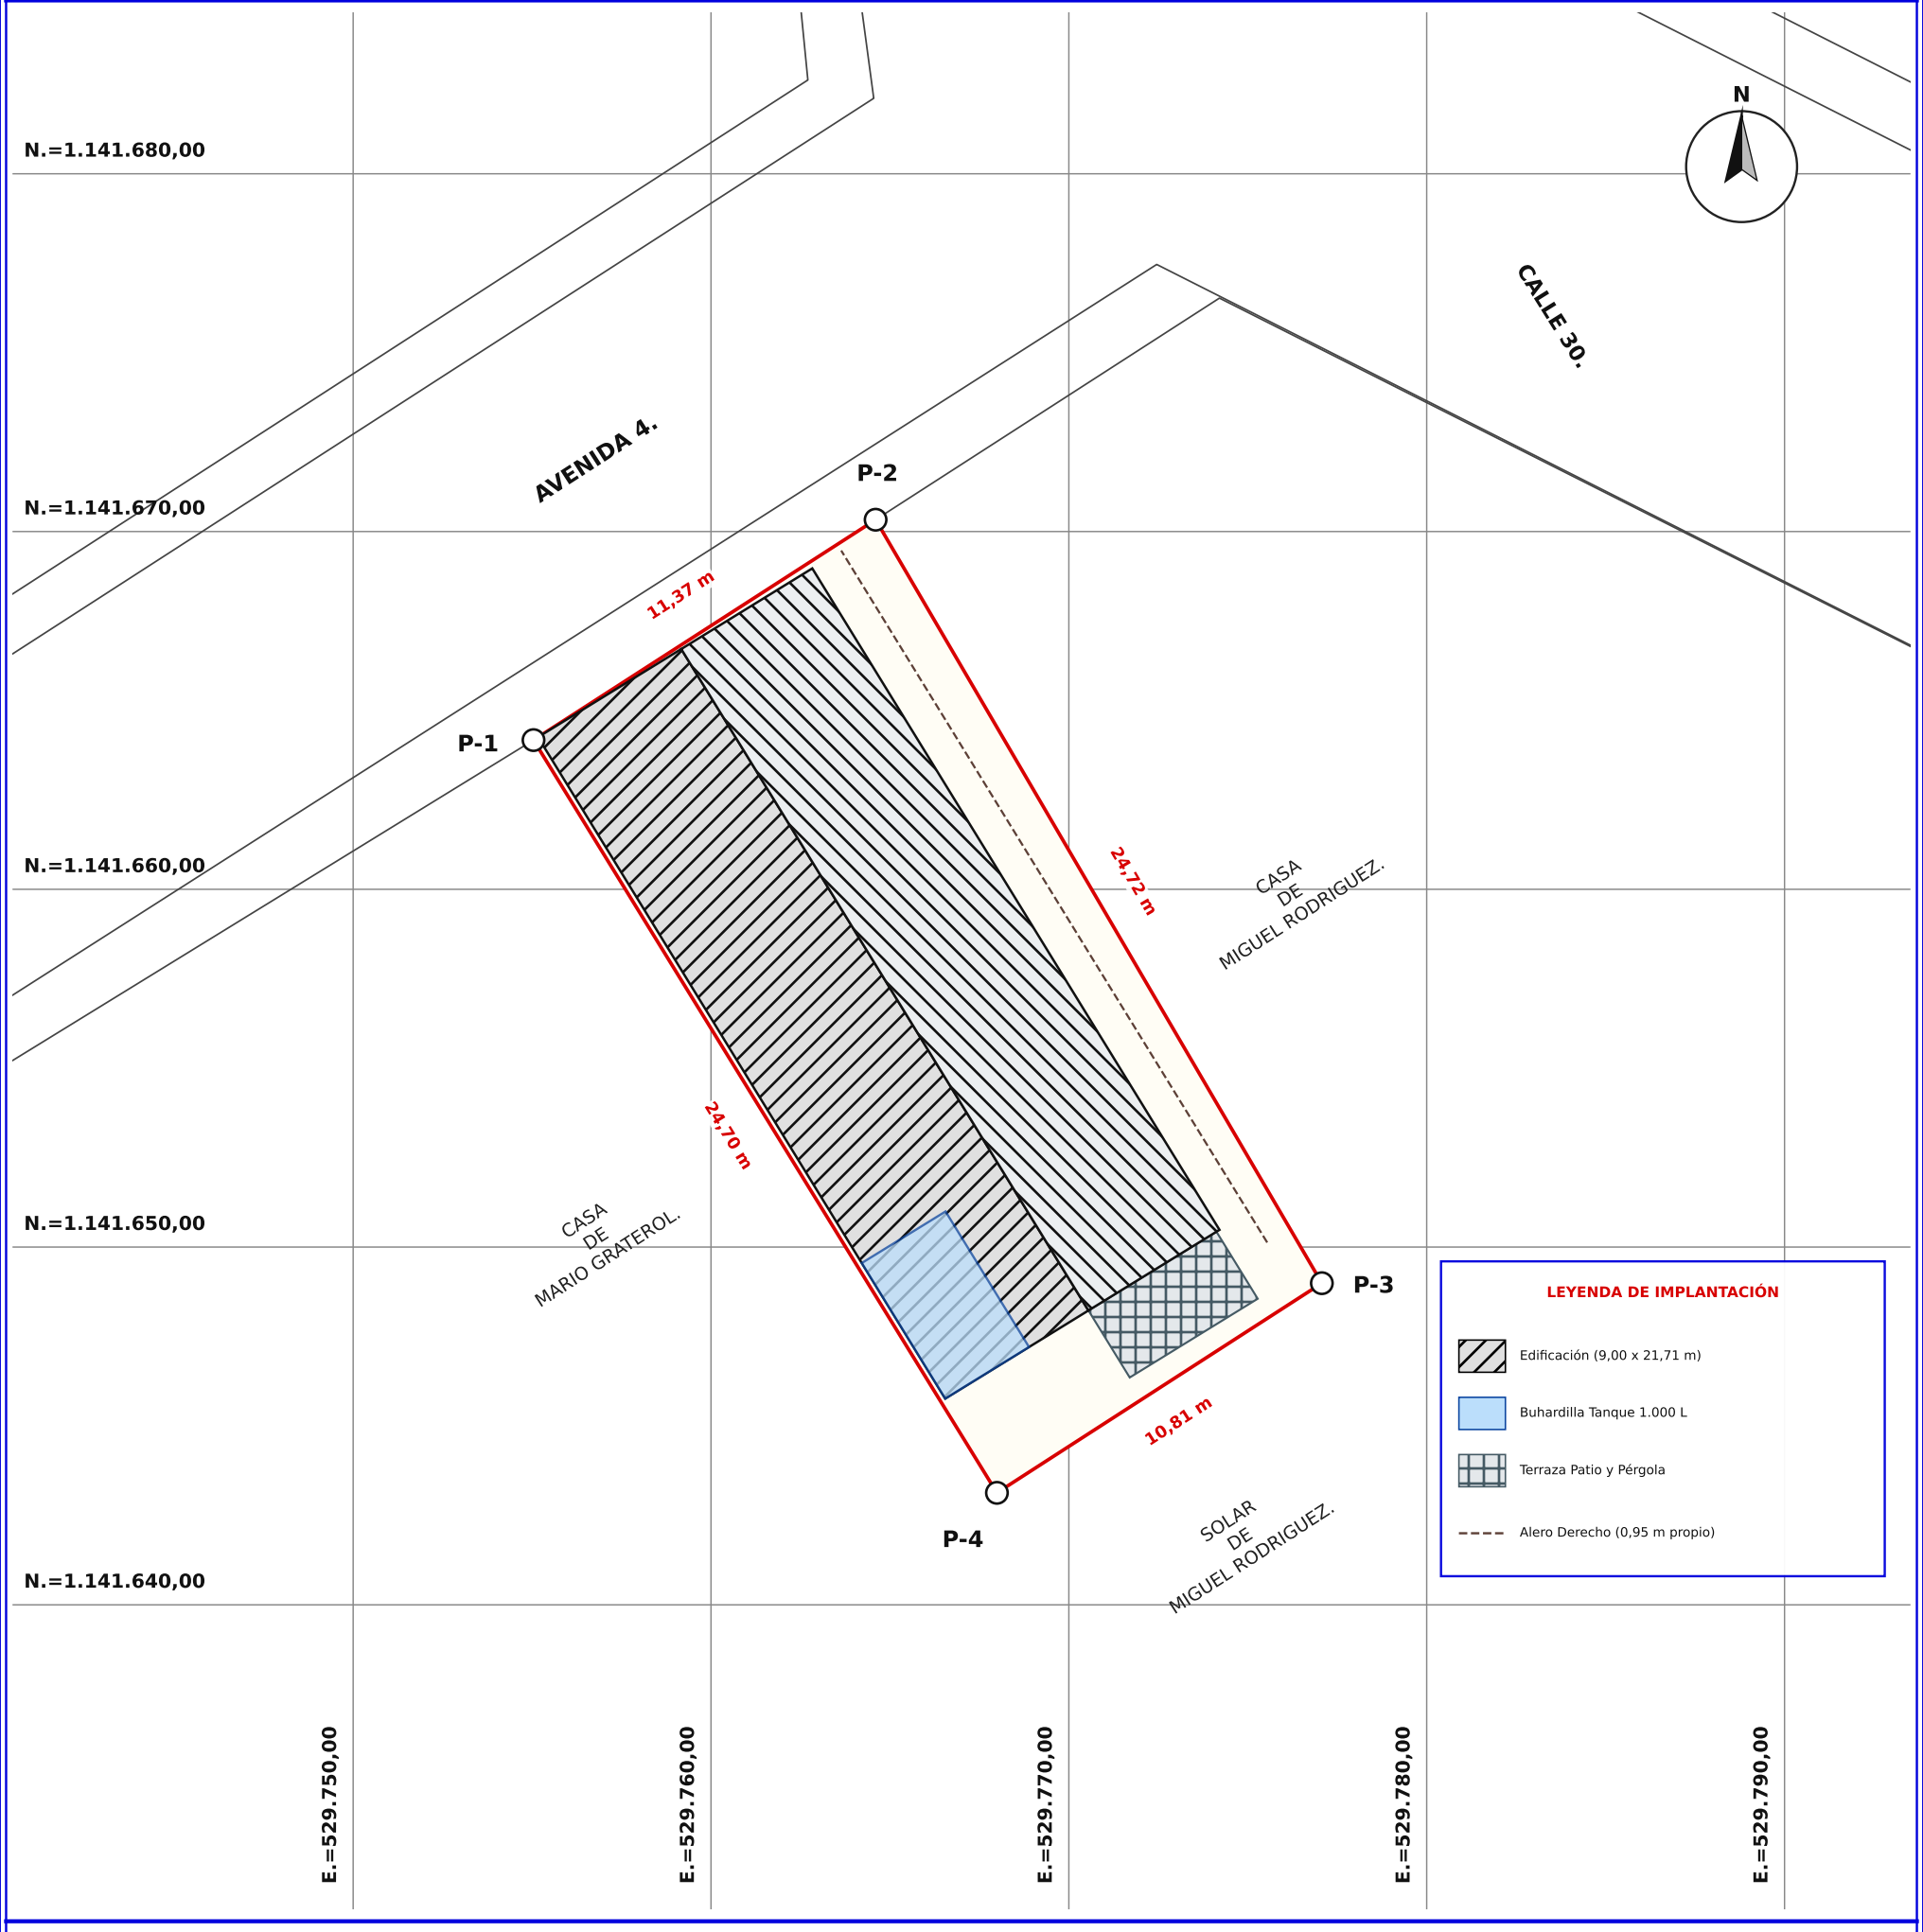

LEVANTAMIENTO POLIGONAL DE LINDEROS

COORDENADAS U.T.M., CUADRO DE ÁREAS, IMPLANTACIÓN Y SITUACIÓN RELATIVA.

ARQUITECTURA EN PIEDRA RÚSTICA Y MADERA

RESPETO ESTRICTO DE LINDEROS (0,00 m INVASIÓN)

UBICACIÓN:	PROPIEDAD:	LEVANTADO CALCULADO Y DIGITALIZO:	REVISADO:	FECHA:	ESCALA:
AVENIDA 4 ENTRE CALLES 30 Y 31 30-7 MUNICIPIO INDEPENDENCIA ESTADO YARACUY.	ALVARO ARGELIO DIAZ FLOREZ. C.I.: 24.633.787	T.S.U. ANGEL CAMACARO M. CVPT.: N° 1260 SOVIT.: N° 0050	PROYECTO REDISEÑO CHALET ALPINO	OCT 2026	1:200