

REPÚBLICA BOLIVARIANA DE VENEZUELA
MUNICIPIO INDEPENDENCIA YARACUY

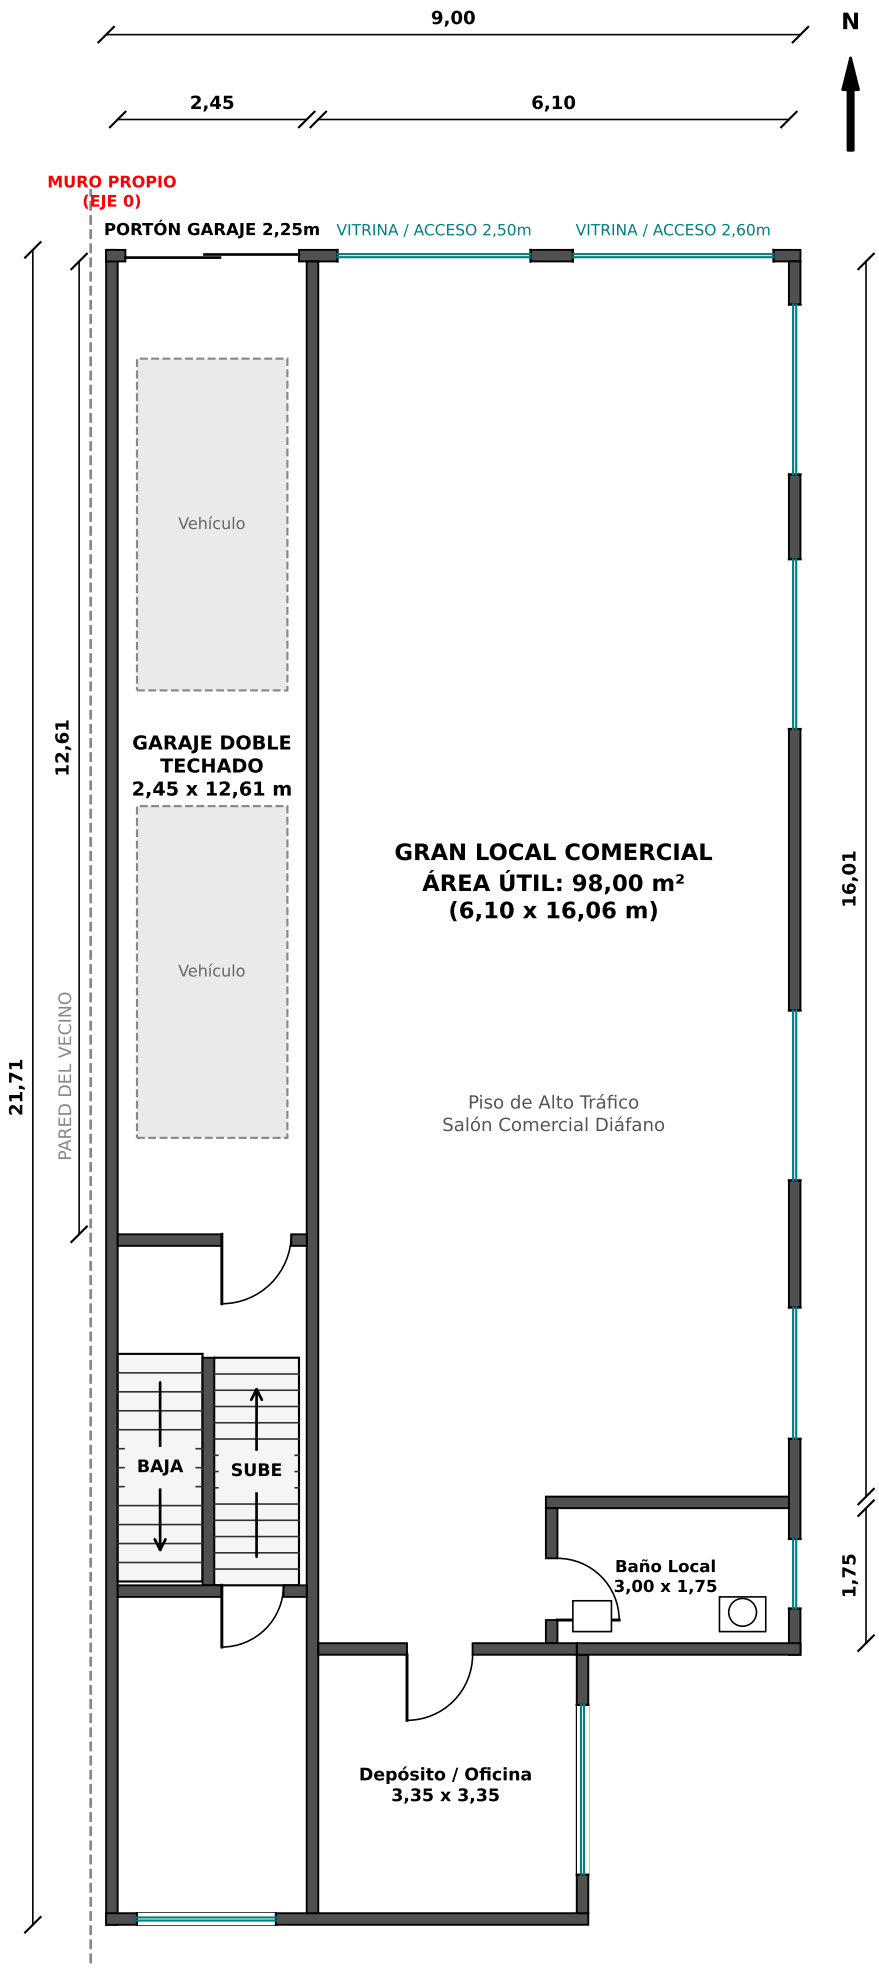

PLANTA BAJA (LOCAL COMERCIAL Y GARAJE)

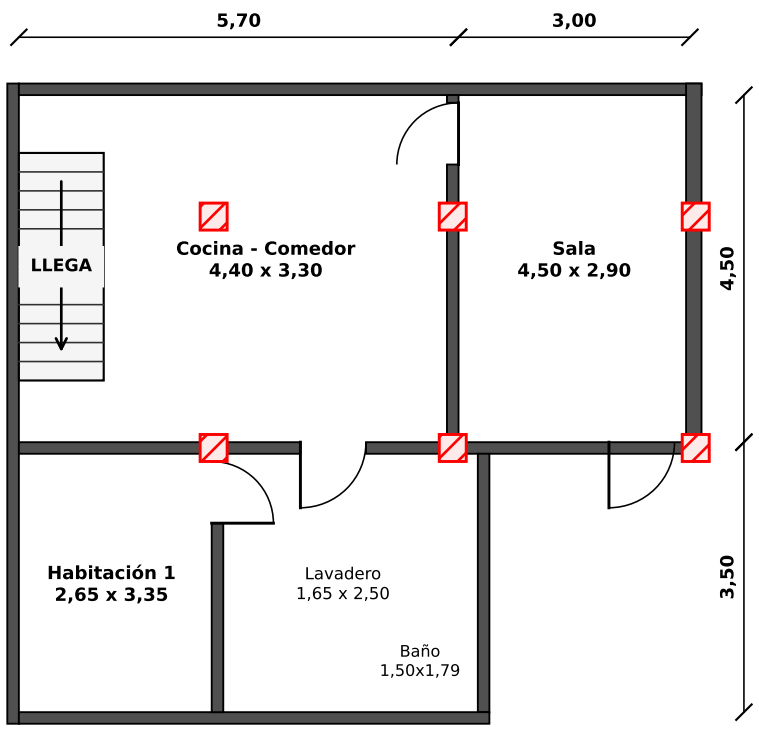


PLANTA SÓTANO

PLANO PLANTA ARQUITECTÓNICA
DISTRIBUCIÓN - PLANTA BAJA Y SÓTANO.

UBICACIÓN:	PROPIEDAD:	LEVANTADO CALCULADO Y DIGITALIZO:	REVISADO:	FECHA:	ESCALA:
AVENIDA 4 ENTRE CALLES 30 Y 31 30-7 MUNICIPIO INDEPENDENCIA ESTADO YARACUY.	ALVARO ARGELIO DIAZ FLOREZ. C.I.: 24.633.787	T.S.U. ANGEL CAMACARO M. CVPT.: N° 1260 SOVIT.: N° 0050		OCT 2026	1:75

REPÚBLICA BOLIVARIANA DE VENEZUELA
MUNICIPIO INDEPENDENCIA YARACUY

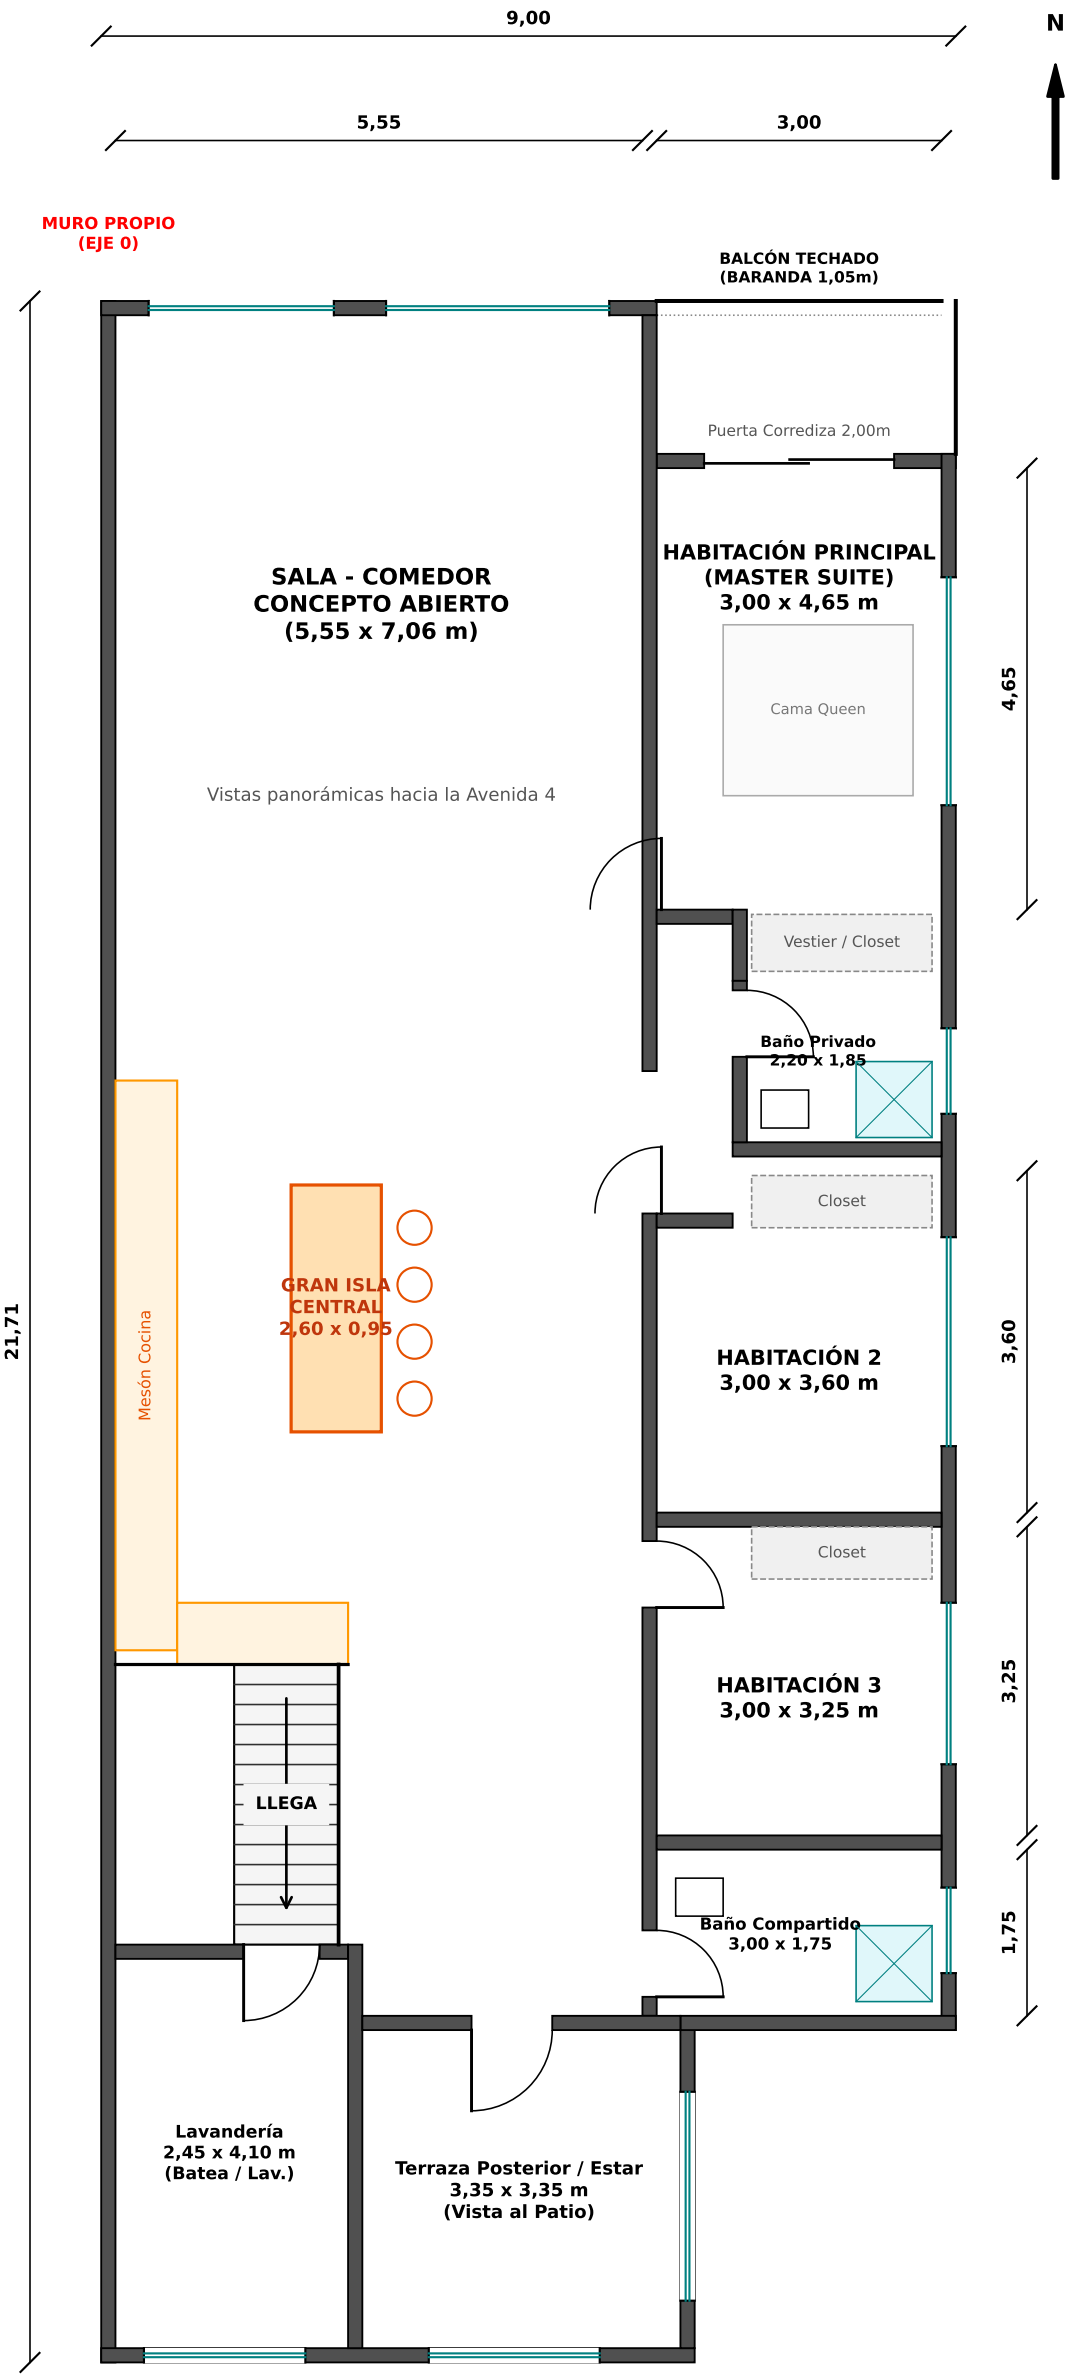


PLANTA SEGUNDO PISO - APARTAMENTO RESIDENCIAL

PLANO PLANTA ARQUITECTÓNICA
DISTRIBUCIÓN - SEGUNDO PISO (APARTAMENTO 3 HABITACIONES).

UBICACIÓN:	PROPIEDAD:	LEVANTADO CALCULADO Y DIGITALIZO:	REVISADO:	FECHA:	ESCALA:
AVENIDA 4 ENTRE CALLES 30 Y 31 30-7 MUNICIPIO INDEPENDENCIA ESTADO YARACUY.	ALVARO ARGELIO DIAZ FLOREZ. C.I.: 24.633.787	T.S.U. ANGEL CAMACARO M. CVPT.: N° 1260 SOVIT.: N° 0050		OCT 2026	1:75

REPÚBLICA BOLIVARIANA DE VENEZUELA

MUNICIPIO INDEPENDENCIA YARACUY

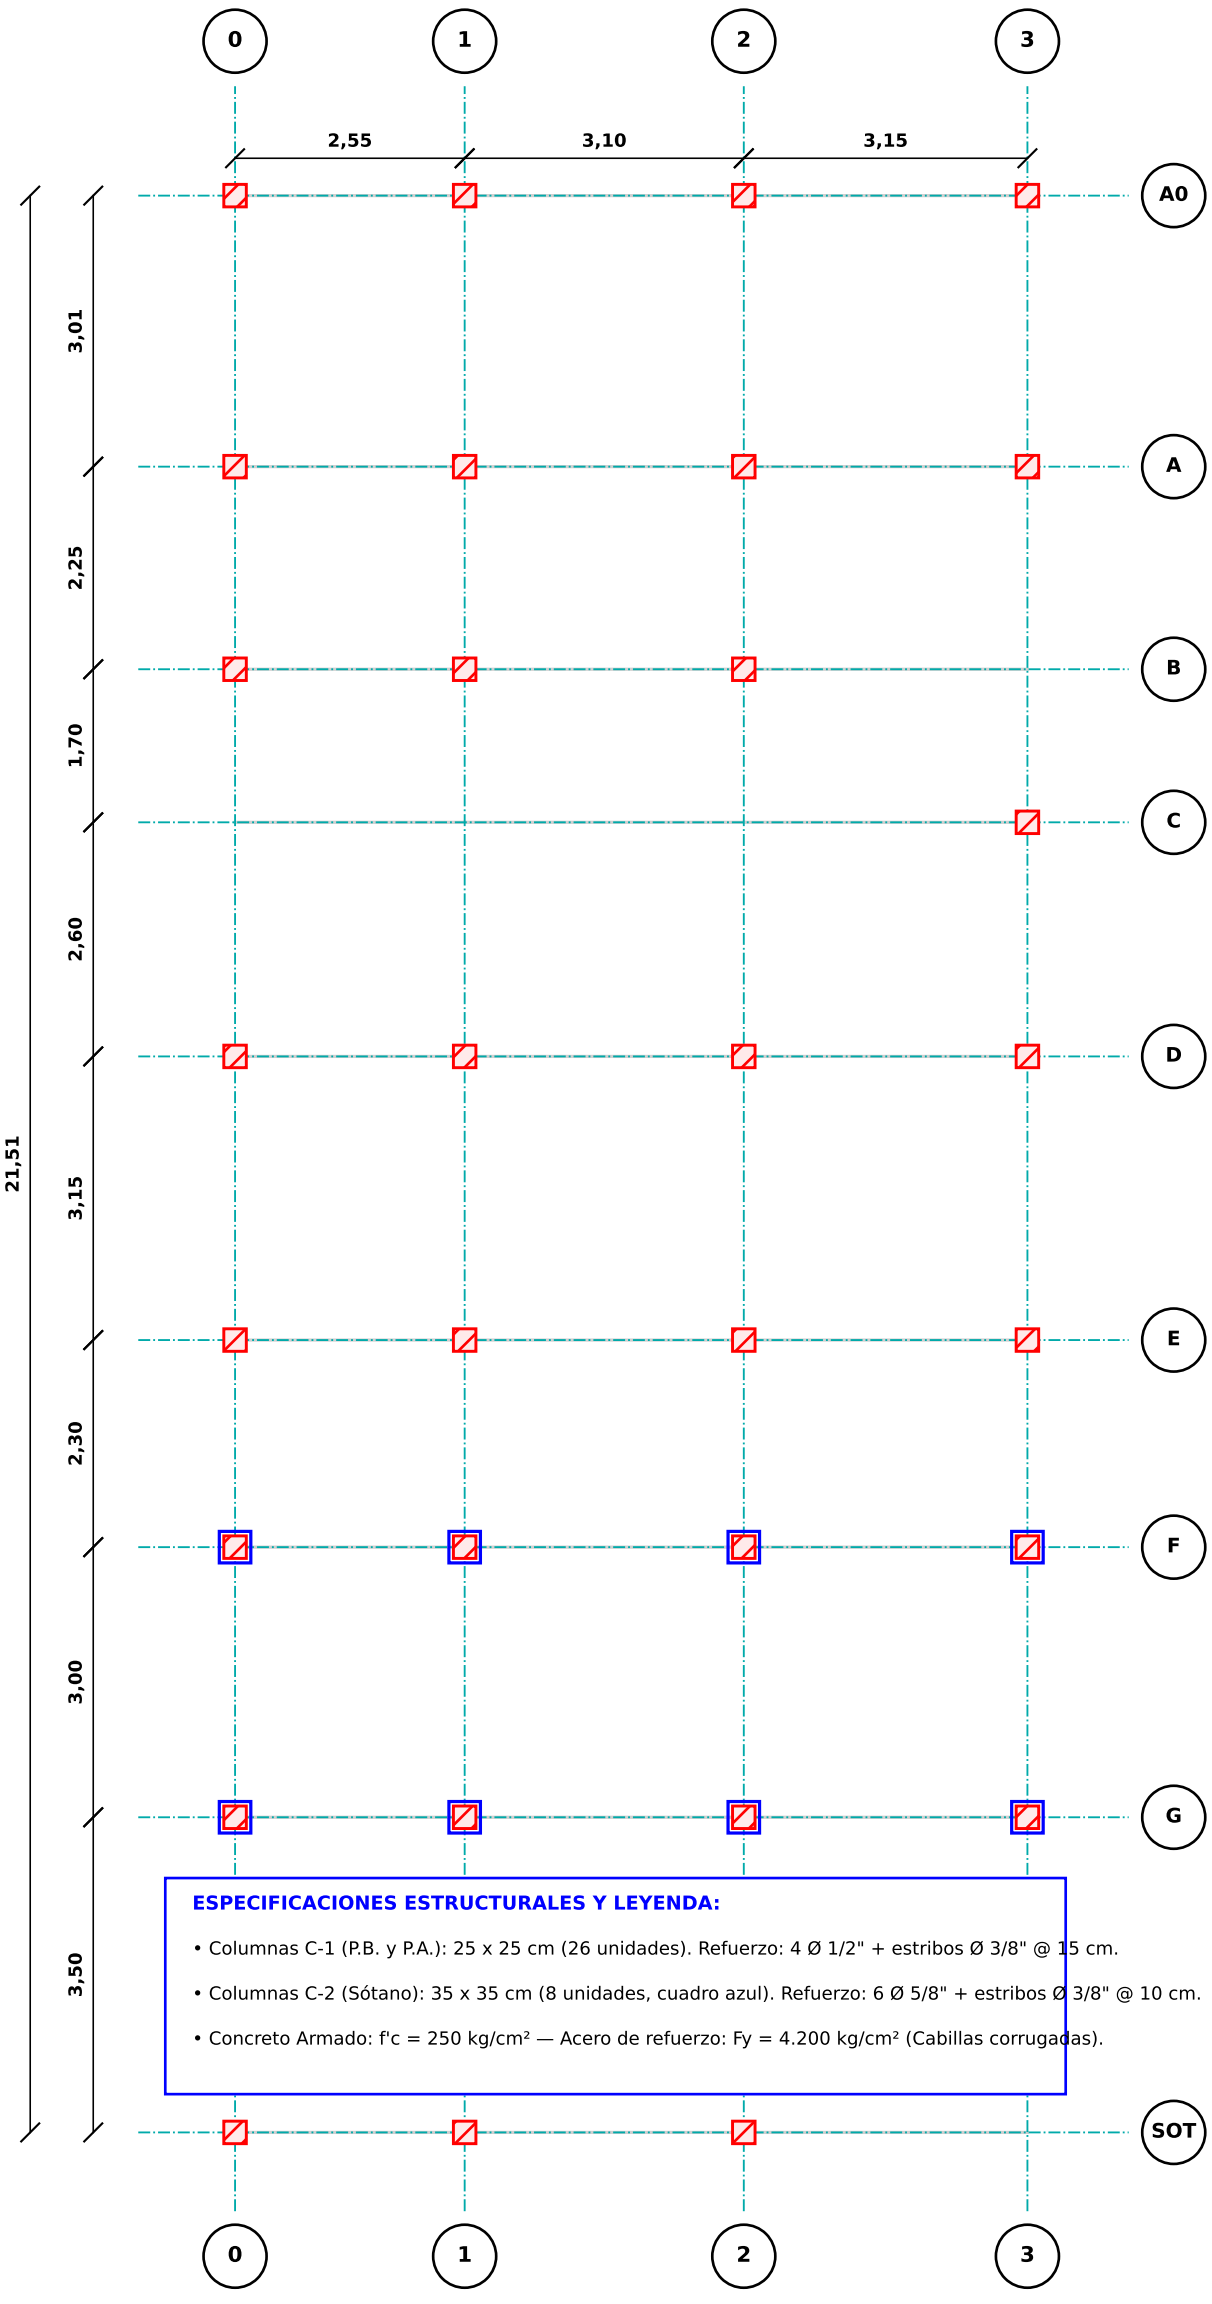


DISTRIBUCIÓN MODULAR DE EJES Y COLUMNAS

PLANO DISTRIBUCIÓN DE COLUMNAS Y EJES


PRIMER Y SEGUNDO PISO: 25 x 25 (cm) — SÓTANO: 35 x 35 (cm).

UBICACIÓN:	PROPIEDAD:	LEVANTADO CALCULADO Y DIGITALIZO:	REVISADO:	FECHA:	ESCALA:
AVENIDA 4 ENTRE CALLES 30 Y 31 30-7 MUNICIPIO INDEPENDENCIA ESTADO YARACUY.	ALVARO ARGELIO DIAZ FLOREZ. C.I.: 24.633.787	T.S.U. ANGEL CAMACARO M. CVPT.: N° 1260 SOVIT.: N° 0050		OCT 2026	1:75


REPÚBLICA BOLIVARIANA DE VENEZUELA
MUNICIPIO INDEPENDENCIA YARACUY

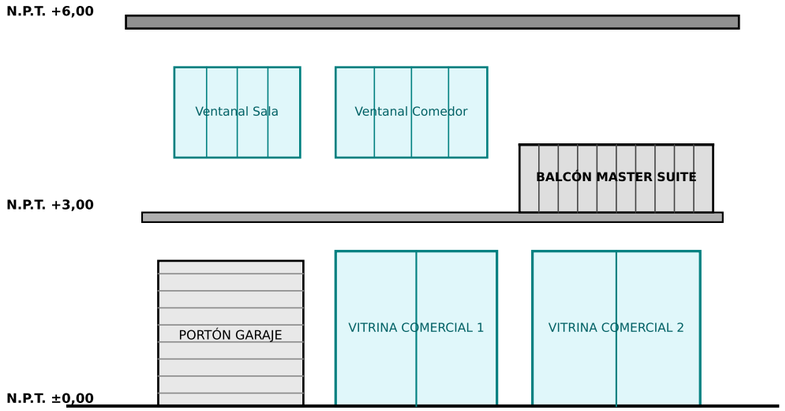

FACHADA PRINCIPAL (AVENIDA 4)

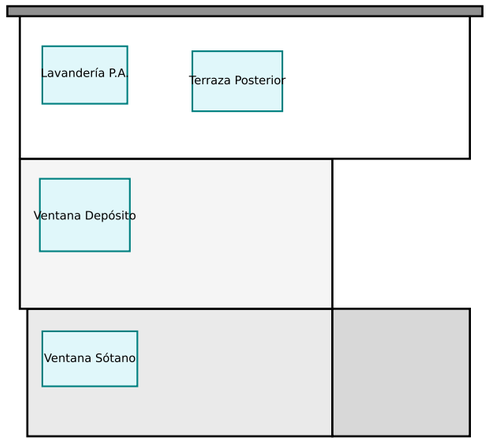

FACHADA POSTERIOR (SÓTANO - P.B. - P.A.)

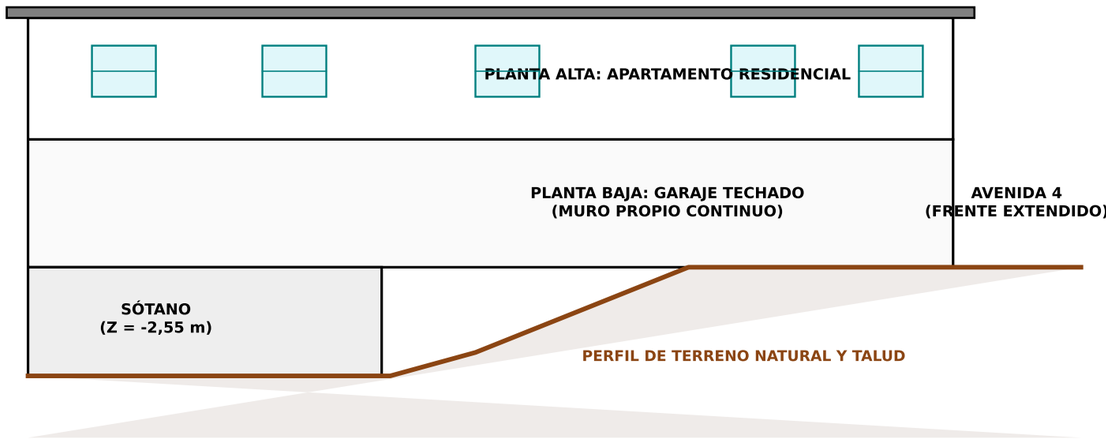

FACHADA LATERAL IZQUIERDA (SÓTANO + P.B. + P.A. + TALUD DE TERRENO)

PLANO FACHADAS Y ELEVACIONES
FACHADA PRINCIPAL (AV. 4) — FACHADA LATERAL IZQUIERDA — FACHADA POSTERIOR.

UBICACIÓN:	PROPIEDAD:	LEVANTADO CALCULADO Y DIGITALIZO:	REVISADO:	FECHA:	ESCALA:
AVENIDA 4 ENTRE CALLES 30 Y 31 30-7 MUNICIPIO INDEPENDENCIA ESTADO YARACUY.	ALVARO ARGELIO DIAZ FLOREZ. C.I.: 24.633.787	T.S.U. ANGEL CAMACARO M. CVPT.: N° 1260 SOVIT.: N° 0050		OCT 2026	1:75


REPÚBLICA BOLIVARIANA DE VENEZUELA
MUNICIPIO INDEPENDENCIA YARACUY

CUADRO DE COORDENADAS U.T.M.

LADO EST-PV	RUMBO	DISTANCIA	P	NORTE	ESTE
1 - 2	N 57°10'22.40" E	11.37 m	1	1.141.664,17	529.755,04
2 - 3	S 30°17'59.36" E	24.72 m	2	1.141.670,33	529.764,60
3 - 4	S 57°10'22.40" W	10.81 m	3	1.141.648,99	529.777,07
4 - 1	N 31°36'27.01" W	24.70 m	4	1.141.643,13	529.767,99

LINDEROS

LINDERO	COLINDANTE
NORESTE	CASA DE MIGUEL RODRIGUEZ
SURESTE	SOLAR DE MIGUEL RODRIGUEZ
NOROESTE	AVENIDA 4
SUROESTE	CASA DE MARIO GRATEROL

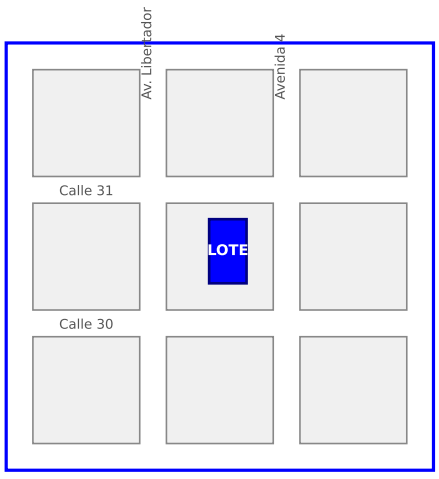


SITUACIÓN RELATIVA S/ESC.

ÁREA DE TERRENO: 273,81 m²

ÁREA DE CONSTRUCCIÓN TOTAL: 372,50 m²

(Sótano: 80,45 m² | Planta Baja: 149,85 m² | Planta Alta: 142,20 m²)

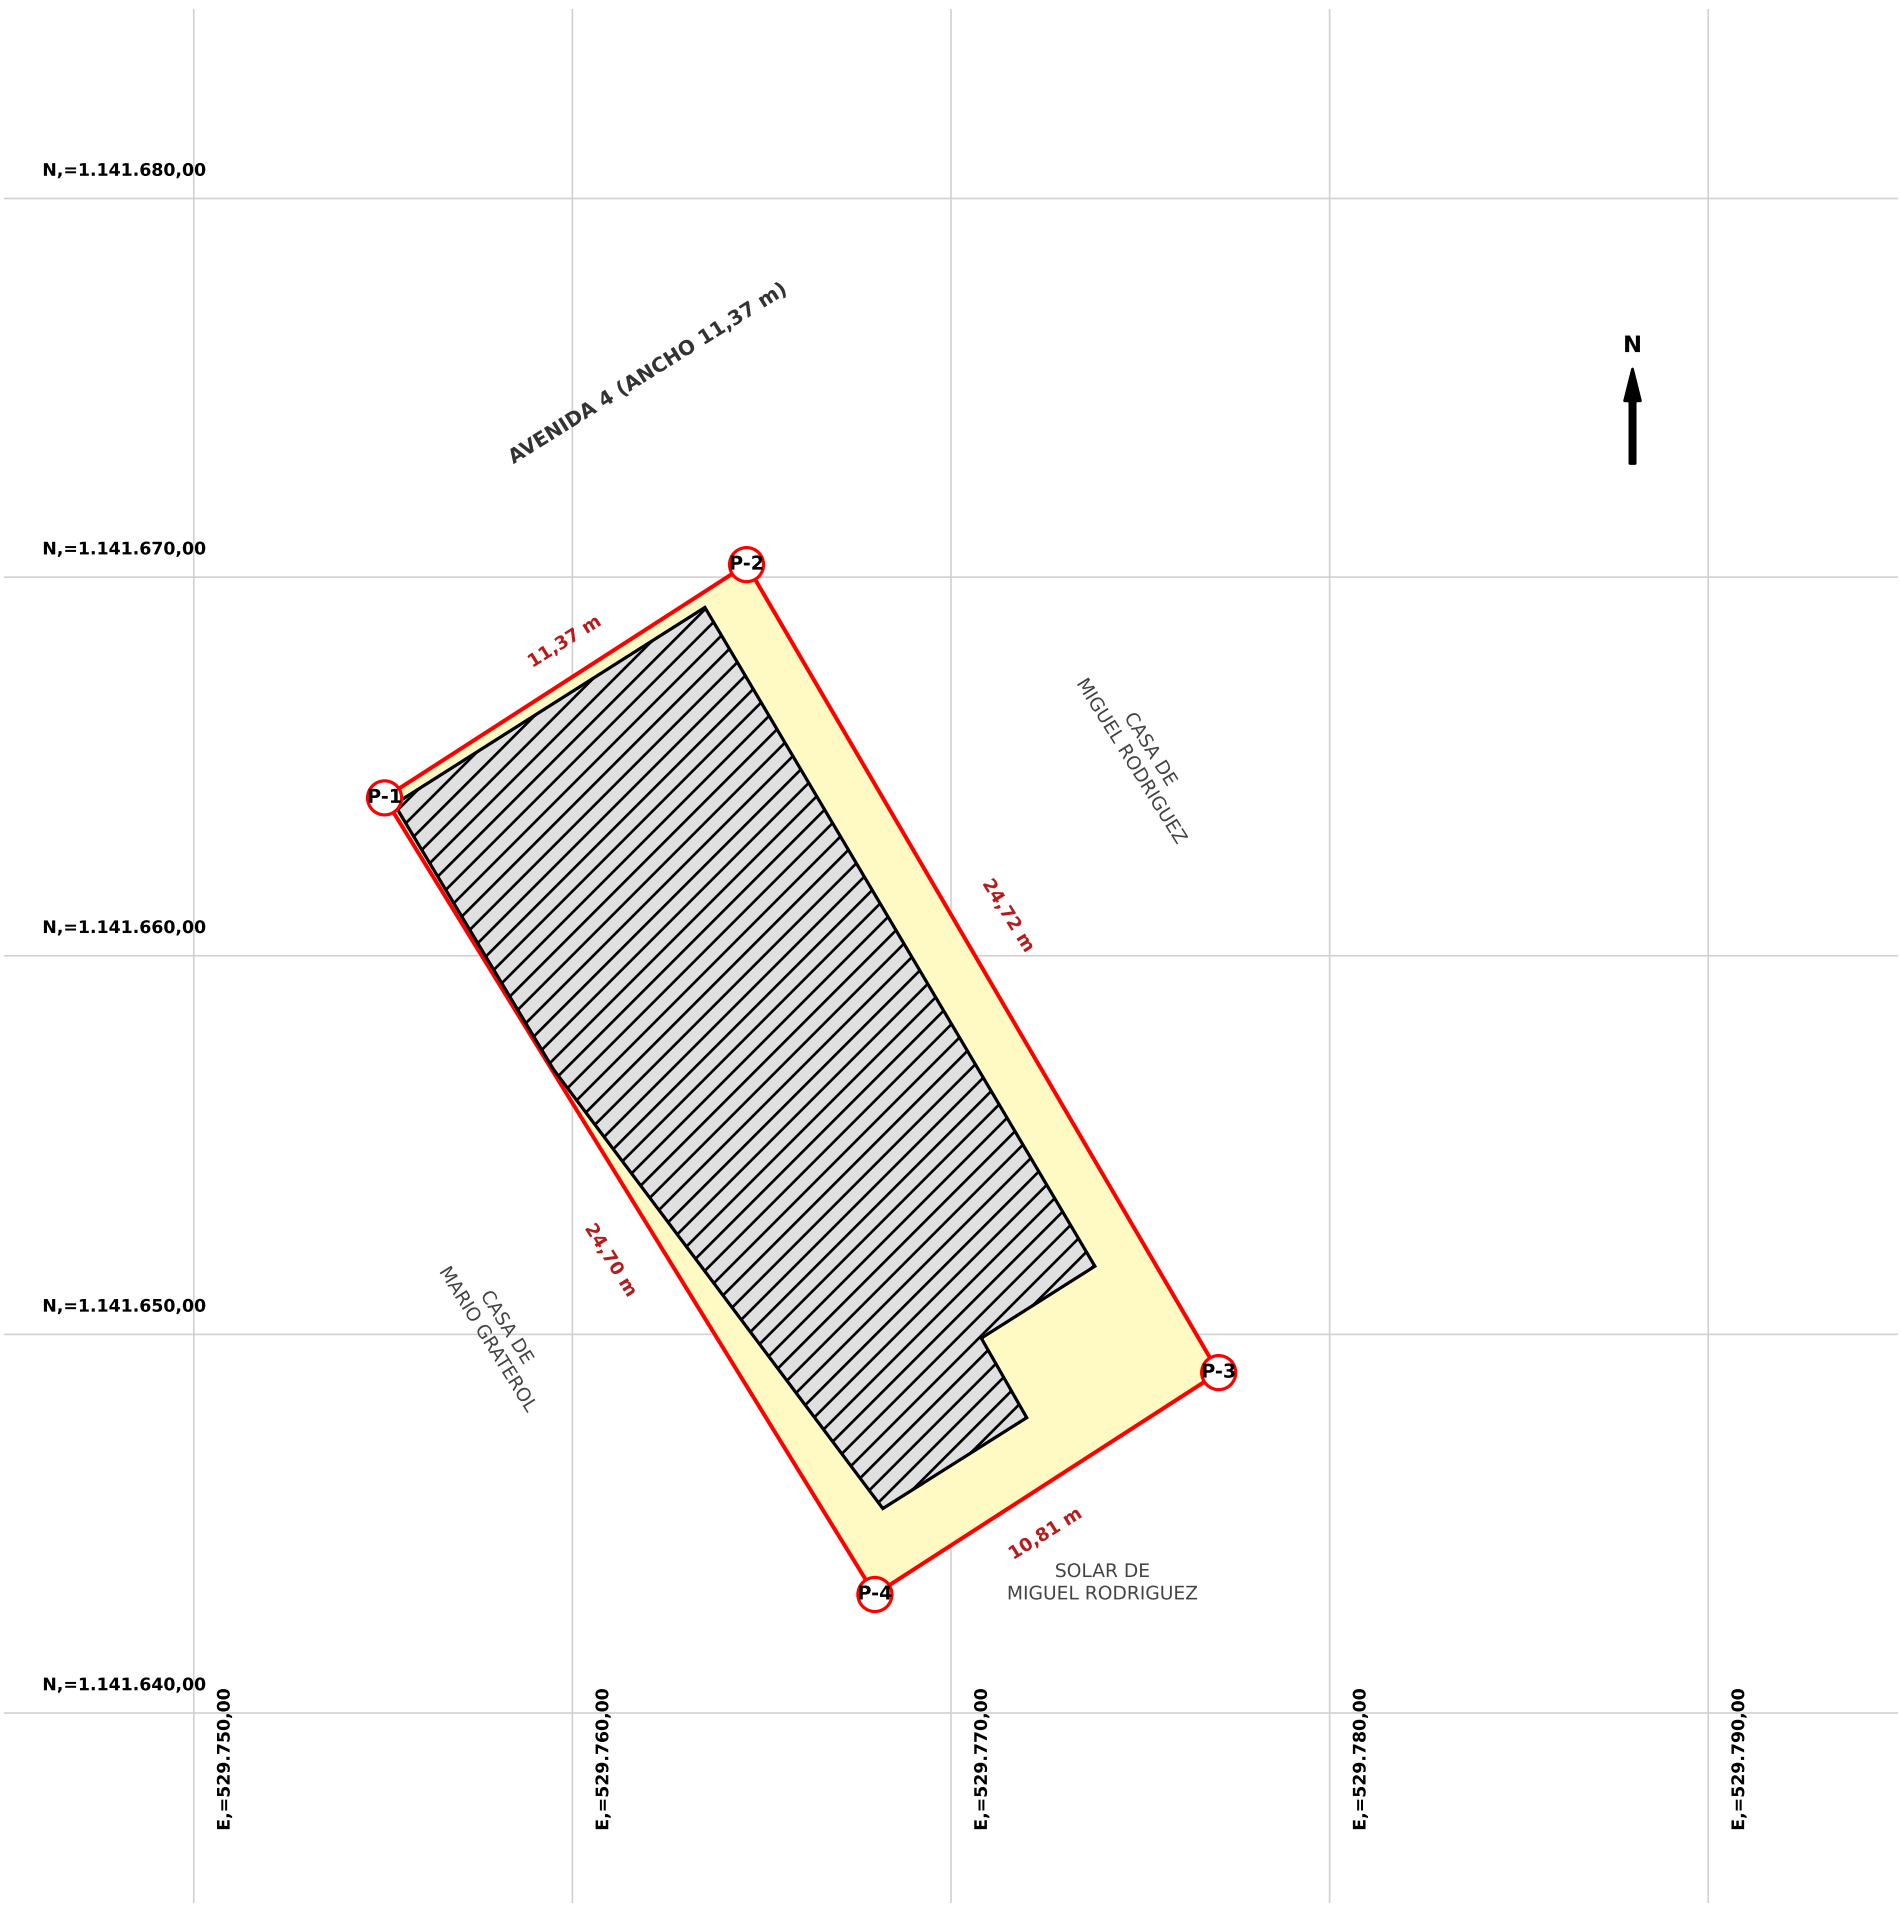

LEVANTAMIENTO POLIGONAL DE LINDEROS
TOPOGRAFÍA Y COORDENADAS U.T.M. — SITUACIÓN RELATIVA.

UBICACIÓN:	PROPIEDAD:	LEVANTADO CALCULADO Y DIGITALIZO:	REVISADO:	FECHA:	ESCALA:
AVENIDA 4 ENTRE CALLES 30 Y 31 30-7 MUNICIPIO INDEPENDENCIA ESTADO YARACUY.	ALVARO ARGELIO DIAZ FLOREZ. C.I.: 24.633.787	T.S.U. ANGEL CAMACARO M. CVPT.: N° 1260 SOVIT.: N° 0050		OCT 2026	1:200