



Porche.
2,25
2,20
3,00
Habitacion 1.
2,10
0,95
3,80
1,95
2,05
0,60
0,70
Baño.
1,85
Garaje.
Sala.
2,60
7,45
0,70
2,05
0,60
10,20
2,95
3,95
3,60
Habitacion 2.
15,15
3,00
2,60
0,70
1,25
2,75
Habitacion 3.
3,25
Comedor.
3,10
3,00
2,95
0,70
Baño.
1,75
3,00
0,70
2,45
Cocina.
2,60
3,35
3,35
Habitacion 4.
Lavadero.
1,50
2,60

PLANTA CASA.

REPÚBLICA BOLIVARIANA DE VENEZUELA
MUNICIPIO INDEPENDENCIA YARACUY

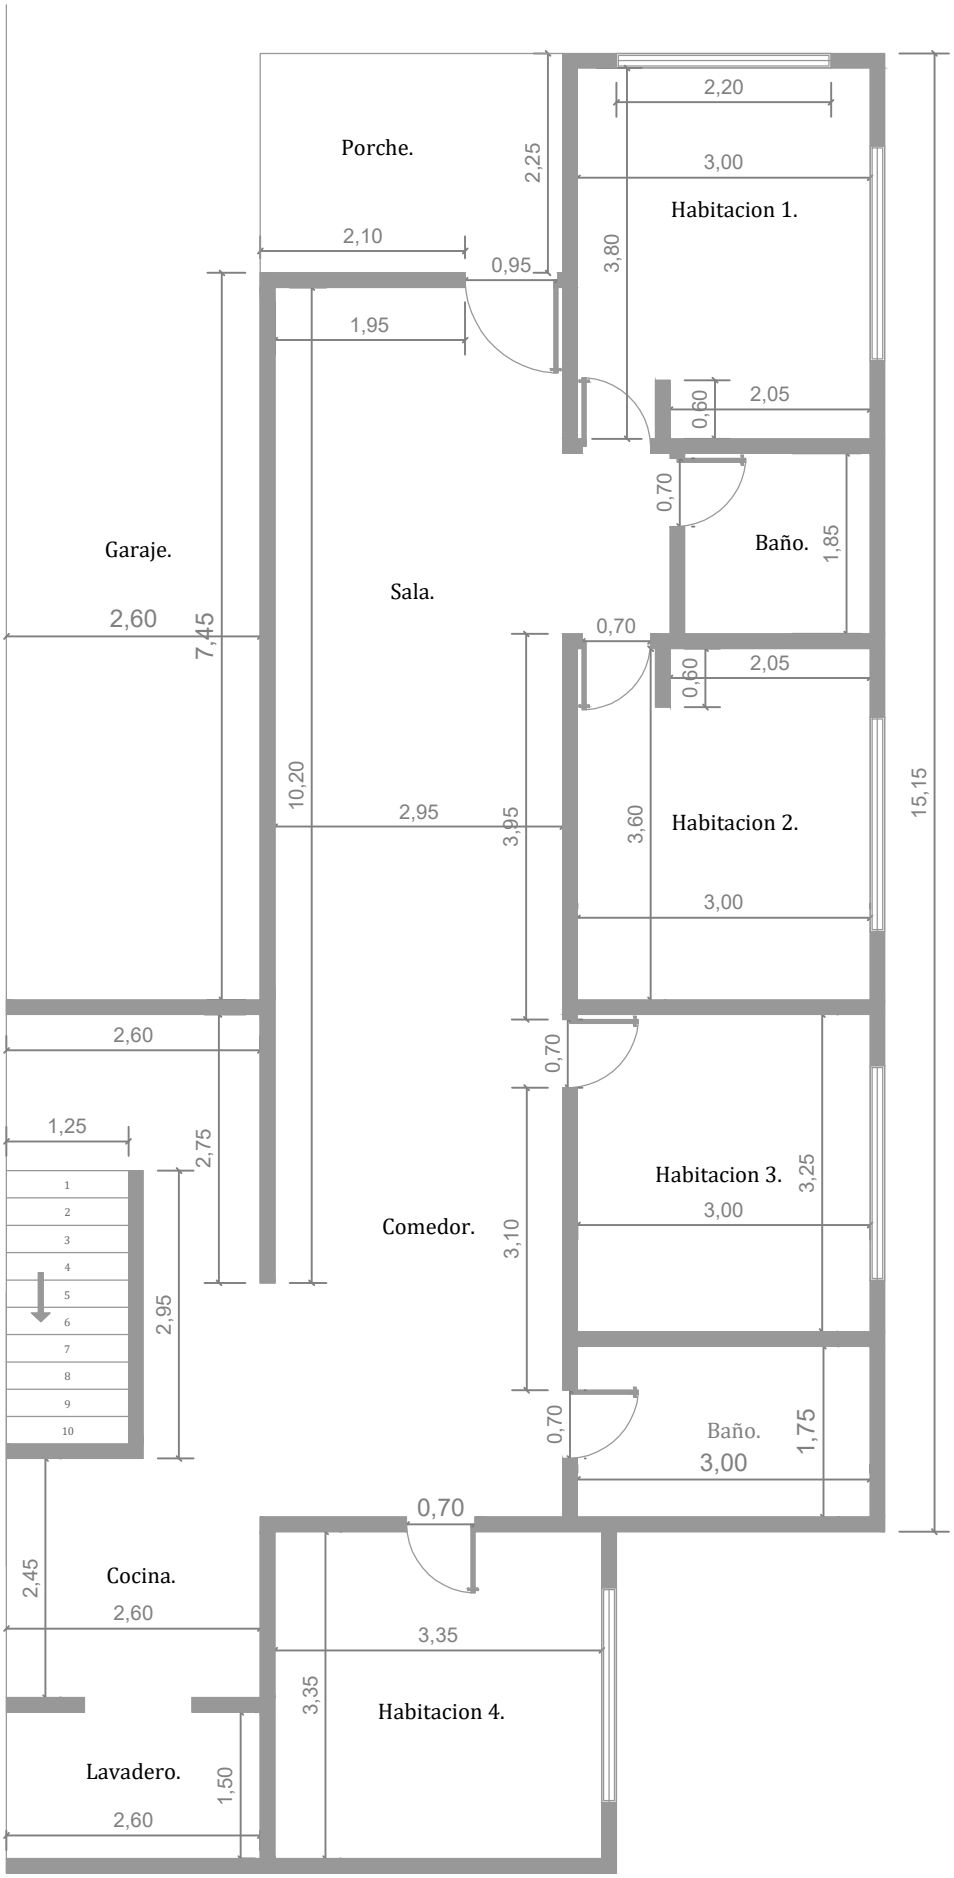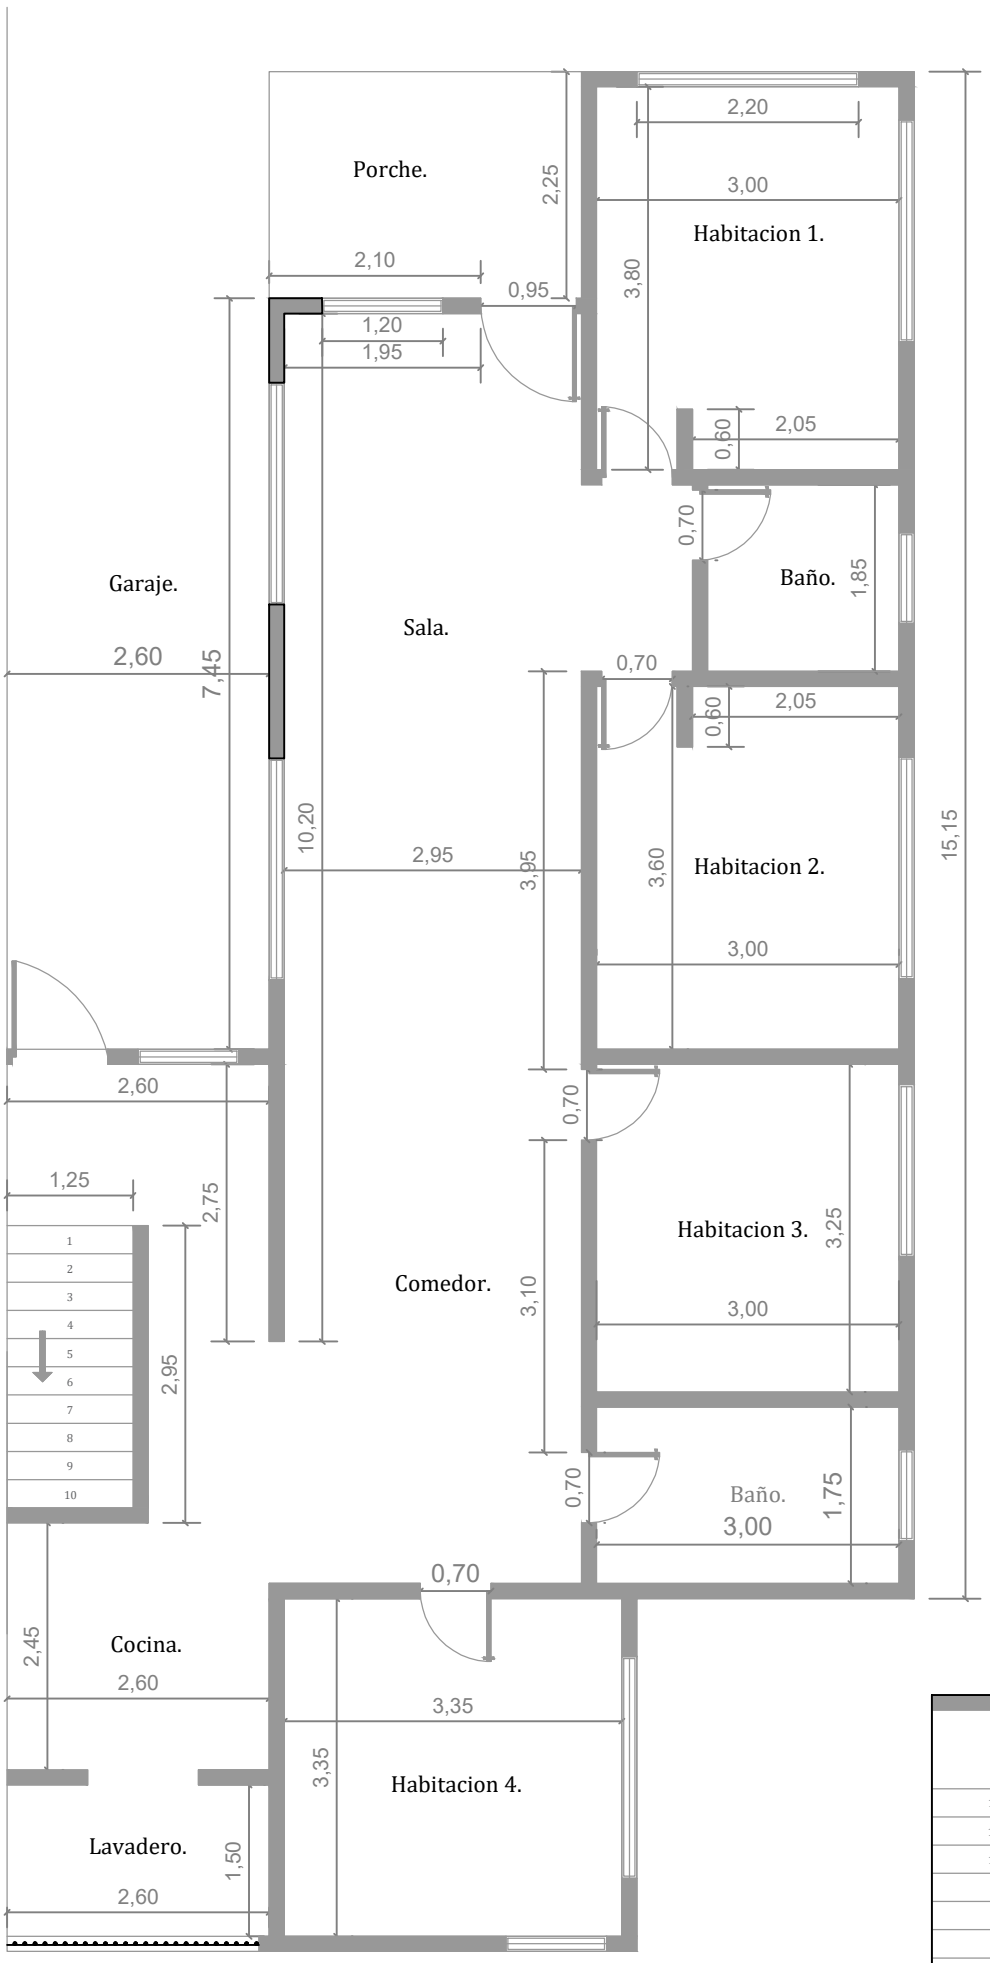

PLANTA CASA.

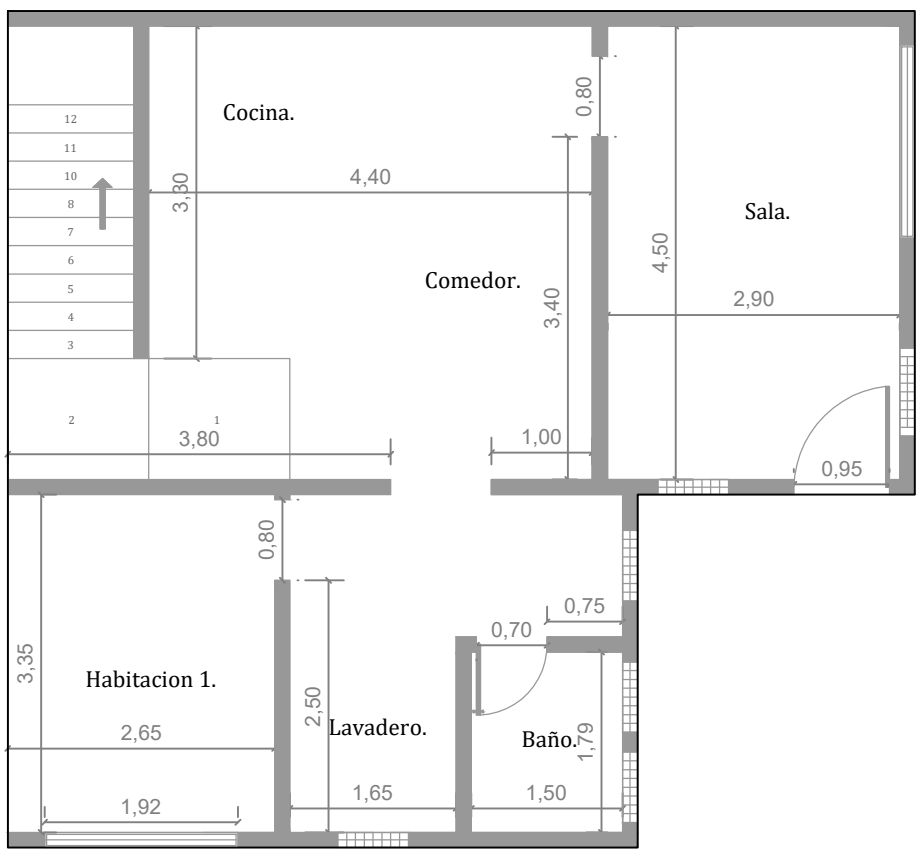


PLANTA SÓTANO.


PLANO PLANTA ARQUITECTÓNICA
DISTRIBUCIÓN.

UBICACIÓN:	PROPIEDAD:	LEVANTADO CALCULADO Y DIGITALIZO:	REVISADO:	FECHA:	ESCALA:
AVENIDA 4 ENTRE CALLES 30 Y 31 30-7 MUNICIPIO INDEPENDENCIA ESTADO YARACUY. .	ALVARO ARGELIO DIAZ FLOREZ. C.I.: 24.633.787	T.S.U. ANGEL CAMACARO M. CVPT.:N°1260 SOVIT.:N°0050		MAR 2026	1:75

REPÚBLICA BOLIVARIANA DE VENEZUELA
MUNICIPIO INDEPENDENCIA YARACUY

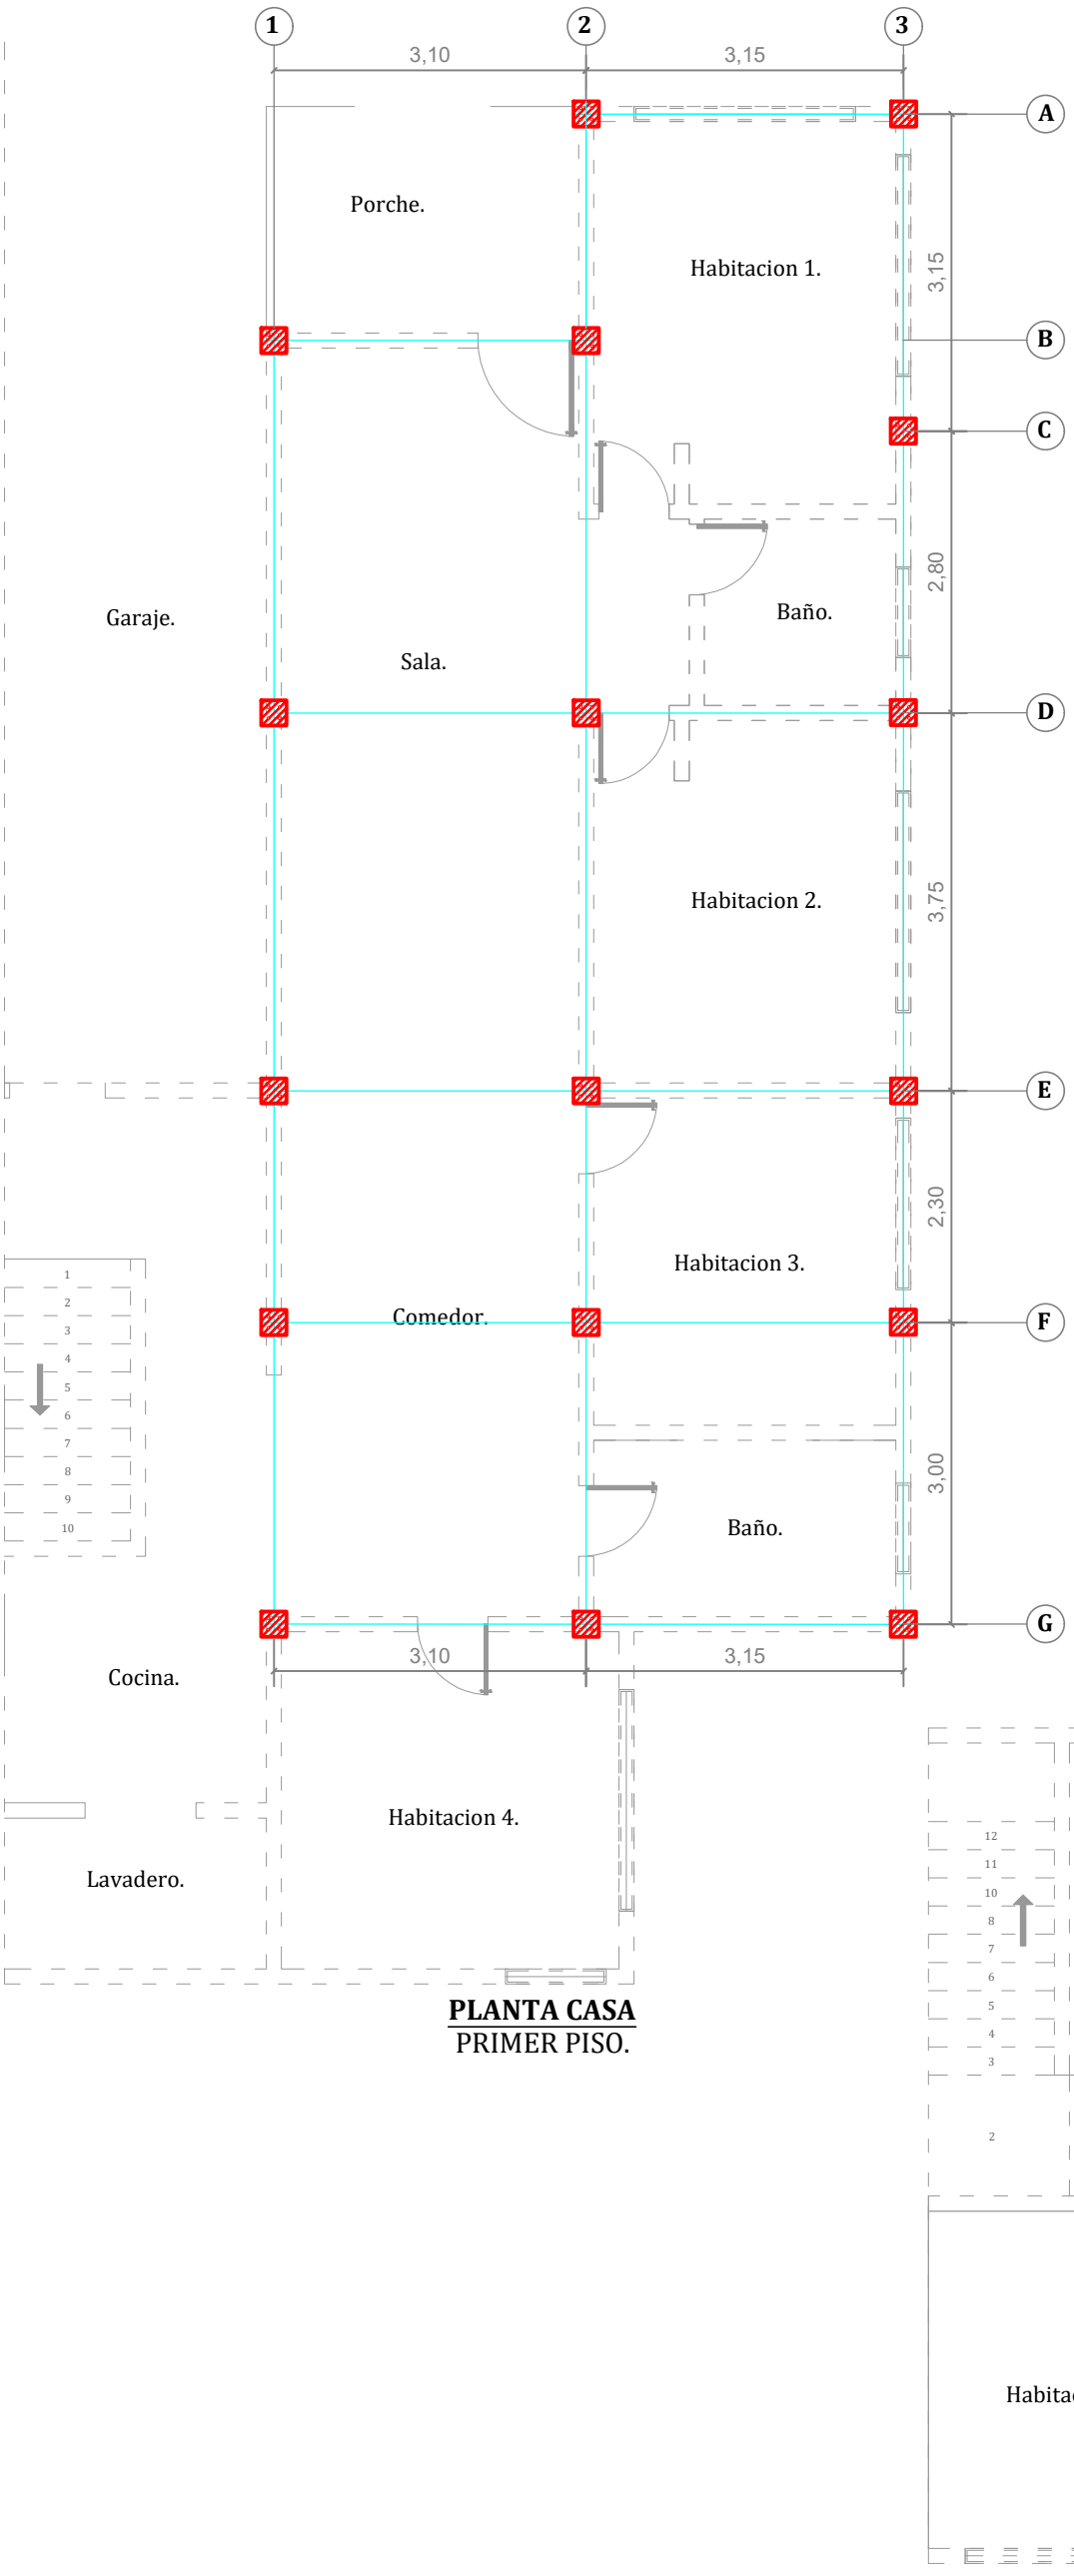

PLANTA CASA
PRIMER PISO.

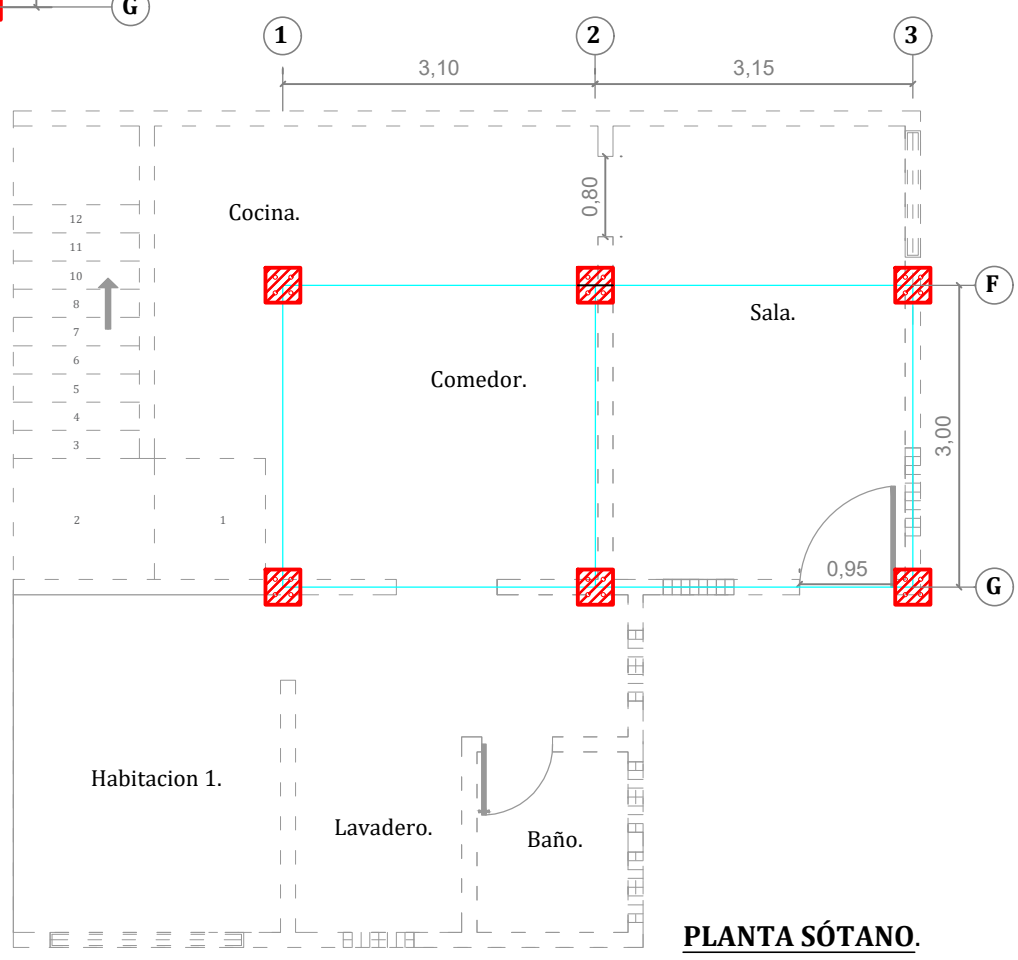


PLANTA SÓTANO.


PLANO DISTRIBUCIÓN DE COLUMNAS
PRIMER PISO25 x 25(cm) SÓTANO 35 x 35 (cm).

UBICACIÓN:	PROPIEDAD:	LEVANTADO CALCULADO Y DIGITALIZO:	REVISADO:	FECHA:	ESCALA:
AVENIDA 4 ENTRE CALLES 30 Y 31 30-7 MUNICIPIO INDEPENDENCIA ESTADO YARACUY.	ALVARO ARGELIO DIAZ FLOREZ. C.I.: 24.633.787	T.S.U. ANGEL CAMACARO M. CVPT.:N°1260 SOVIT.:N°0050		MAR 2026	1:75


REPÚBLICA BOLIVARIANA DE VENEZUELA
MUNICIPIO INDEPENDENCIA YARACUY

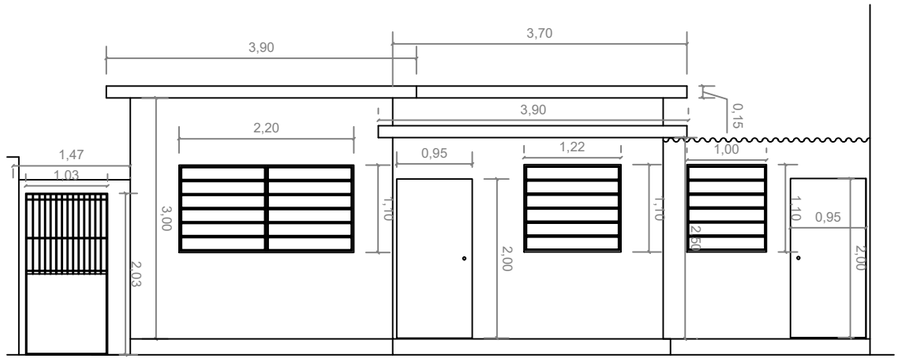

FACHADA PRINCIPAL
PRIMER PISO.

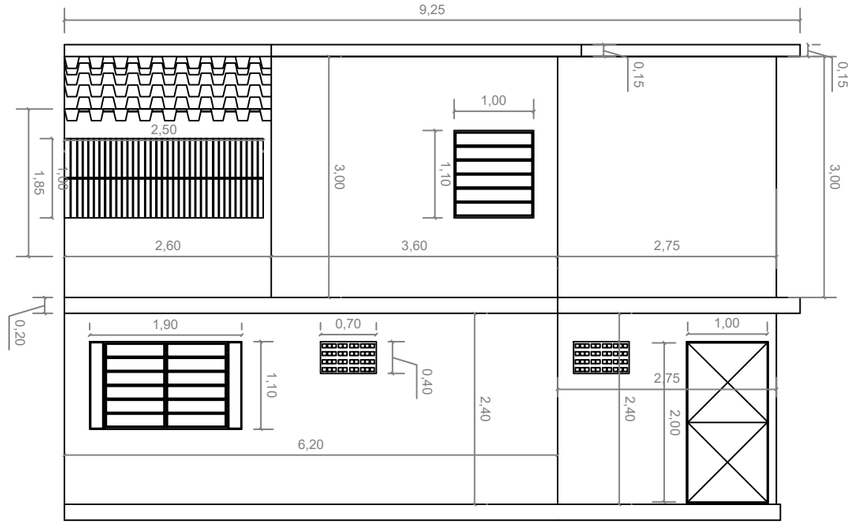

FACHADA POSTERIOR
PRIMER PISO - SÓTANO.

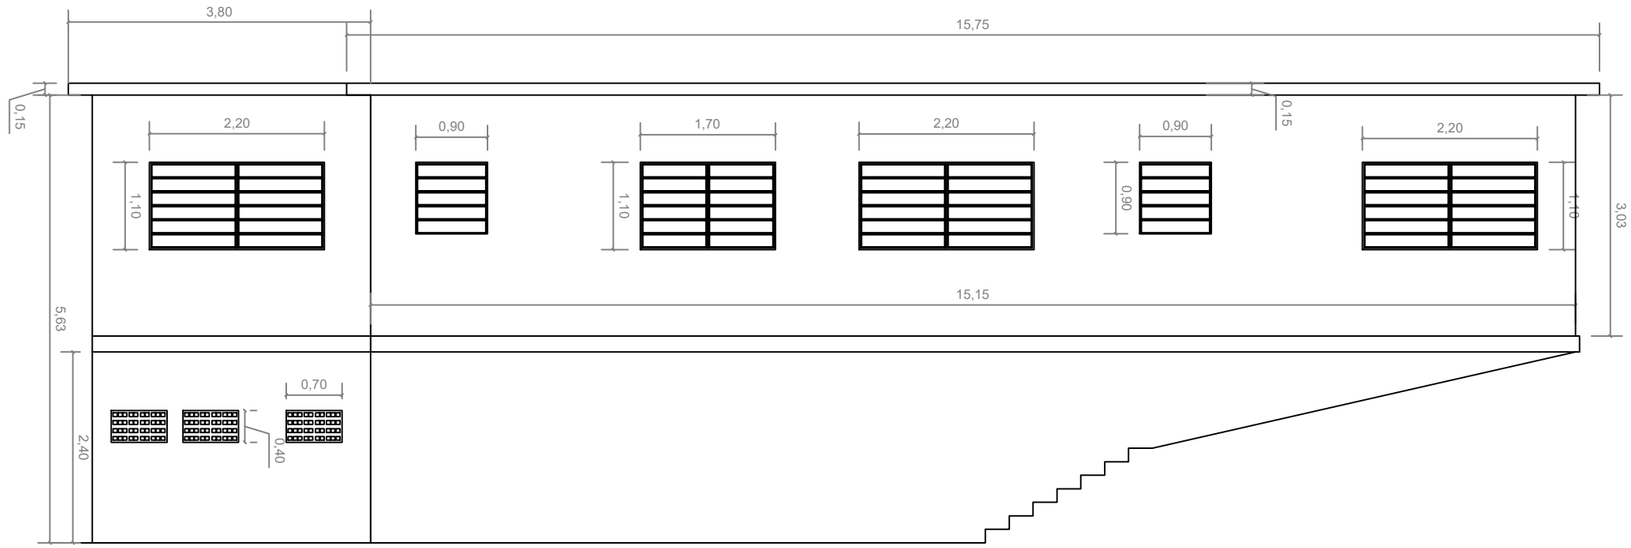

FACHADA LATERAL IZQUIERDA.
PRIMER PISO - SOTANO.

PLANO DISTRIBUCIÓN DE COLUMNAS FACHADAS.

UBICACIÓN:	PROPIEDAD:	LEVANTADO CALCULADO Y DIGITALIZO:	REVISADO:	FECHA:	ESCALA:
AVENIDA 4 ENTRE CALLES 30 Y 31 30-7 MUNICIPIO INDEPENDENCIA ESTADO YARACUY.	ALVARO ARGELIO DIAZ FLOREZ. C.I.: 24.633.787	T.S.U. ANGEL CAMACARO M. CVPT.:N°1260 SOVIT.:N°0050		MAR 2026	1:75

REPÚBLICA BOLIVARIANA DE VENEZUELA
MUNICIPIO INDEPENDENCIA YARACUY

CUADRO DE COORDENADAS U.T.M.

LADO EST	LADO PV	RUMBO	DISTANCIA	P	COORDENADAS NORTE	COORDENADAS ESTE
				1	1,141,664.17	529,755.04
1	2	N 57°10'22.40" E	11.37m	2	1,141,670.33	529,764.60
2	3	S 30°17'59.36" E	24.72m	3	1,141,648.99	529,777.07
3	4	S 57°10'22.40" W	10.81m	4	1,141,643.13	529,767.99
4	1	N 31°36'27.01" W	24.70m	1	1,141,664.17	529,755.04


LINDEROS.

NORESTE
CASA DE MIGUEL RODRIGUEZ.

SURESTE
SOLAR DE MIGUEL RODRIGUEZ.


NOROESTE
AVENIDA 4.

SUROESTE
CASA DE MARIO GRATEROL.

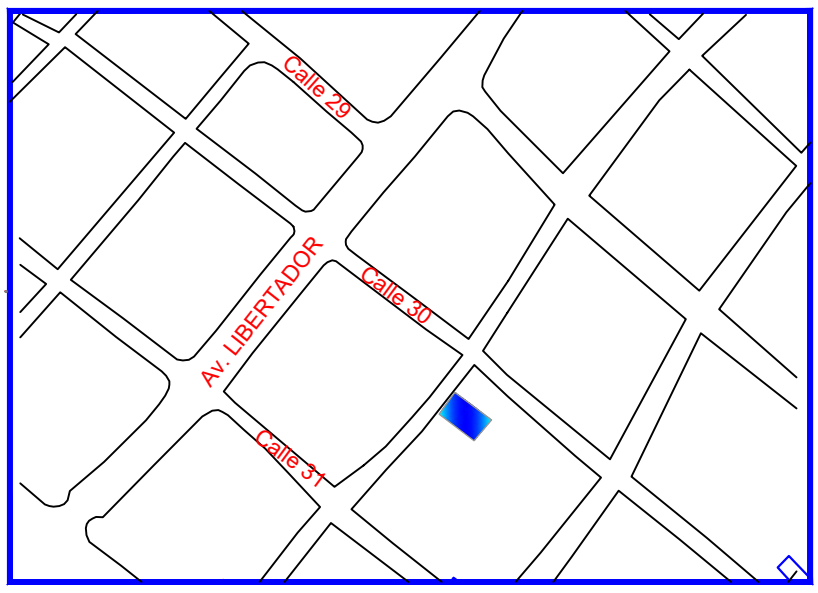

SITUASION RELATIVA S/ESC.

AREA DE TERRENO: 273,81m2.
AREA DE CONSTRUCCION: 215,98m2.

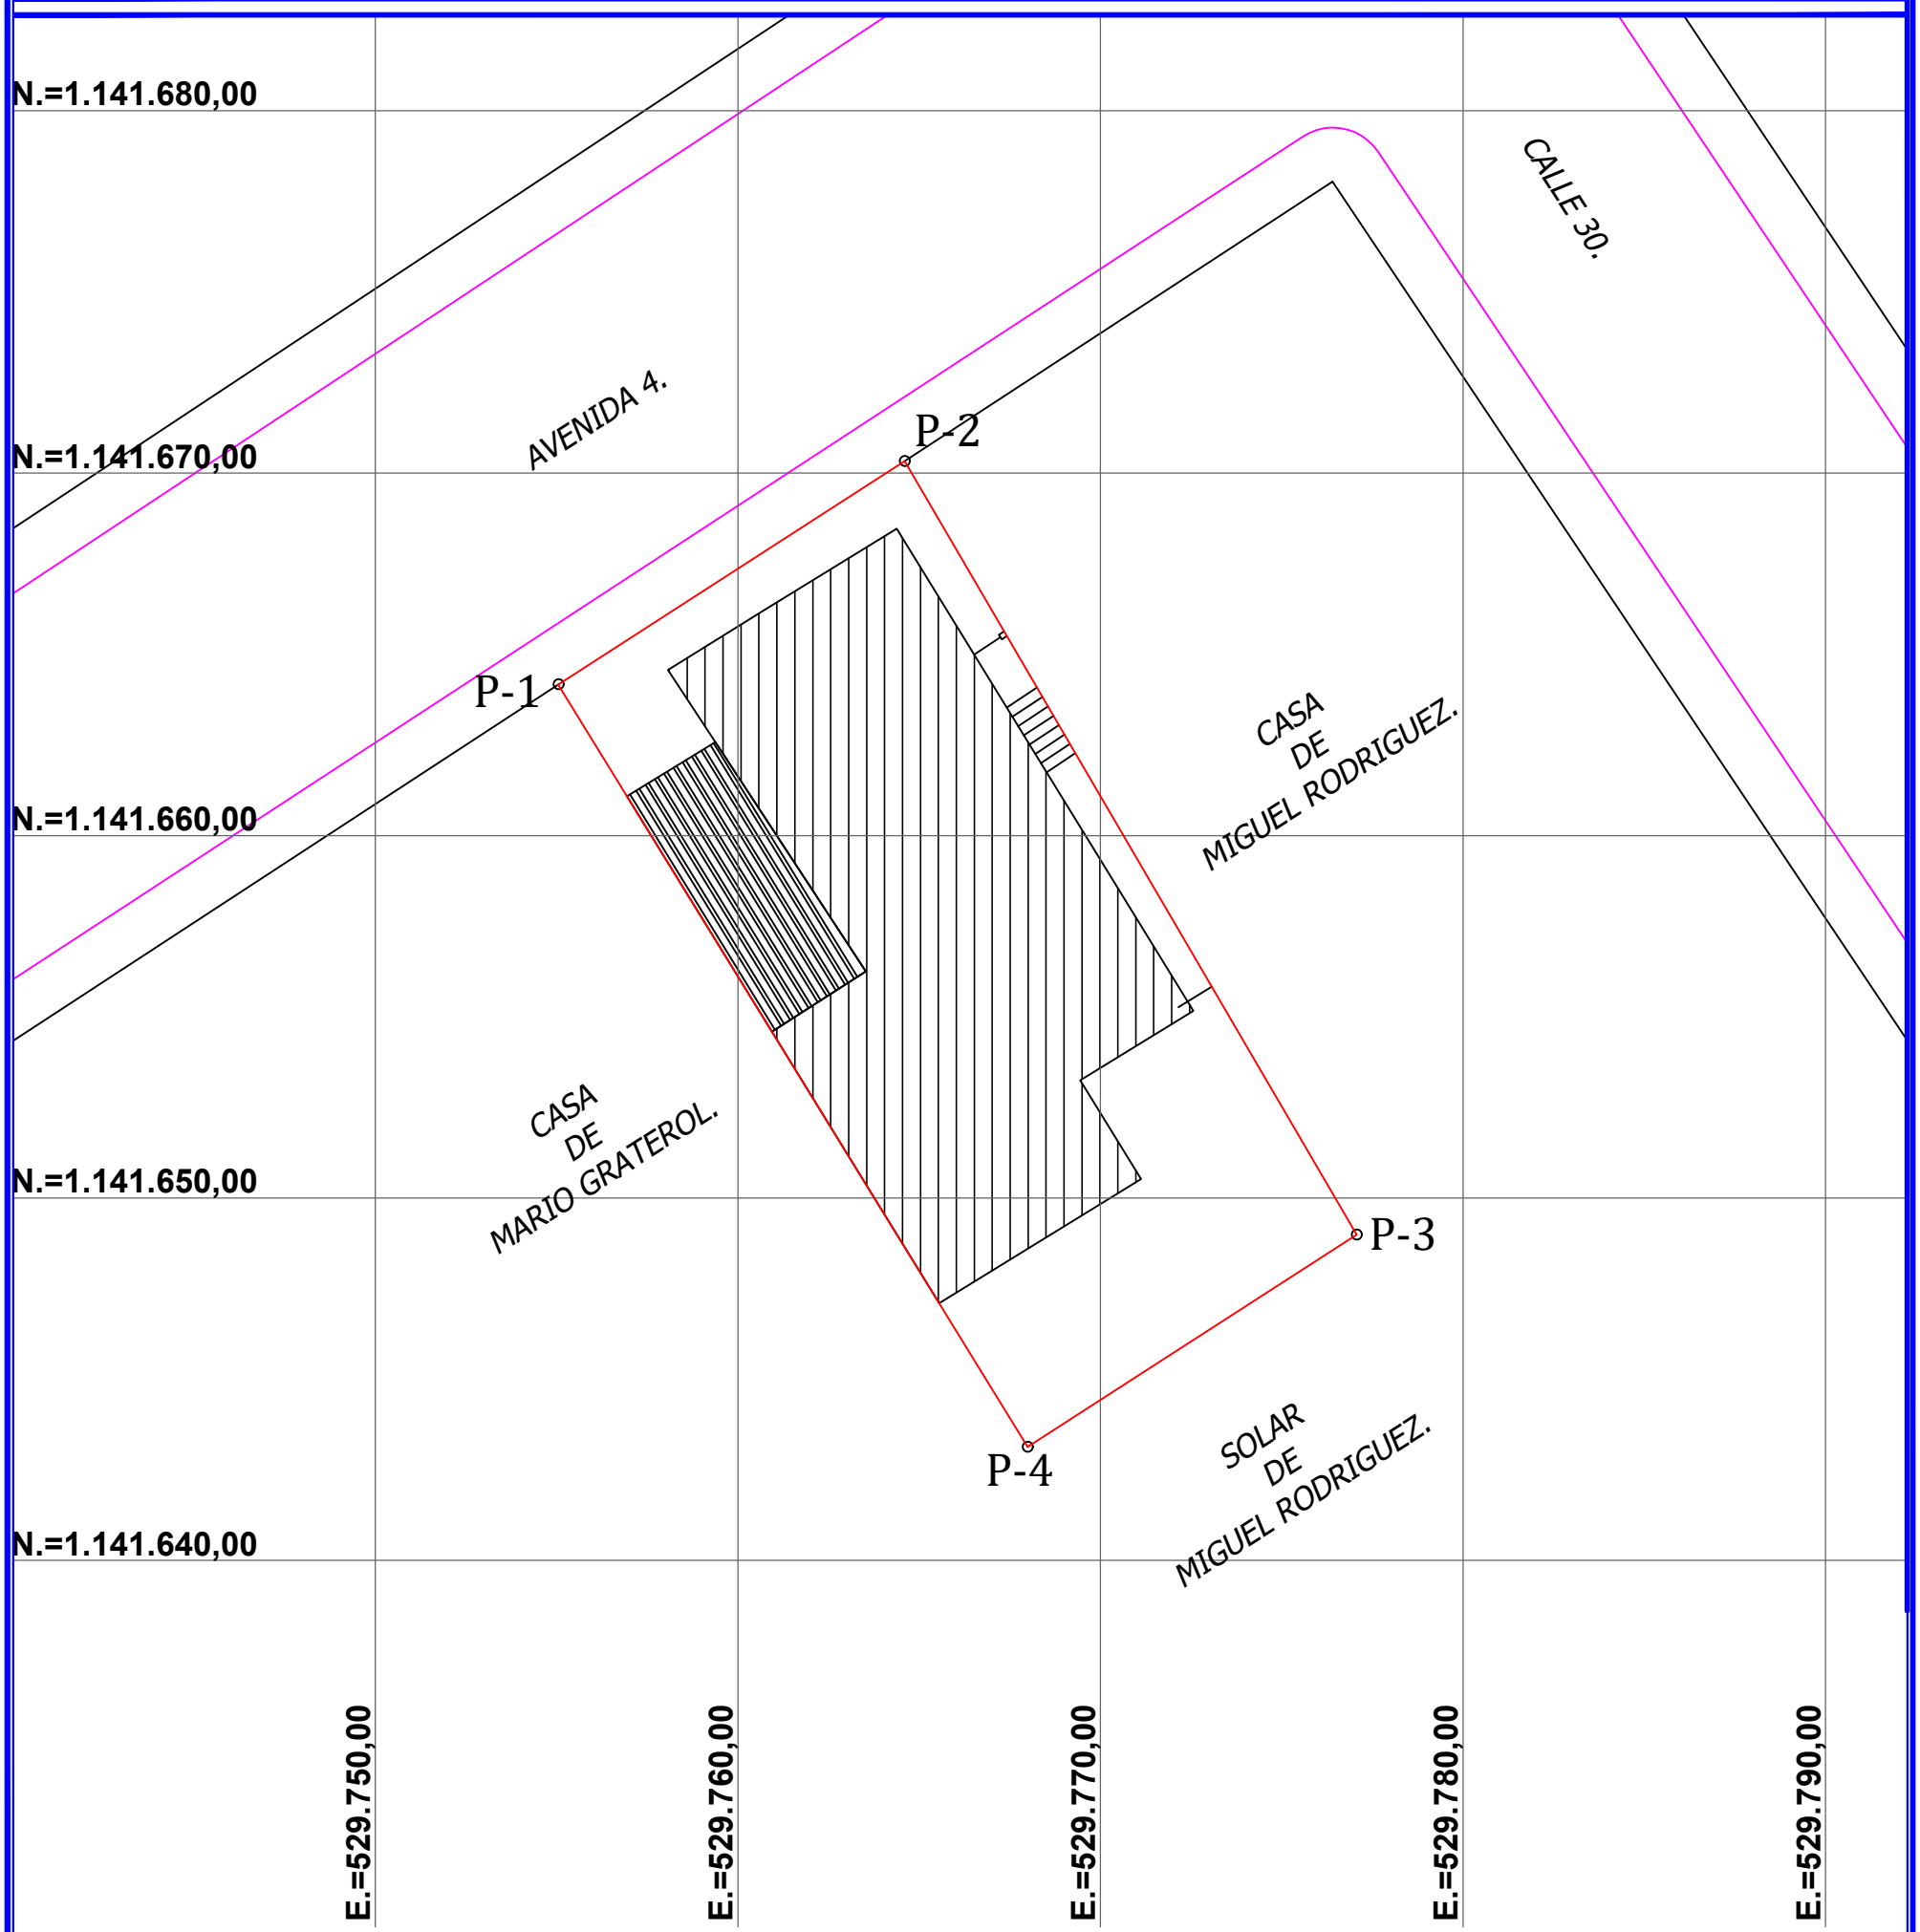

LEVANTAMIENTO POLIGONAL DE LINDEROS

UBICACIÓN:	PROPIEDAD:	LEVANTADO CALCULADO Y DIGITALIZO:	REVISADO:	FECHA:	ESCALA:
AVENIDA 4 ENTRE CALLES 30 Y 31 30-7 MUNICIPIO INDEPENDENCIA ESTADO YARACUY.	ALVARO ARGELIO DIAZ FLOREZ. C.I.: 24.633.787	T.S.U. ANGEL CAMACARO M. CVPT.:N°1260 SOVIT.:N°0050		MAR 2026	1:200