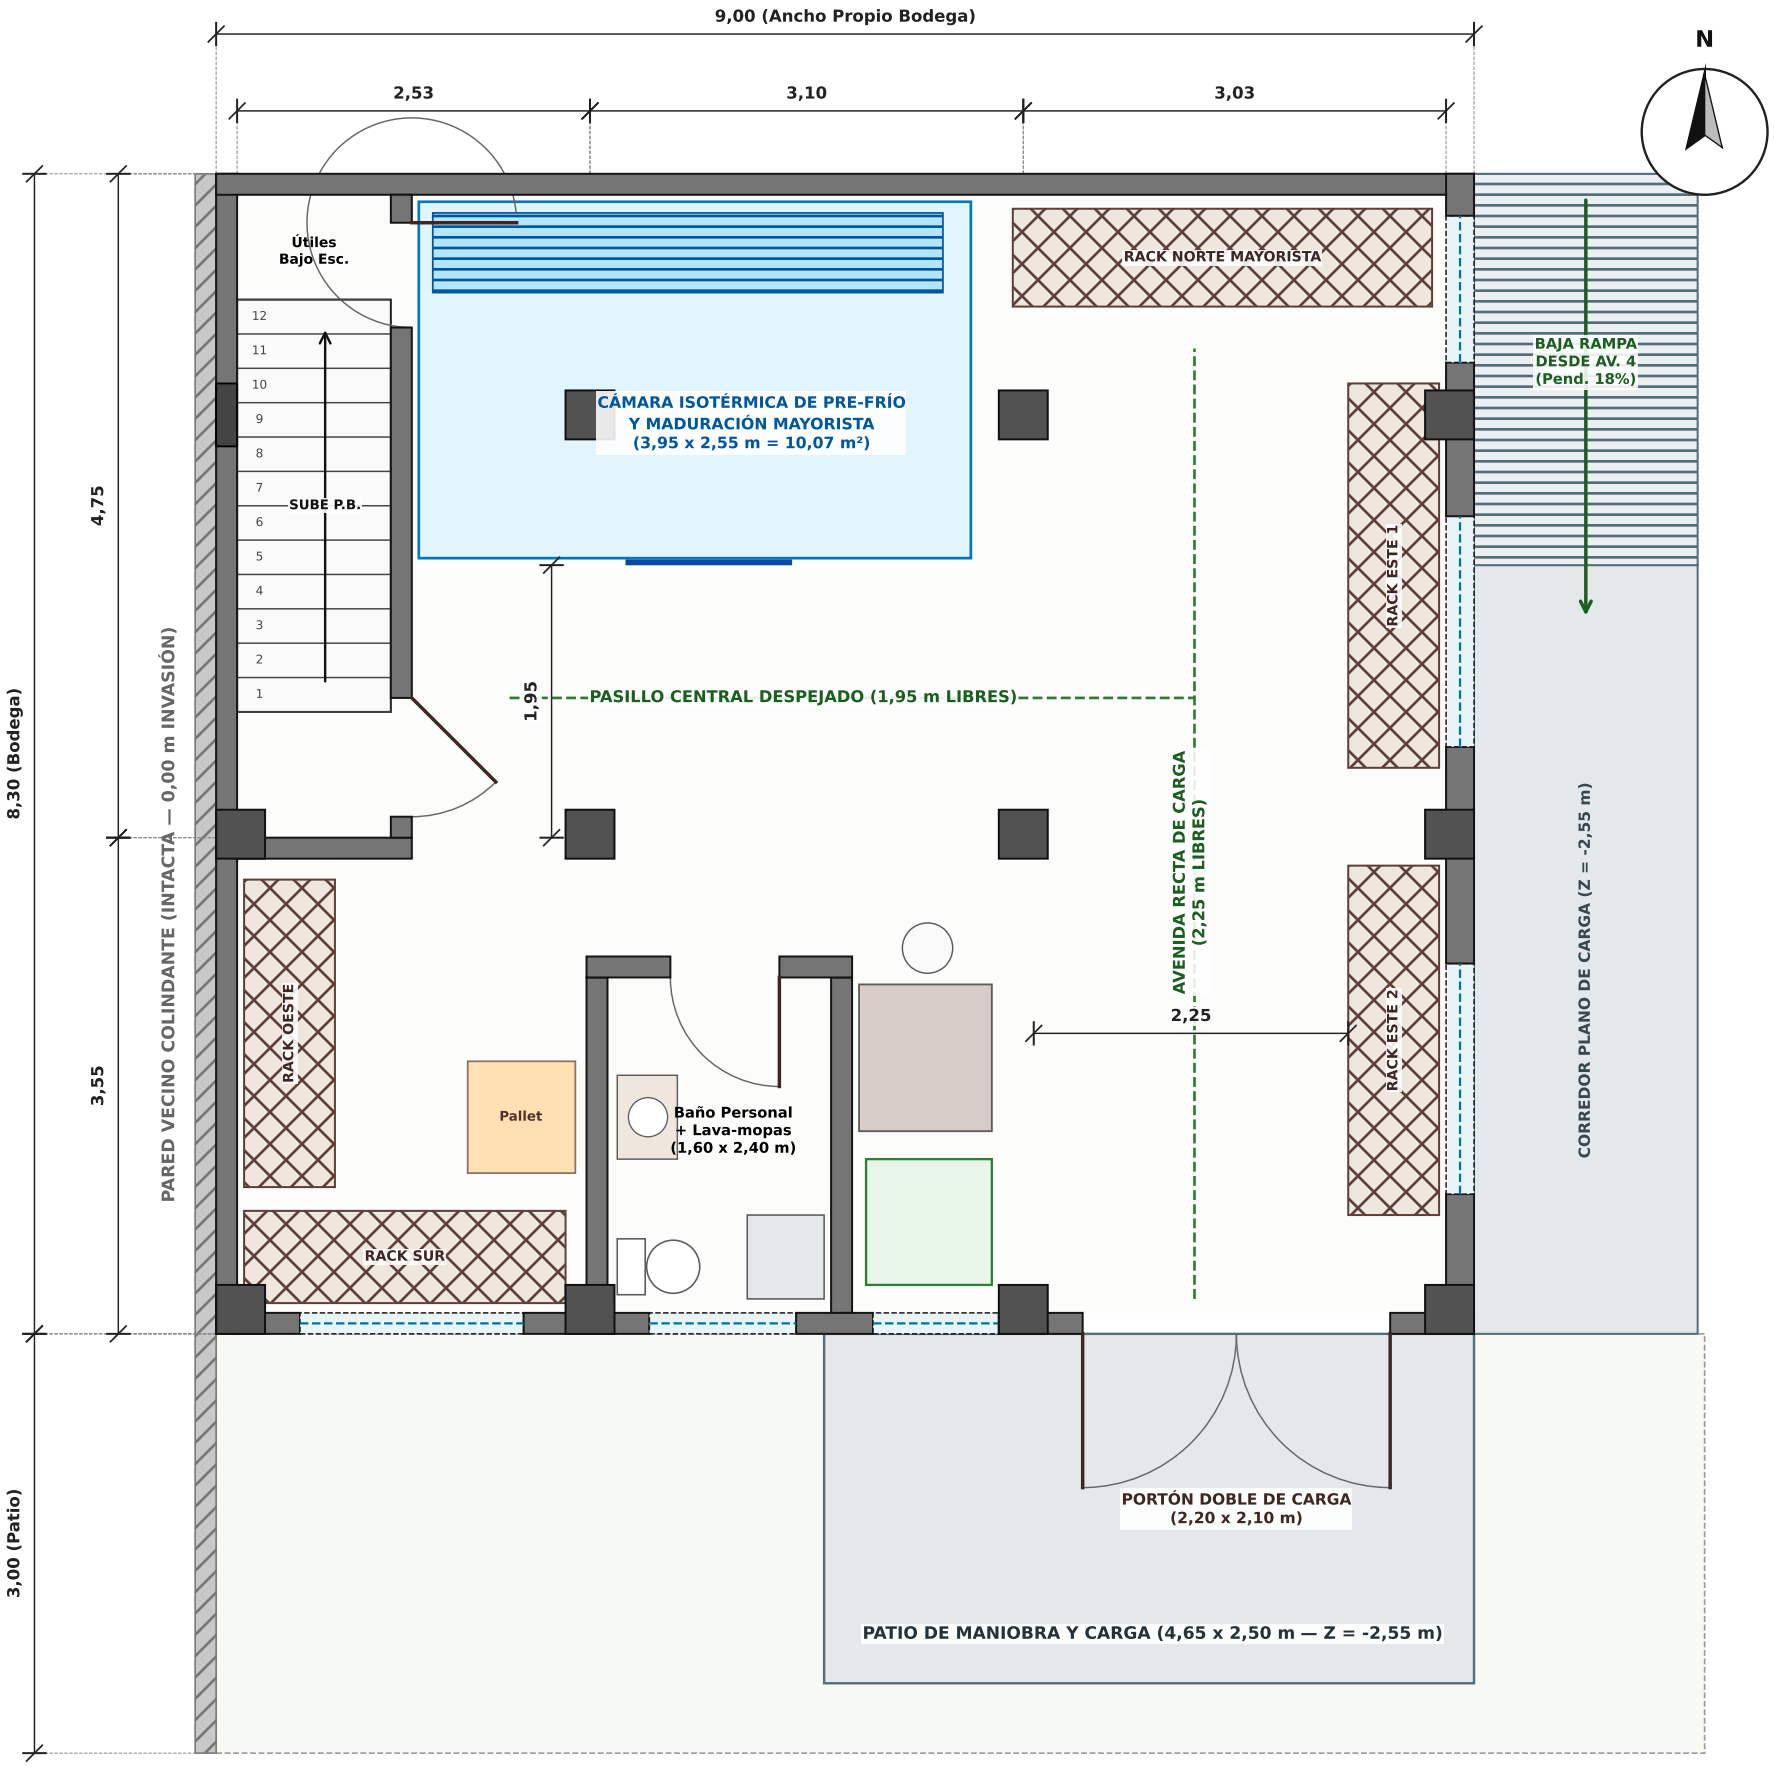



## PLANTA NIVEL SÓTANO — GRAN BODEGA MAYORISTA (COTA N.P.T. = -2,55 m)

**PROGRAMA LOGÍSTICO Y FUNCIONAL — GRAN BODEGA MAYORISTA EN SÓTANO (74,70 m²):**

- Acceso Logístico Independiente: Rampa lateral derecha desde Portón exclusivo en Av. 4 hasta Patio de Maniobra Sur (Z = -2,55 m) y Portón Doble (2,20 m).
- Circulación Ergonómica Despejada: Esclusa cerrada de escalera con puerta metálica a 45° hacia pasillo libre de 1,95 m + Avenida de Carga recta de 2,25 m.
- Cadena de Frío y Almacenaje: Cámara Isotérmica de Pre-Frío y Maduración (10,07 m²) + 5 baterías perimetrales de racks pesados de alta rotación.
- Control y Servicios: Báscula industrial a ras de piso (500 kg) + Mesa de recepción/guías + Baño operativo de personal con lava-mopas.


**PLANO PLANTA ARQUITECTÓNICA — NIVEL SÓTANO BODEGA**

**GRAN BODEGA MAYORISTA COMERCIAL, CÁMARA PRE-FRÍO Y PATIO DE MANIOBRA (Z = -2,55 m).**

**PIEDRA RÚSTICA + MADERA + ACERO NEGRO P3**

**RESPETO ESTRICTO DE LINDEROS (0,00 m INVASIÓN)**

| UBICACIÓN: | PROPIEDAD: | LEVANTADO CALCULADO Y DIGITALIZO: | REVISADO: | FECHA: | ESCALA: |
|---|---|---|---|---|---|
| AVENIDA 4 ENTRE CALLES 30 Y 31 30-7<br>MUNICIPIO INDEPENDENCIA ESTADO YARACUY. | ALVARO ARGELIO DIAZ FLOREZ.<br>C.I.: 24.633.787 | T.S.U. ANGEL CAMACARO M.<br>CVPT.: N° 1260 SOVIT.: N° 0050 | PROYECTO AMPLIACIÓN<br>3 PISOS + BODEGA | NOV 2026 | 1:50 |

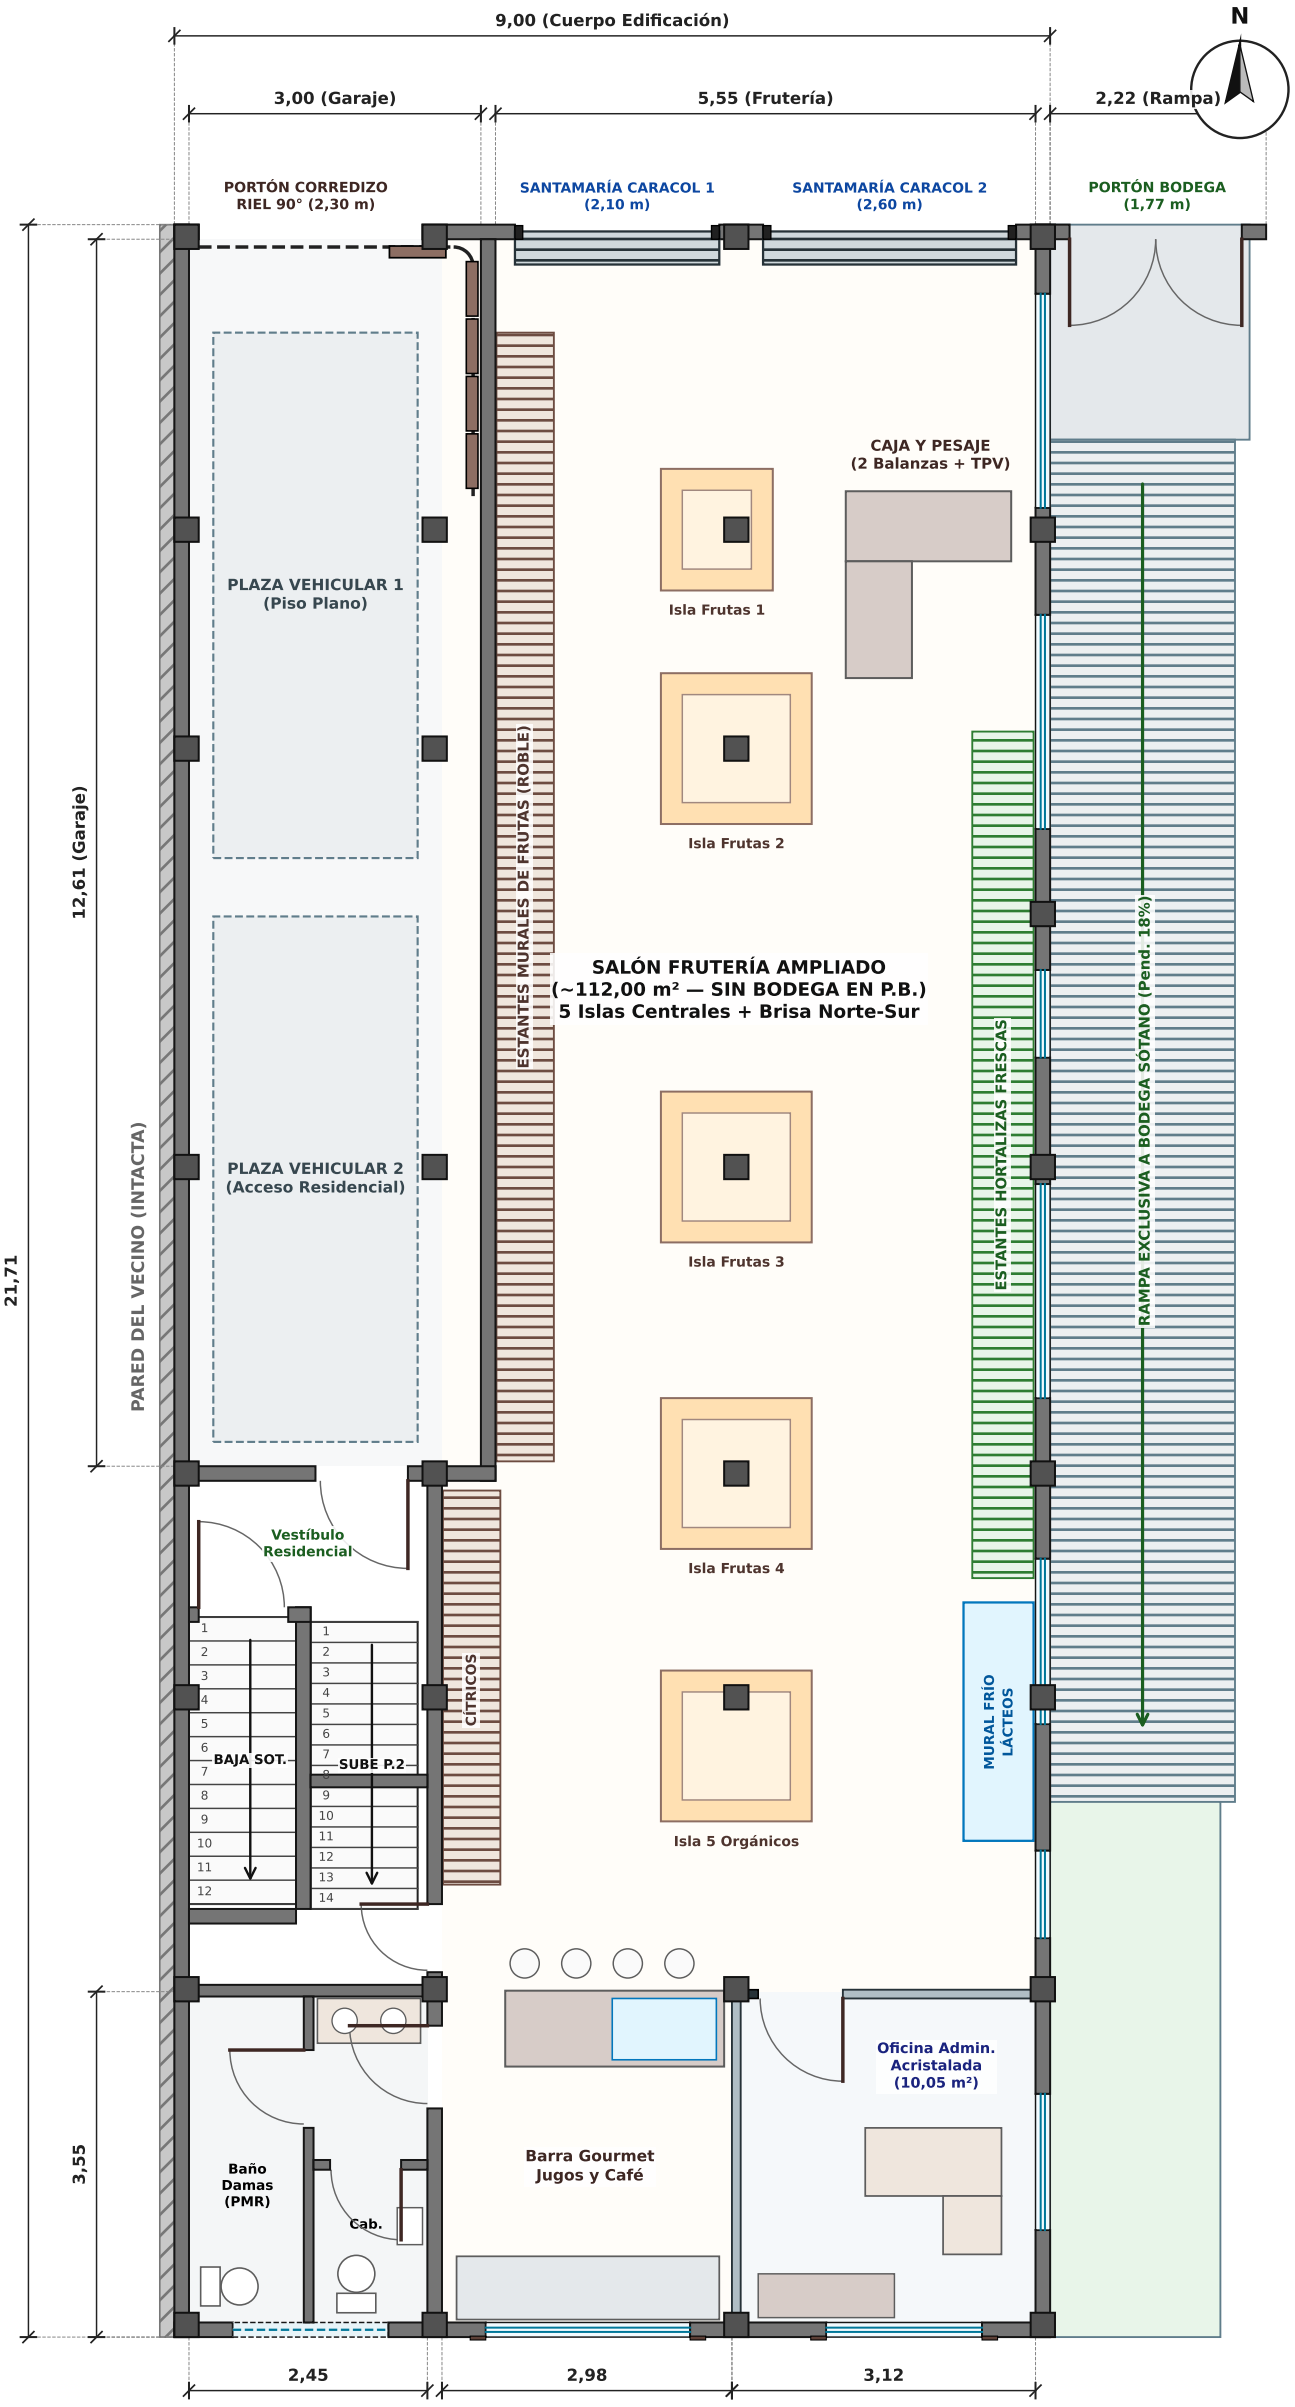


## CUADRO DE AMBIENTES
## PLANTA BAJA (195,39 m²)

### 1. SALÓN FRUTERÍA AMPLIADO — ~112,0 m²

- Eliminada antigua bodega trasera (trasladada al Sótano) ganando amplitud comercial.
- 2 Santamarías de Caracol completas en Av. 4 (carriles U, tambor espiral y faldón).
- 5 Islas centrales + Mural Frío de Lácteos.

### 2. BARRA JUGOS Y CAFÉ SUR — 10,60 m²

- Atención con vitrina fría y 4 taburetes.
- Gran ventanal Sur para luz y brisa N-S.

### 3. OFICINA ADMIN. ACRISTALADA — 10,05 m²

- Cerramiento en hierro negro y cristal con control visual completo de la tienda.

### 4. NÚCLEO BAÑOS SUROESTE — 8,20 m²

- Antebaño doble + Cabinas Damas (PMR) y Caballeros bajo columna húmeda de P2.

### 5. GARAJE Y ESCLUSA ESCALERA — 44,50 m²

- Portón corredizo-articulado sobre riel a 90° (4 hojas en bolsillo + hoja guía visible).
- Vestíbulo cerrado con puerta residencial a P2 y puerta de seguridad a Sótano.

### 6. PORTÓN Y RAMPA BODEGA — Retiro Der.

- Puerta doble en Av. 4 (1,77 m) exclusiva hacia rampa continua (18%) al Sótano.

**PLANTA BAJA — COMERCIO AMPLIADO, GARAJE Y RAMPA BODEGA (N.P.T. ±0,00 m)**


## PLANO PLANTA ARQUITECTÓNICA — PLANTA BAJA

**FRUTERÍA AMPLIADA (~112 m²) + BARRA DE JUGOS + OFICINA + GARAJE Y RAMPA BODEGA.**

PIEDRA RÚSTICA + MADERA + ACERO NEGRO P3

RESPETO ESTRICTO DE LINDEROS (0,00 m INVASIÓN)

| UBICACIÓN: | PROPIEDAD: | LEVANTADO CALCULADO Y DIGITALIZO: | REVISADO: | FECHA: | ESCALA: |
|---|---|---|---|---|---|
| AVENIDA 4 ENTRE CALLES 30 Y 31 30-7<br>MUNICIPIO INDEPENDENCIA ESTADO YARACUY. | ALVARO ARGELIO DIAZ FLOREZ.<br>C.I.: 24.633.787 | T.S.U. ANGEL CAMACARO M.<br>CVPT.: N° 1260 SOVIT.: N° 0050 | PROYECTO AMPLIACIÓN<br>3 PISOS + BODEGA | NOV 2026 | 1:75 |

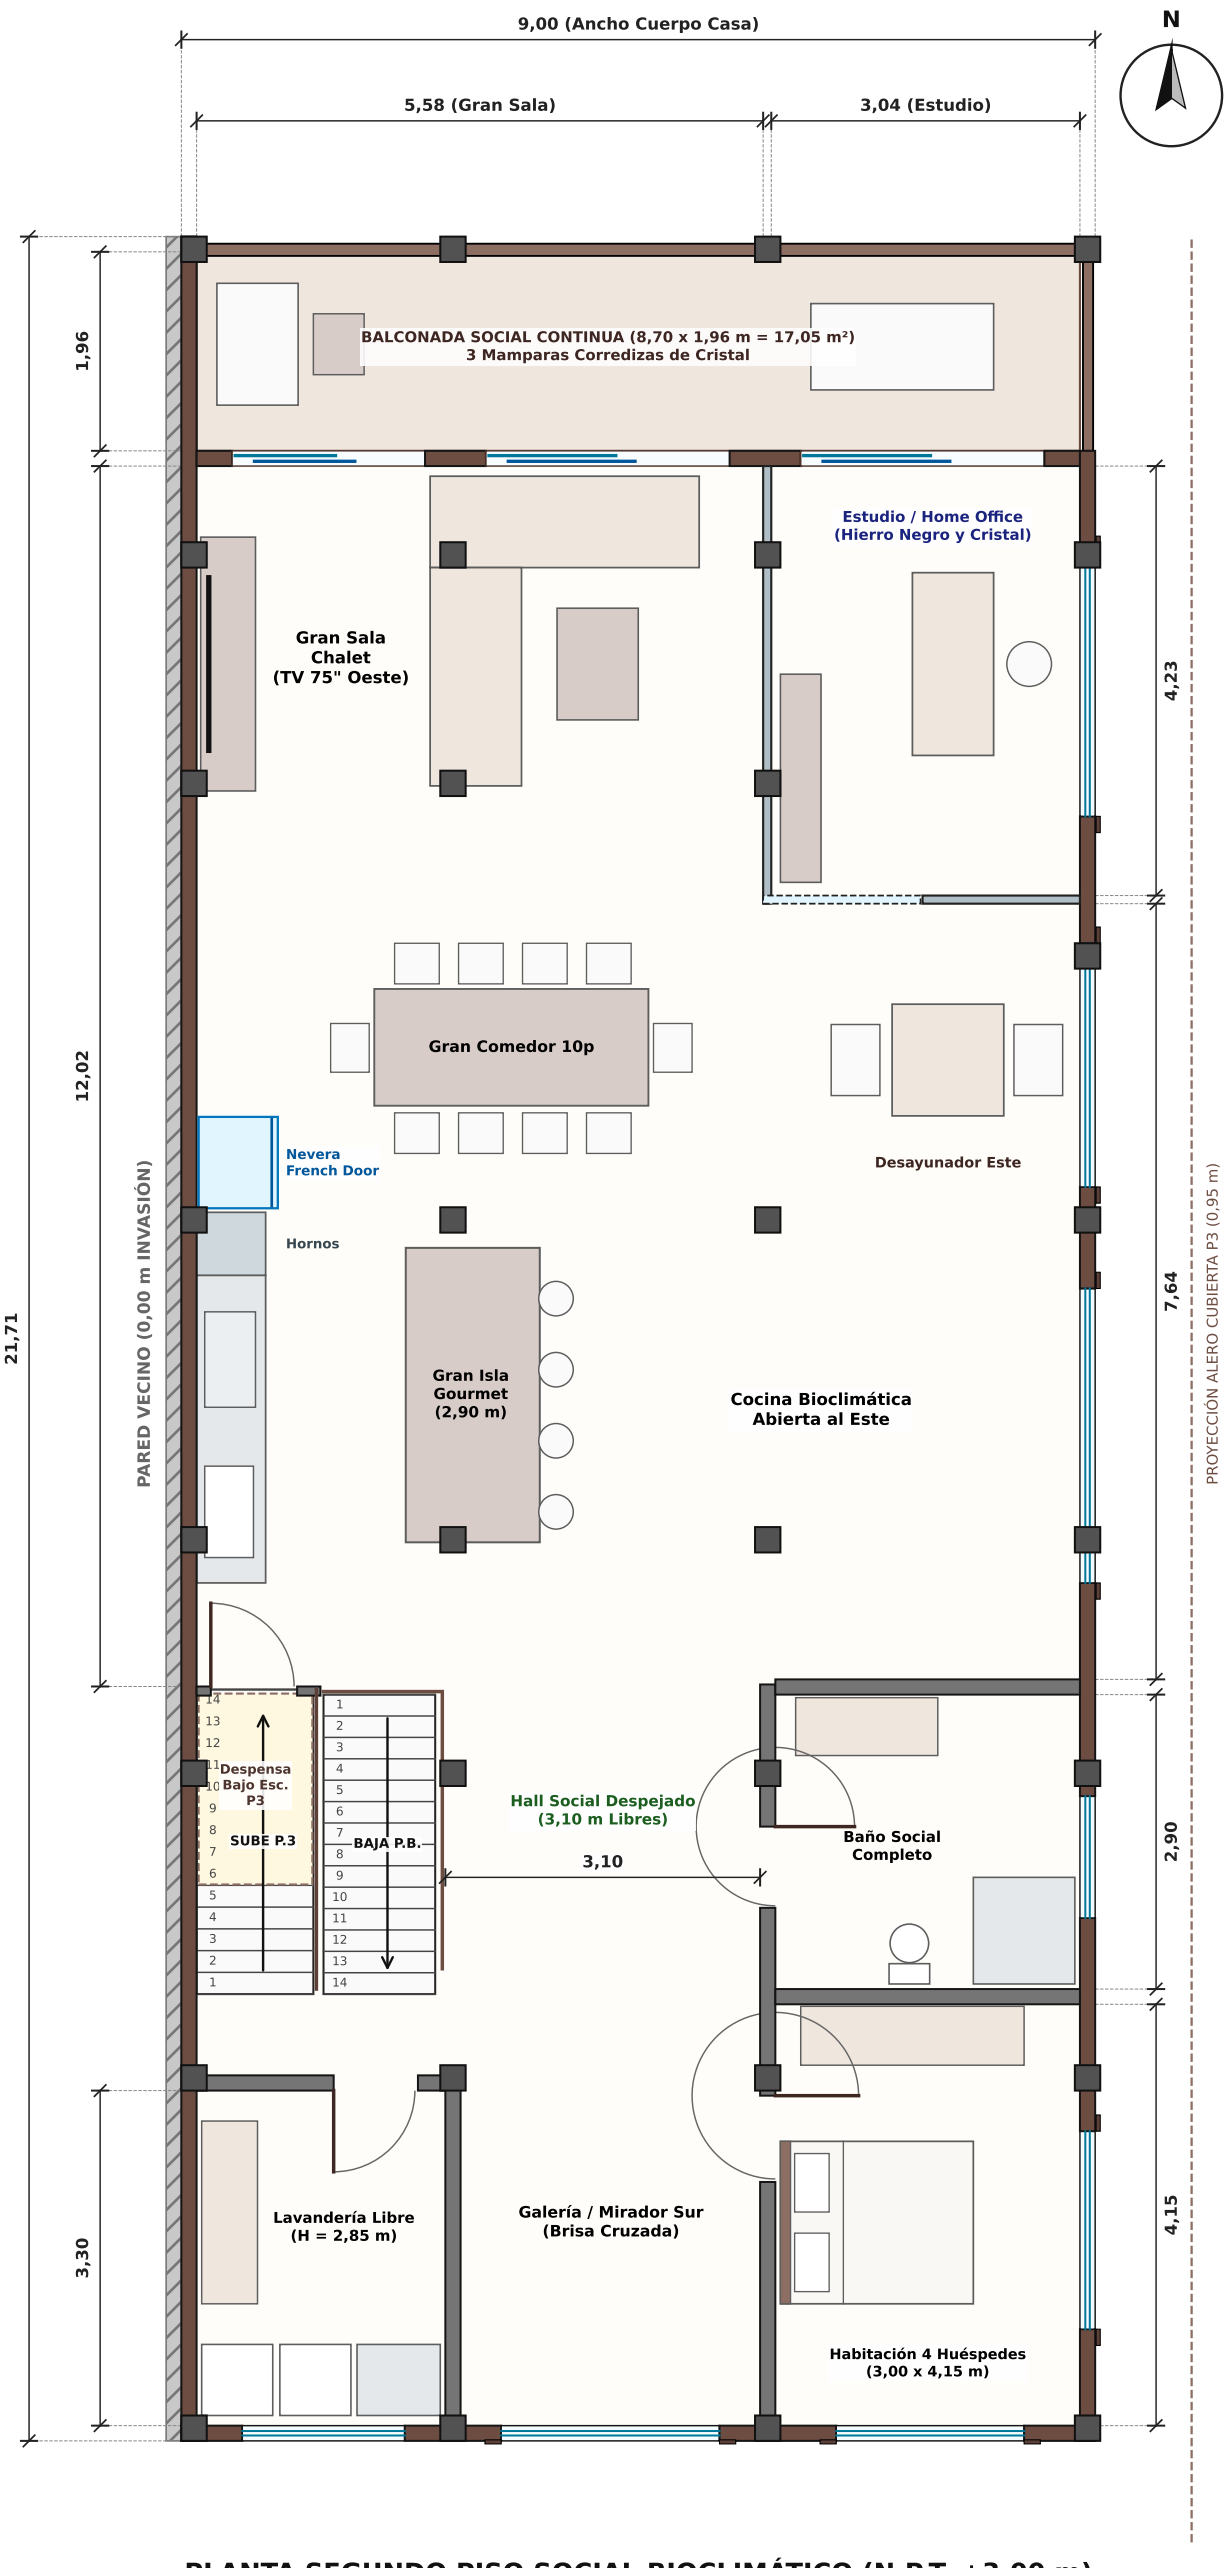


**PLANTA SEGUNDO PISO SOCIAL BIOCLIMÁTICO (N.P.T. +3,00 m)**

## CUADRO DE AMBIENTES SEGUNDO PISO (195,39 m²)

### 1. BALCONADA Y 3 MAMPARAS — 17,05 m²

- Balcón continuo de 8,70 x 1,96 m en Av. 4.
- 3 Mamparas corredizas de cristal templado con doble riel y paso franco al exterior.

### 2. GRAN SALA Y COMEDOR 10p — 64,80 m²

- Planta social abierta a 3 fachadas (N, E, S) para iluminación y brisa alisia directa.
- Comedor 10 puestos + Desayunador Este.

### 3. ESTUDIO ACRISTALADO — 12,85 m²

- Tabique industrial en hierro negro y vidrio corredizo (privacidad sin perder luz).

### 4. COCINA + NEVERA + ISLA — 32,40 m²

- Mesón granito negro + Torre de Hornos.
- Nevera French Door ubicada en nicho Norte (X=0,32..1,10, Y=12,14..13,04).
- Gran Isla central de 2,90 m con 4 bancos.

### 5. DESPENSA BAJO ESCALERA P3 — Aprovech.

- Integrada bajo el tramo alto que sube a P3, liberando un Hall limpio de 3,10 m.

### 6. HAB. 4, BAÑO Y LAVANDERÍA — 29,20 m²

- Habitación 4 Huéspedes / Adulto Mayor + Baño Social + Lavandería libre (H=2,85 m).


## PLANO PLANTA ARQUITECTÓNICA — SEGUNDO PISO SOCIAL

**PLANTA DE DÍA: BALCONADA CON MAMPARAS, SALA, ESTUDIO, COCINA CON ISLA Y HAB. 4 (Z = +3,00 m).**


PIEDRA RÚSTICA + MADERA + ACERO NEGRO P3

RESPETO ESTRICTO DE LINDEROS (0,00 m INVASIÓN)

| UBICACIÓN: | PROPIEDAD: | LEVANTADO CALCULADO Y DIGITALIZO: | REVISADO: | FECHA: | ESCALA: |
|---|---|---|---|---|---|
| AVENIDA 4 ENTRE CALLES 30 Y 31 30-7<br>MUNICIPIO INDEPENDENCIA ESTADO YARACUY. | ALVARO ARGELIO DIAZ FLOREZ.<br>C.I.: 24.633.787 | T.S.U. ANGEL CAMACARO M.<br>CVPT.: N° 1260 SOVIT.: N° 0050 | PROYECTO AMPLIACIÓN<br>3 PISOS + BODEGA | NOV 2026 | 1:75 |

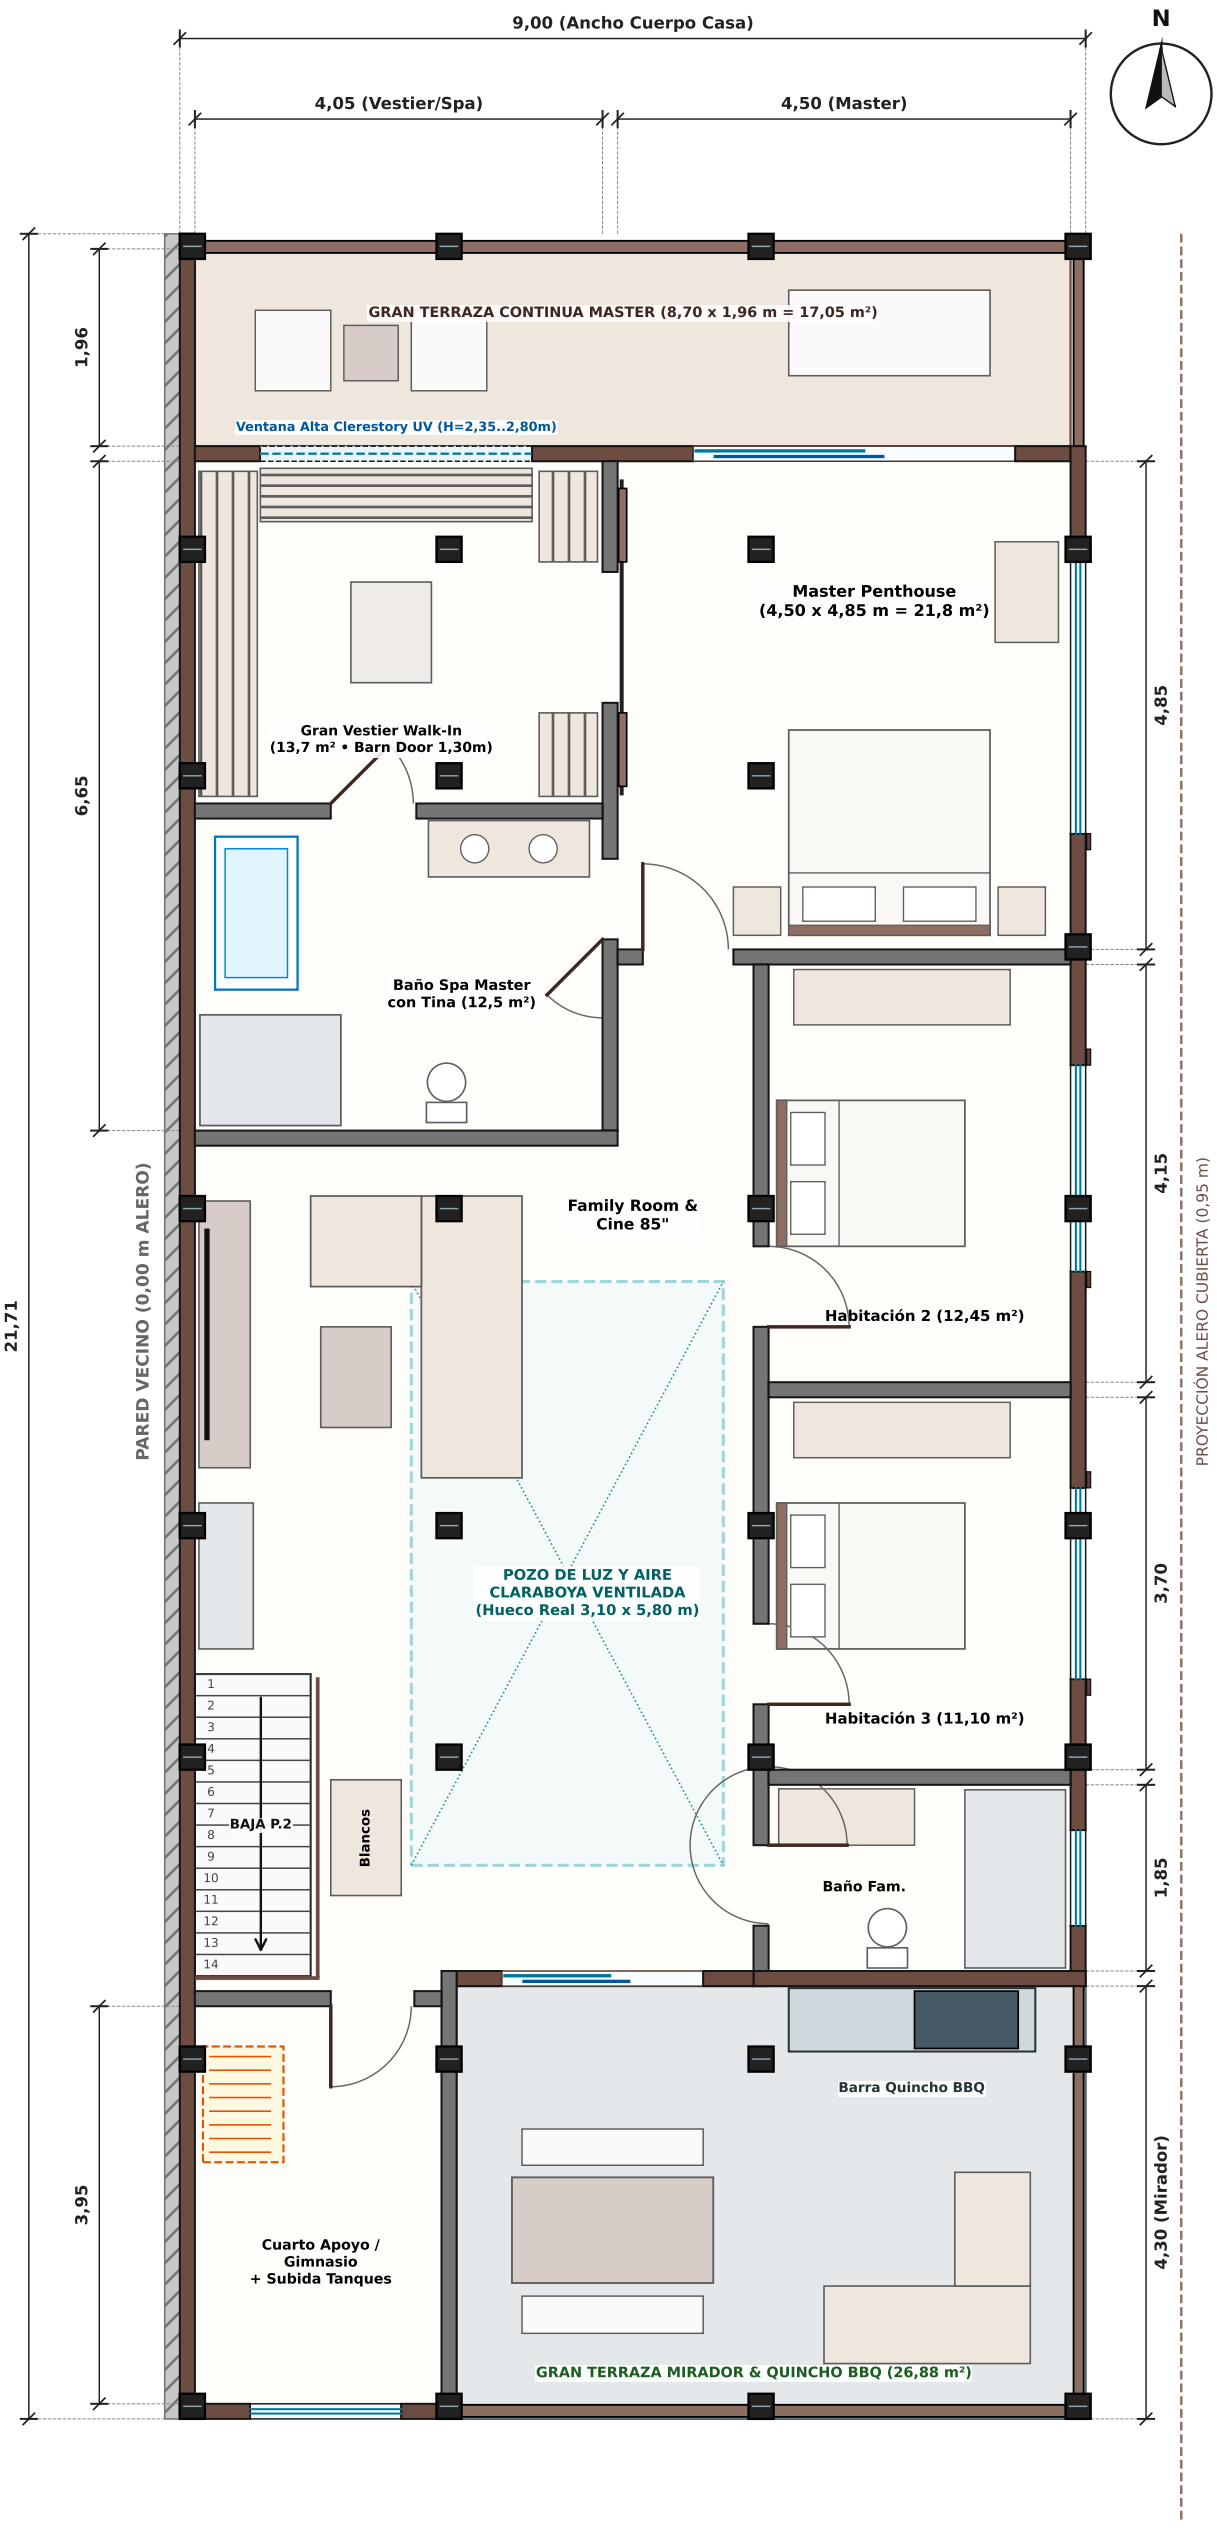


**PLANTA NUEVO TERCER PISO PRIVADO Y MIRADOR BBQ (N.P.T. +6,00 m)**

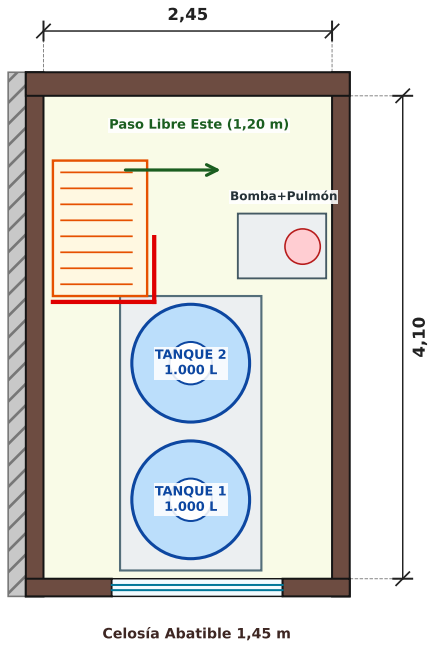


**PLANTA BUHARDILLA RESERVA 2.000 L**
**(N.P.T. +8,68 m — ESC. 1:50)**

## PROGRAMA ARQUITECTÓNICO TERCER PISO (195,39 m²)

- Terraza Continua Master (17,05 m²): Frente unificado sin muro pantalla; acceso exclusivo desde el Dormitorio Master.
- Gran Vestier (13,7 m²) + Clerestory UV: Portal Barn Door (1,30 m), ventana alta (H=2,35..2,80 m) sobre clóset Norte y puerta interna a 45° al Baño Spa con Tina.
- Claraboya Ventilada (3,10 x 5,80 m): Hueco real en cubierta sobre Family Room para luz cenital y efecto chimenea solar.
- Gran Terraza Mirador & BBQ (26,88 m²): Esquina Sureste abierta (sin Hab. 4) con columnas metálicas negras vistas.
- Buhardilla 2.000 L (+8,68 m): 2 tanques x 1.000 L con baranda en 'L' que deja libre el desembarque Este.


## PLANO PLANTA ARQUITECTÓNICA — TERCER PISO Y TANQUES

**PENTHOUSE, CLARABOYA, TERRAZA MIRADOR BBQ (+6,00 m) + BUHARDILLA 2.000 L (+8,68 m).**

**PIEDRA RÚSTICA + MADERA + ACERO NEGRO P3**

**RESPETO ESTRICTO DE LINDEROS (0,00 m INVASIÓN)**

| UBICACIÓN: | PROPIEDAD: | LEVANTADO CALCULADO Y DIGITALIZO: | REVISADO: | FECHA: | ESCALA: |
|---|---|---|---|---|---|
| AVENIDA 4 ENTRE CALLES 30 Y 31 30-7<br>MUNICIPIO INDEPENDENCIA ESTADO YARACUY. | ALVARO ARGELIO DIAZ FLOREZ.<br>C.I.: 24.633.787 | T.S.U. ANGEL CAMACARO M.<br>CVPT.: N° 1260 SOVIT.: N° 0050 | PROYECTO AMPLIACIÓN<br>3 PISOS + BODEGA | NOV 2026 | 1:75 / 1:50 |

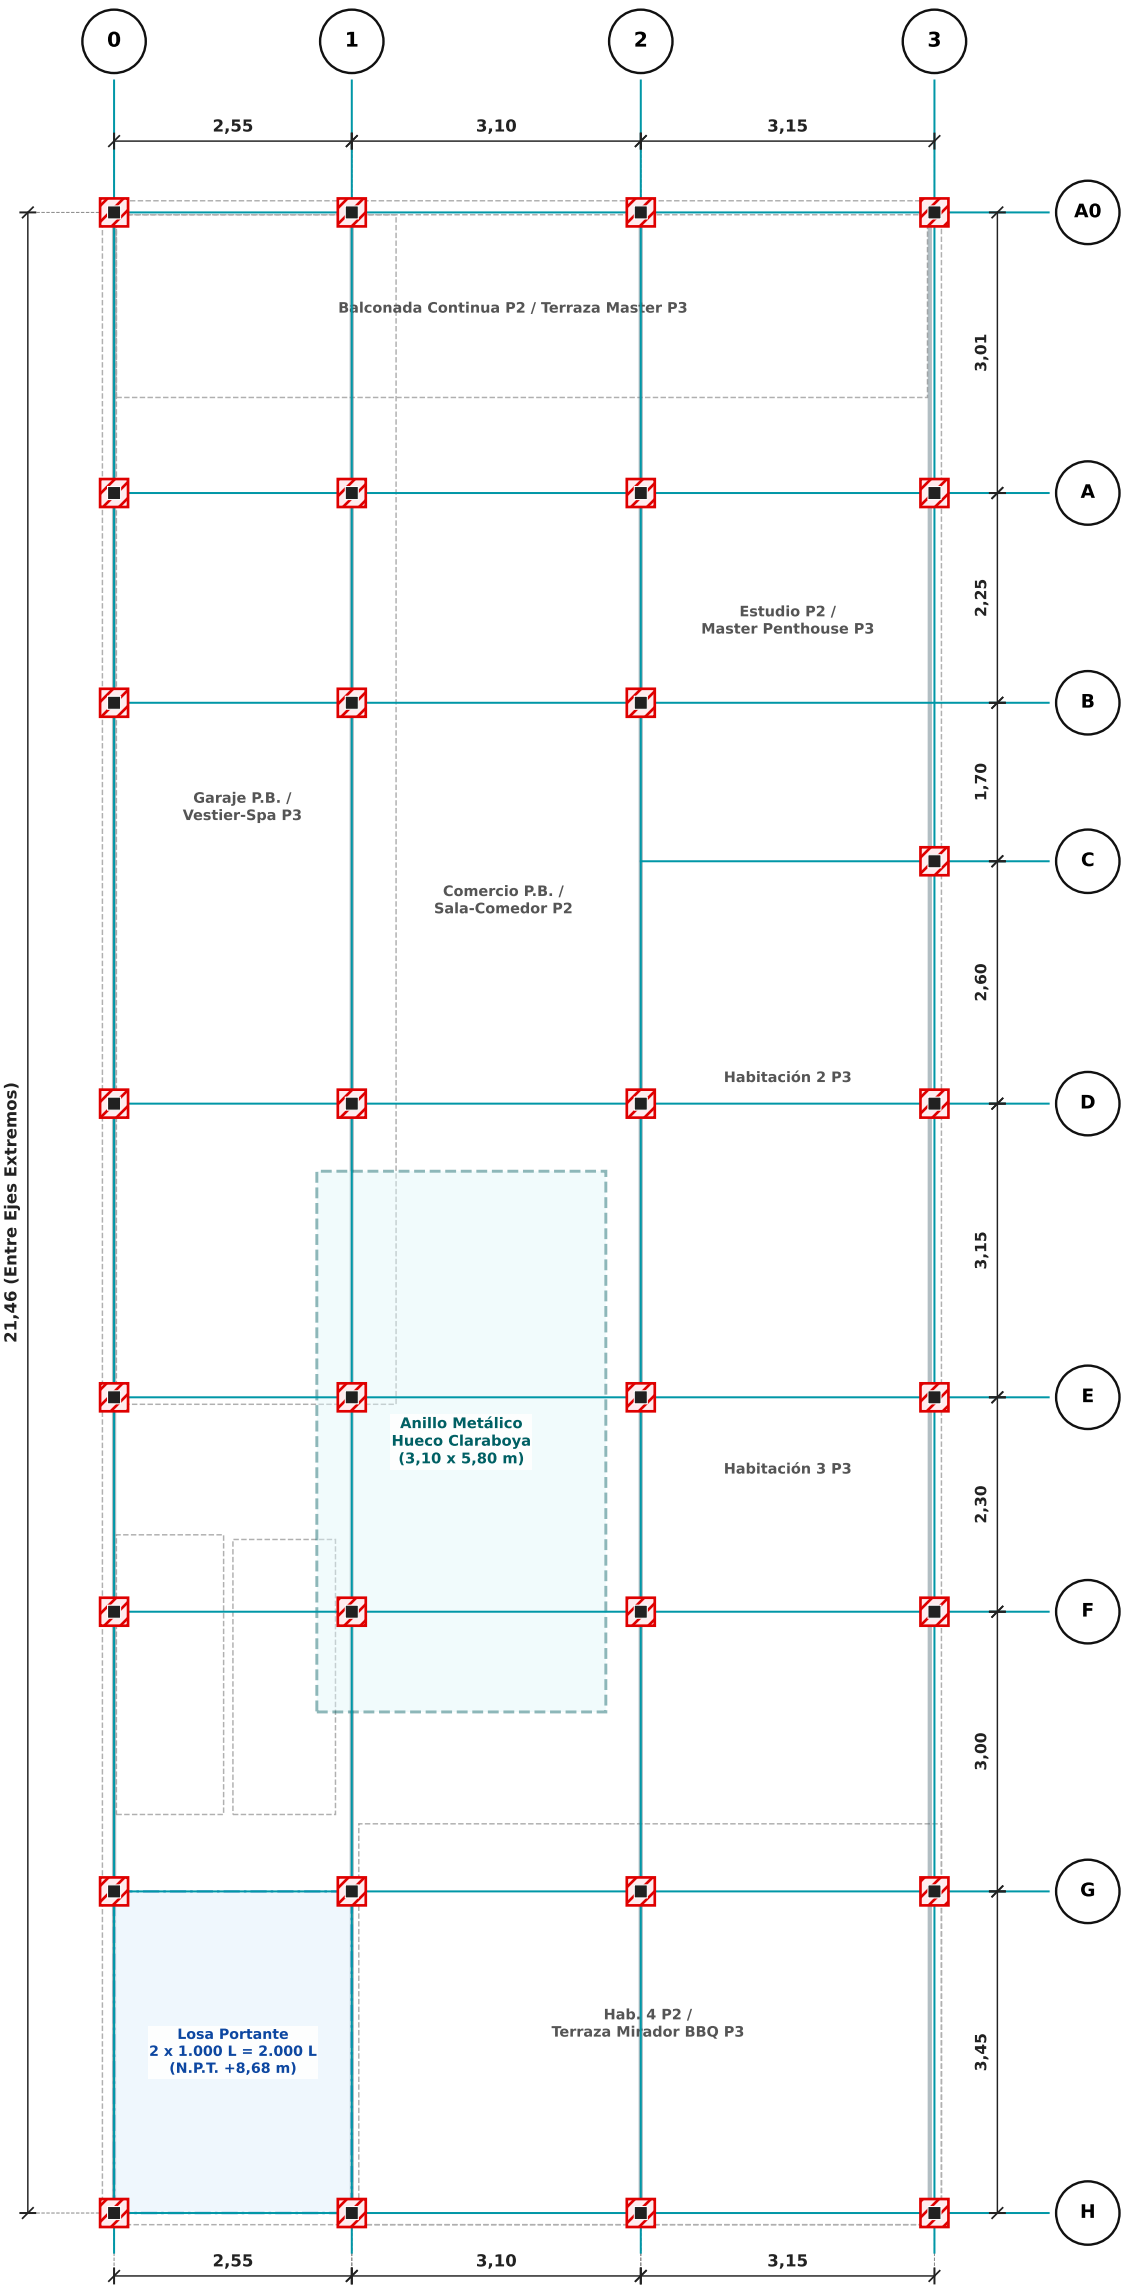


**PLANTA ESTRUCTURAL P.B., P2 Y NUEVO P3**
**(32 NODOS: CONCRETO 25x25 cm EN P.B./P2 + ACERO NEGRO EN P3)**

## MEMORIA Y ESPECIFICACIONES ESTRUCTURALES (3 PISOS + SÓTANO)

**1. SÓTANO BODEGA MAYORISTA (-2,55 m):**

- 12 columnas de 35 x 35 cm en concreto armado ($f'c$ = 280 kg/cm²) + muros de contención N/O.
- Cero contacto con fundación vecina (X >= 0,15 m).

**2. PLANTA BAJA Y SEGUNDO PISO (0,00 / +3,00 m):**


- 32 columnas de 25 x 25 cm en retícula ortogonal continua (Ejes 0, 1, 2, 3 x A0..H) + vigas 25x40 cm.

**3. TERCER PISO LIVIANO EN ACERO (+6,00 m):**

- Entrepiso colaborante Steel Deck (e = 15 cm) sobre vigas metálicas negras para reducir masa sísmica en el nivel superior.
- 32 Columnas metálicas estructurales negras 25x25 cm / IPE con placas base empernadas.

**4. CUBIERTA 32°, CLARABOYA Y 2.000 L (+8,68 m):**

- Anillo metálico perimetral en hueco de claraboya (3,10 x 5,80 m) + Losa portante para 2.000 kg.

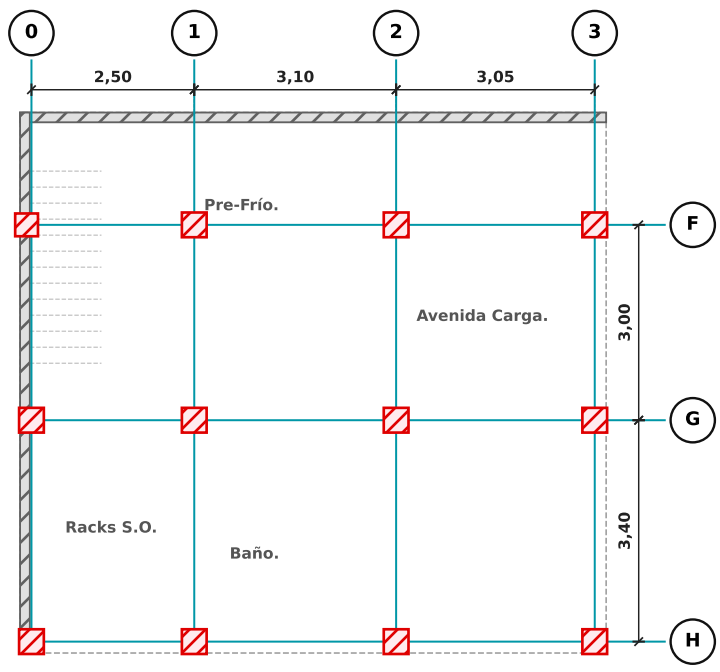


**PLANTA SÓTANO BODEGA (12 APOYOS 35 x 35 cm)**

## PLANO DISTRIBUCIÓN DE COLUMNAS Y EJES ESTRUCTURALES

**PIEDRA RÚSTICA + MADERA + ACERO NEGRO P3**

**SÓTANO (35x35 cm) • P.B. Y P2 CONCRETO (25x25 cm) • P3 COLUMNAS METÁLICAS NEGRAS + STEEL DECK.**


**RESPETO ESTRICTO DE LINDEROS (0,00 m INVASIÓN)**

| UBICACIÓN: | PROPIEDAD: | LEVANTADO CALCULADO Y DIGITALIZO: | REVISADO: | FECHA: | ESCALA: |
|---|---|---|---|---|---|
| AVENIDA 4 ENTRE CALLES 30 Y 31 30-7<br>MUNICIPIO INDEPENDENCIA ESTADO YARACUY. | ALVARO ARGELIO DIAZ FLOREZ.<br>C.I.: 24.633.787 | T.S.U. ANGEL CAMACARO M.<br>CVPT.: N° 1260 SOVIT.: N° 0050 | PROYECTO AMPLIACIÓN<br>3 PISOS + BODEGA | NOV 2026 | 1:75 |


# REPÚBLICA BOLIVARIANA DE VENEZUELA
## MUNICIPIO INDEPENDENCIA YARACUY

**PROYECTO AMPLIACIÓN: 3 PISOS CHALET ALPINO & COMERCIO**


**ELEVACIONES, RAMPA Y CLARABOYA | LÁMINA 6 / 7**

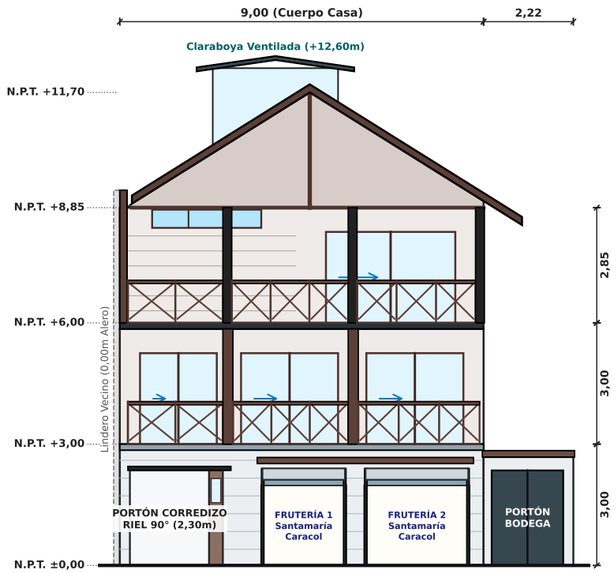


**FACHADA PRINCIPAL AVENIDA 4**
**(PORTÓN BODEGA, COMERCIO, PISO 2 Y PENTHOUSE P3 CON CLERESTORY)**

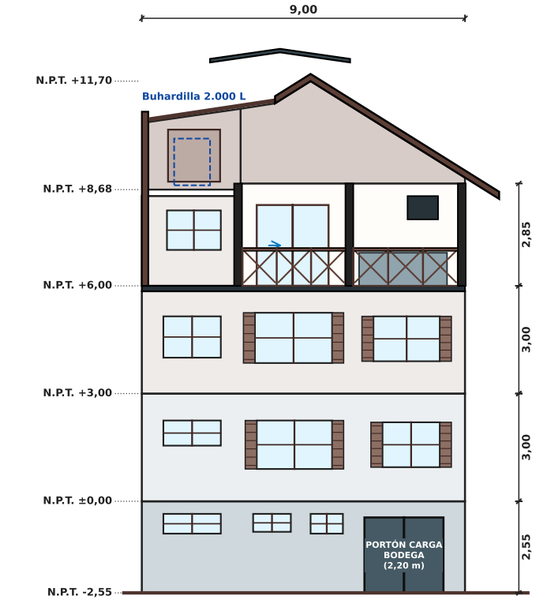


**FACHADA POSTERIOR SUR**
**(BODEGA SÓTANO, JUGOS P.B., PISO 2, TERRAZA MIRADOR BBQ Y 2.000 L)**

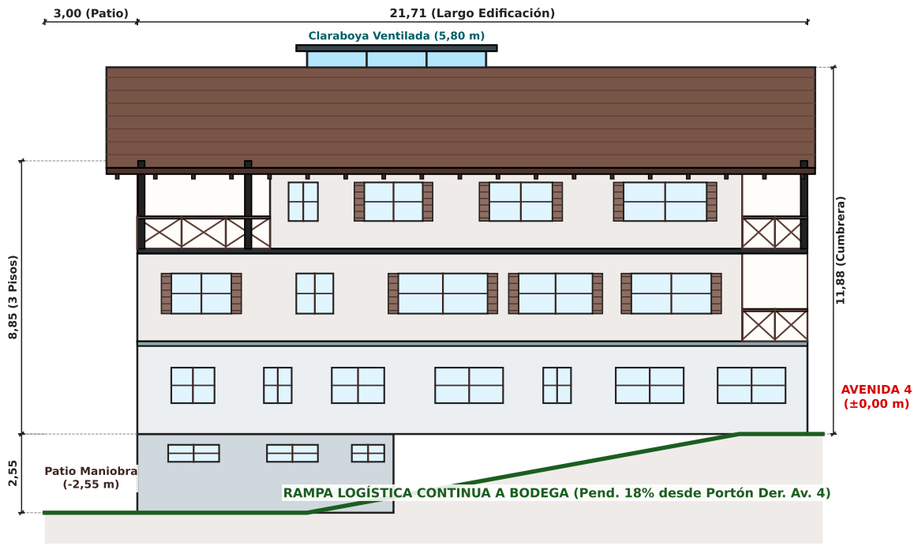


**ELEVACIÓN LATERAL ESTE — SÓTANO BODEGA, 3 PISOS, TERRAZA MIRADOR, CLARABOYA Y RAMPA LOGÍSTICA**

## PLANO DE FACHADAS Y ELEVACIONES ARQUITECTÓNICAS (3 PISOS + SÓTANO)

**FACHADA PRINCIPAL AV. 4 • FACHADA POSTERIOR SUR • ELEVACIÓN LATERAL CON RAMPA Y CLARABOYA.**

**PIEDRA + MADERA + ACERO NEGRO P3 + CLARABOYA VENTILADA**

**RESPETO ESTRICTO DE MEDIANERA (0,00 m INVASIÓN LINDERO VECINO)**

| UBICACIÓN: | PROPIEDAD: | LEVANTADO CALCULADO Y DIGITALIZO: | REVISADO: | FECHA: | ESCALA: |
|---|---|---|---|---|---|
| AVENIDA 4 ENTRE CALLES 30 Y 31 30-7<br>MUNICIPIO INDEPENDENCIA ESTADO YARACUY. | ALVARO ARGELIO DIAZ FLOREZ.<br>C.I.: 24.633.787 | T.S.U. ANGEL CAMACARO M.<br>CVPT.: N° 1260 SOVIT.: N° 0050 | PROYECTO AMPLIACIÓN<br>3 PISOS + BODEGA | NOV 2026 | 1:75 / 1:100 |

# REPÚBLICA BOLIVARIANA DE VENEZUELA
## MUNICIPIO INDEPENDENCIA YARACUY

**PROYECTO AMPLIACIÓN: 3 PISOS CHALET ALPINO & COMERCIO**

**MODELO MAESTRO VERIFICADO | LÁMINA 7 / 7**

### CUADRO DE COORDENADAS U.T.M.

| LADO | | RUMBO | DISTANCIA | P | COORDENADAS | |
|---|---|---|---|---|---|---|
| EST | PV | | | | NORTE | ESTE |
| | | | | 1 | 1.141.664,17 | 529.755,04 |
| 1 | 2 | N 57°10'22,40" E | 11,37 m | 2 | 1.141.670,33 | 529.764,60 |
| 2 | 3 | S 30°17'59,36" E | 24,72 m | 3 | 1.141.648,99 | 529.777,07 |
| 3 | 4 | S 57°10'22,40" W | 10,81 m | 4 | 1.141.643,13 | 529.767,99 |
| 4 | 1 | N 31°36'27,01" W | 24,70 m | 1 | 1.141.664,17 | 529.755,04 |

**ÁREA DE TERRENO POLIGONAL: 273,81 m².**

**ÁREA TOTAL CONSTRUIDA TECHADA: 673,11 m² (+ Rampa y Patio Maniobra).**

Sótano 74,70 | P.B. 195,39 | 2do Piso 195,39 | 3er Piso 195,39 | Buhardilla 12,24 m²

### LINDEROS.

**NORESTE**

CASA
DE
MIGUEL RODRIGUEZ.

**SURESTE**


SOLAR
DE
MIGUEL RODRIGUEZ.

**NOROESTE**

AVENIDA 4.

**SUROESTE**

CASA
DE
MARIO GRATEROL.

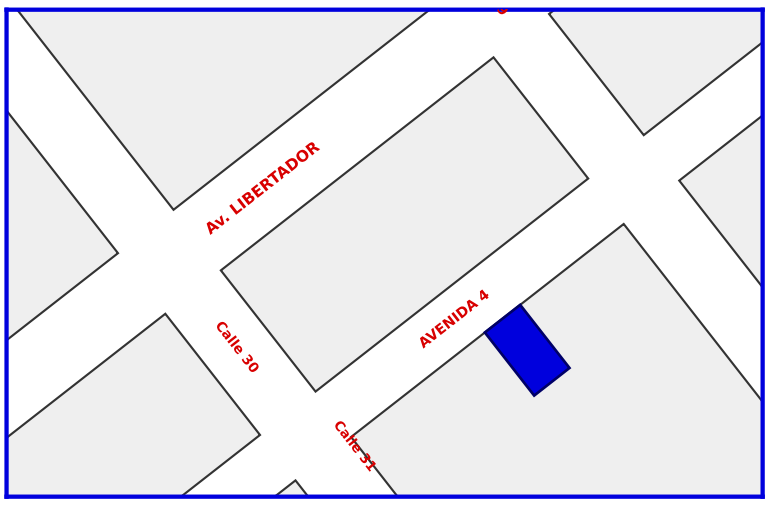


**SITUACIÓN RELATIVA S/ESC.**




## LEVANTAMIENTO POLIGONAL DE LINDEROS

**COORDENADAS U.T.M., CUADRO DE ÁREAS (3 PISOS + BODEGA), IMPLANTACIÓN Y SITUACIÓN.**

**PIEDRA RÚSTICA + MADERA + ACERO NEGRO P3**

**RESPETO ESTRICTO DE LINDEROS (0,00 m INVASIÓN)**

| UBICACIÓN: | PROPIEDAD: | LEVANTADO CALCULADO Y DIGITALIZO: | REVISADO: | FECHA: | ESCALA: |
|---|---|---|---|---|---|
| AVENIDA 4 ENTRE CALLES 30 Y 31 30-7<br>MUNICIPIO INDEPENDENCIA ESTADO YARACUY. | ALVARO ARGELIO DIAZ FLOREZ.<br>C.I.: 24.633.787 | T.S.U. ANGEL CAMACARO M.<br>CVPT.: N° 1260 SOVIT.: N° 0050 | PROYECTO AMPLIACIÓN<br>3 PISOS + BODEGA | NOV 2026 | 1:200 |